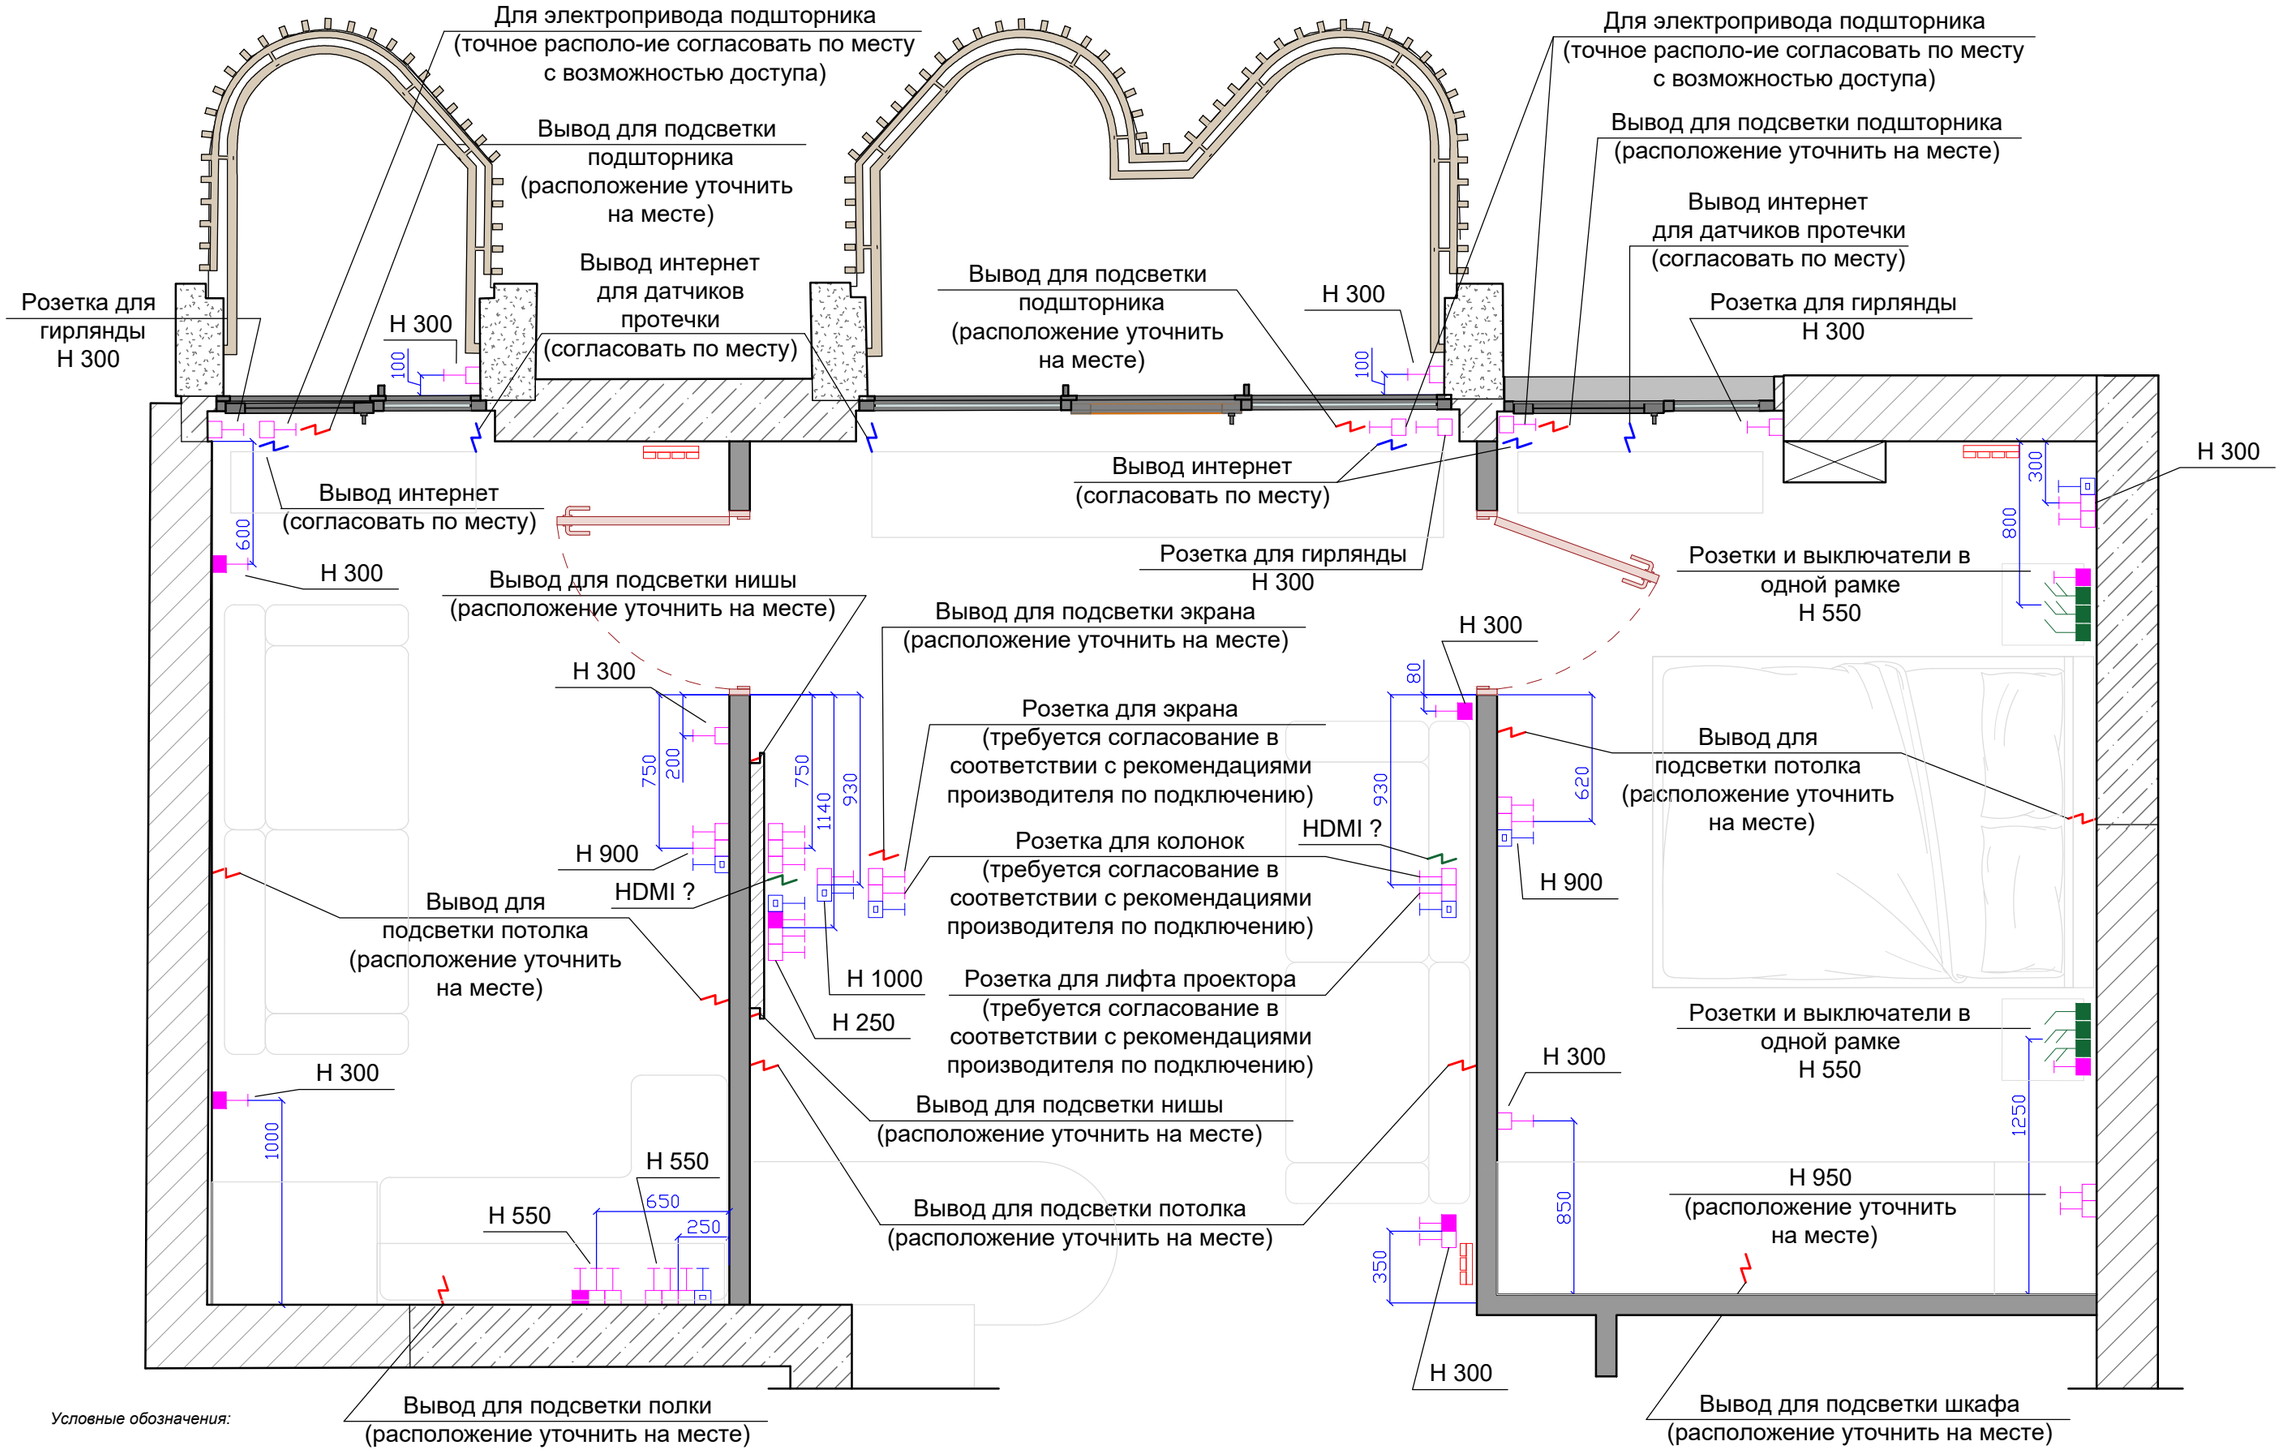

Условные обозначения:

Розетка

Розетка интернет двойная RJ 45

Розетка интернет

Розетка + USB + Type-C

Вывод

Вывод HDMI

Вывод слаботочки

Выключатель одноклавишный

Выключатель одноклавишный проходной

Выключатель двухклавишный

Выключатель двухклавишный проходной

изм.	кол.у	лист	Nдок.	подп.	дата		стадия	лист	листов
						Квартира 60.1 м2	РП		
Исполнил									
Проверил						План электрики лист 2			
Заказчик									