


Ведомость чертежей									
Номер листа		Наименование							
1		Ведомость чертежей							
2		Обмерный план М1:50							
3		План монтажа перегородок							
4		План расстановки мебели							
5		План заполнения дверных проемов							
6		План расположения сантехнического оборудования							
7		План теплого пола							
8		План напольных покрытий							
9		План потолка							
10		План расположения осветительных приборов							
11		План расположения электрооборудования							
12		План расположения электропроводов							
13		Схема привязки групп светильников к выключателям							
14		План-схема отделки стен и маркировки разветок							
15		Ведомость отделки стен по помещениям							
16		Развертки 1...6. Прихожая. Кухня-гостиная							
17		Развертки 7...12. Детская, Спальня							
18		Развертки13...20. Санузел, Ванная комната							
19		Развертки 17...20. Ванная комната							
Примечание: -на чертежах все привязки указаны в мм от УЧП, если не указано иное; -за отметку 0.000 принят уровень чистого пола -привязки по электрооборудованию (розетки, светильники и т.д.) указаны до оси прибора (рамки), если не указано иное; -дизайн-проект разработан с учетом черновых обмеров, после проведения отделочных работ, при необходимости дополнительно согласовать размеры; -3D-визуализации могут частично отличаться от рабочей документации и даны для понимания общей концепции. Дизайн-проект реализуется по рабочей документации.									
					Ведомость чертежей				
Изм.	Лист	№ докум.	Подп.	Дата					
Разраб.									
Пров.									
Н.контр.									
Утв.									
Копировал					Формат А3				

Экспликация помещений

Номер помеще-ния	Наименование	Площадь, м²
1	Жилая комната №1	12,82
2	Жилая комната №2	16,24
3	Кухня	9,73
4	Ванная комната	3,75
5	Прихожая/коридор	8,90
6	Лоджия	3,23
		54,67


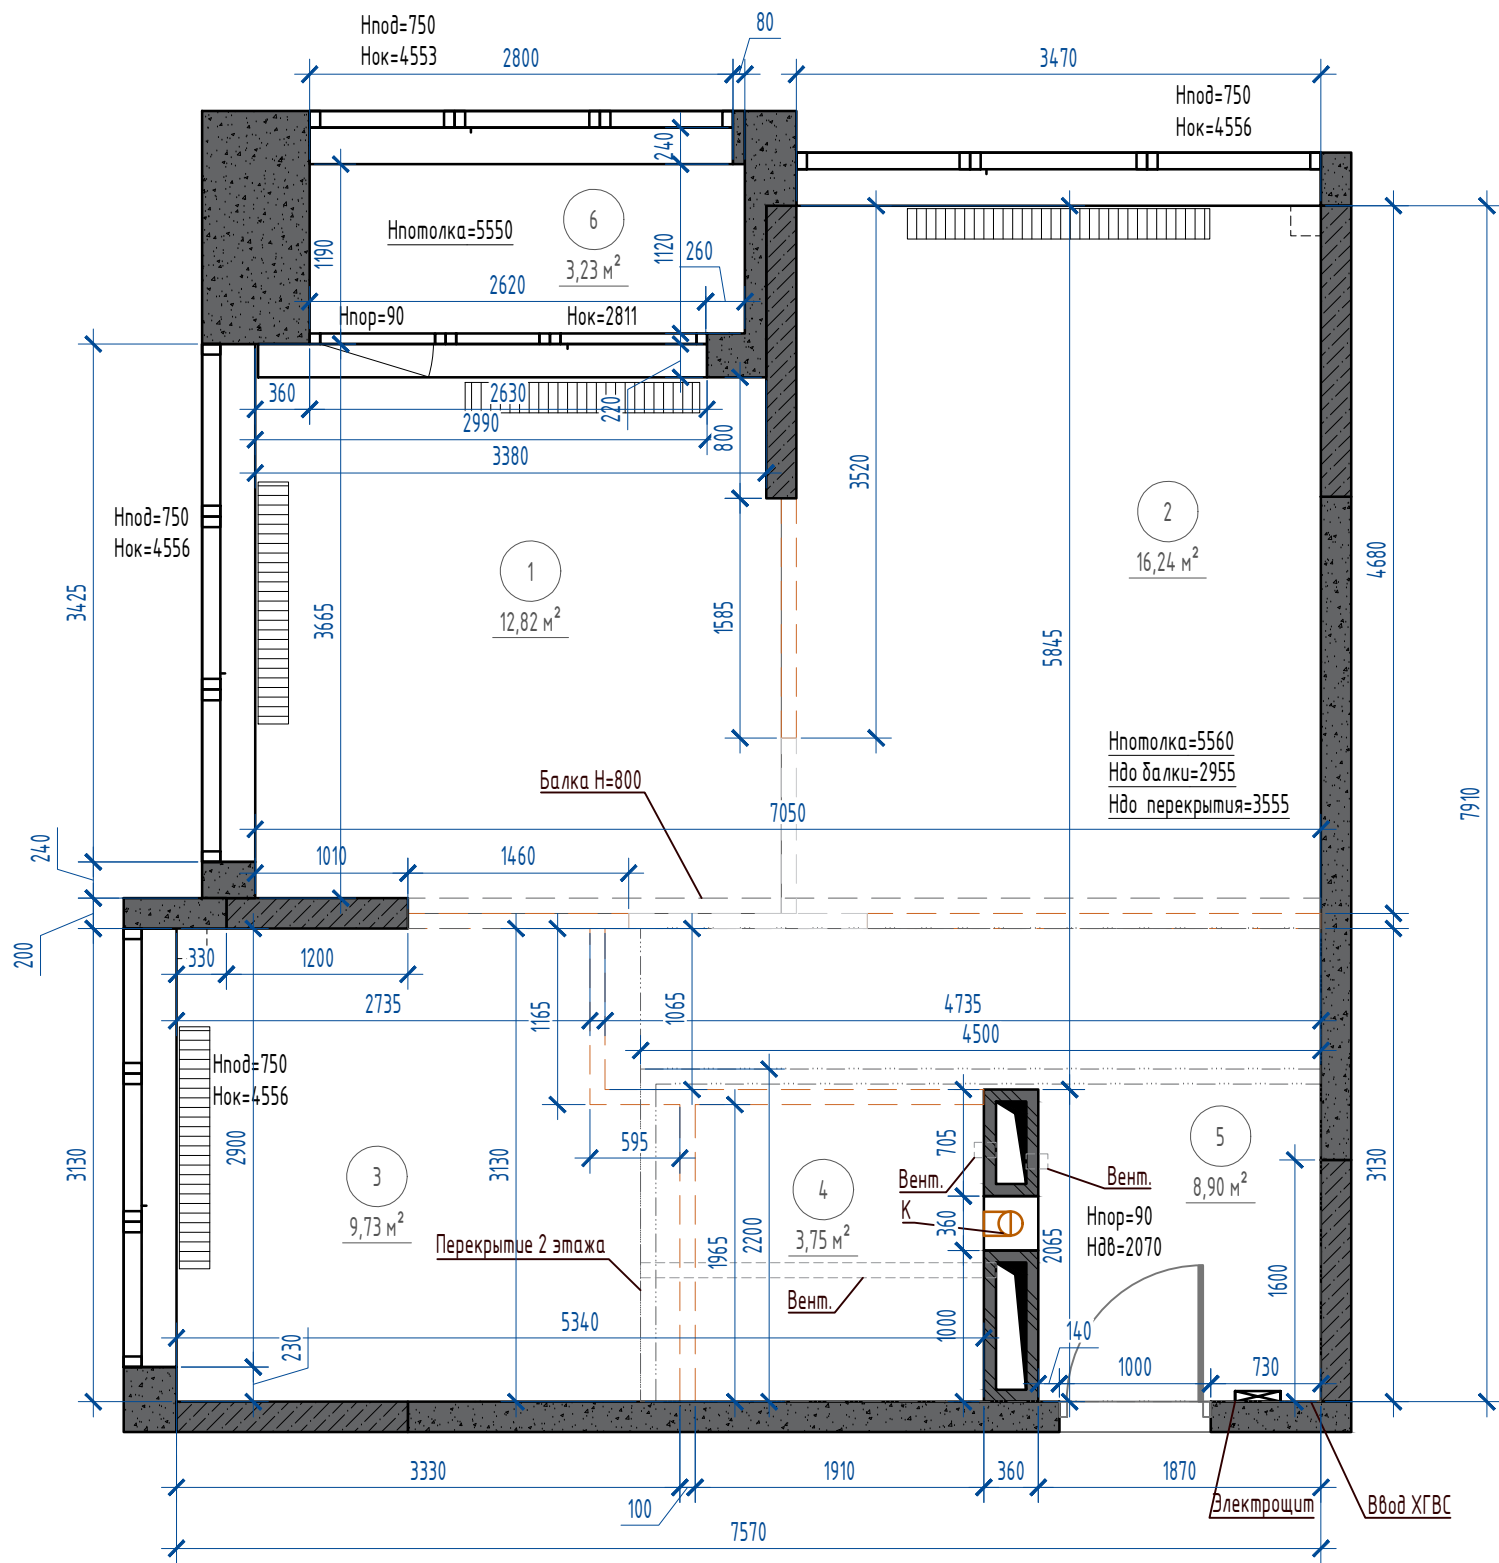


Условные обозначения:

- контур наружных стен
- контур ж/б конструкций
- контур внутренних перегородок
- контур перегородок в 1 блок

- Примечание:
- Высота потолка указана от уровня черного пола до уровня перекрытия.
 - Толщины внешних стен показаны условно.
 - Все возникающие вопросы и расхождения размеров решаются в процессе строительных работ.

Изм.	Кол.уч.	Лист	№ док.	Подп.	Дата	Обмерный план M1:50	Лист
							2

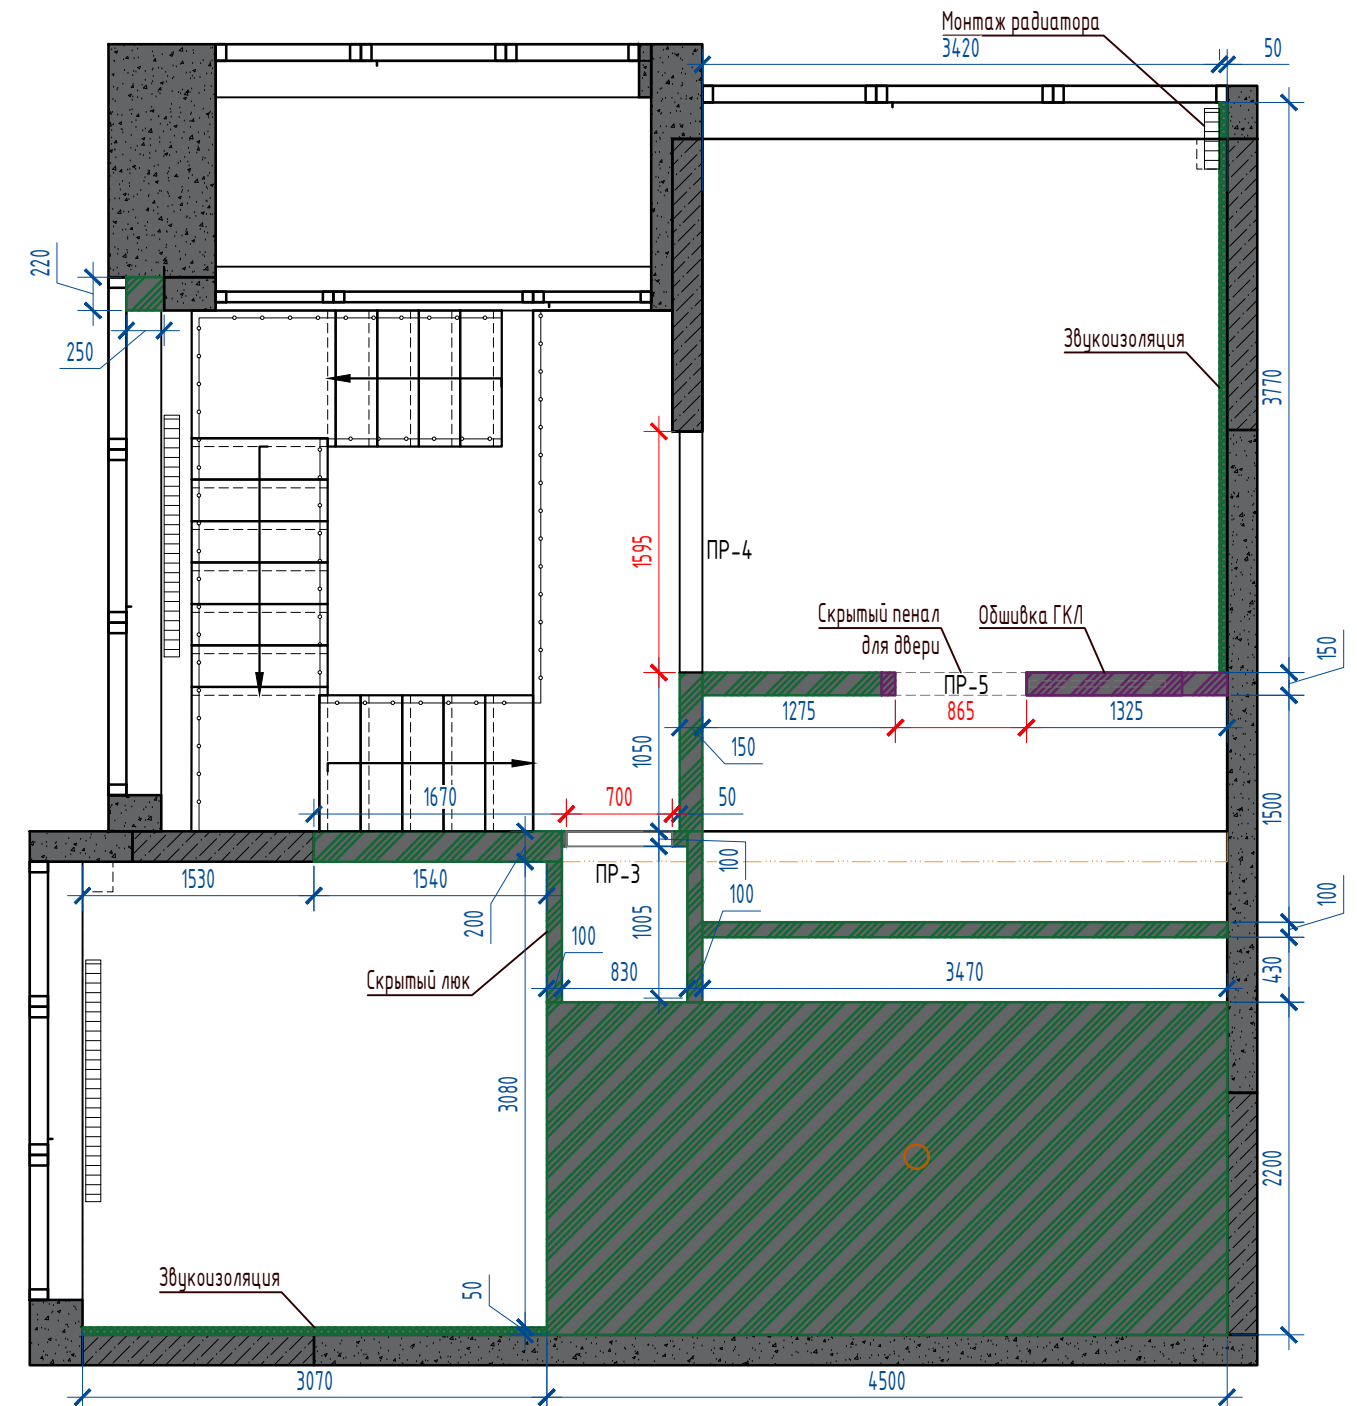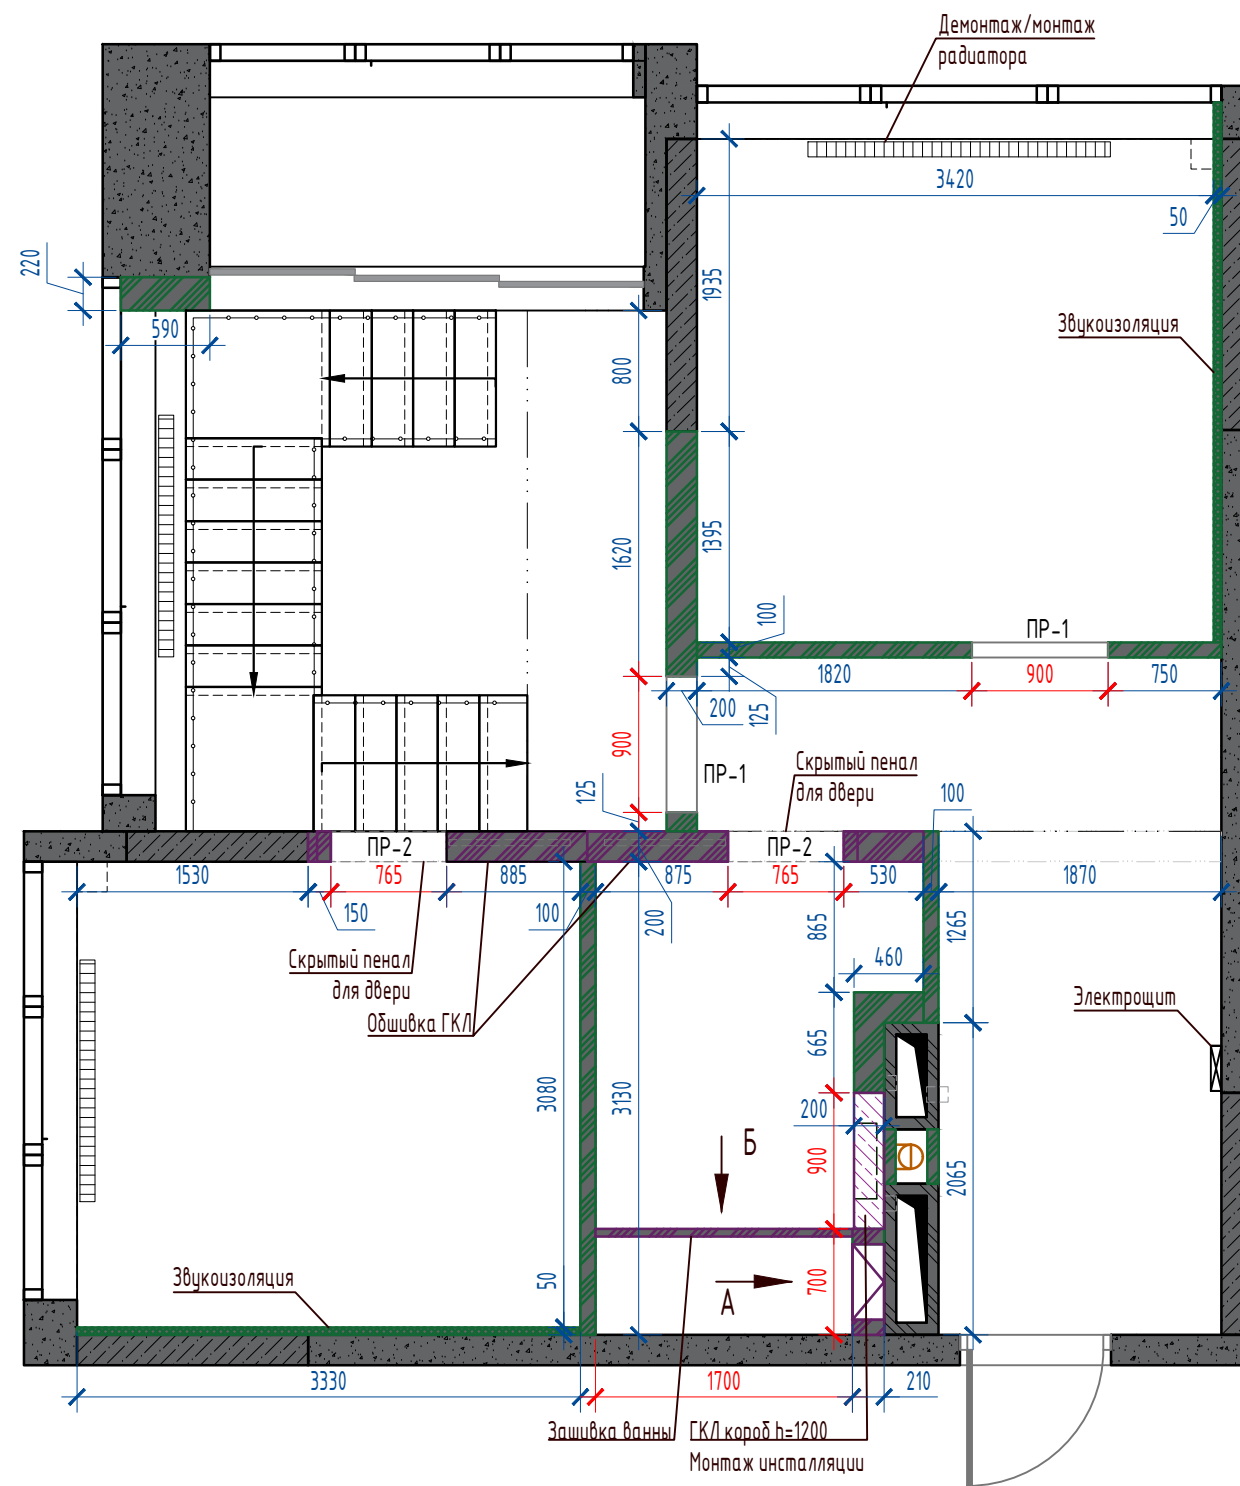

Ведомость проемов


Марка, позиц.	Размеры проема	Кол-во
ПР-1	900x2370 (h)	2
ПР-2	765x2400 (h)	2
ПР-3	700x1670 (h)	1
ПР-4	1595x2130 (h)	1
ПР-5	865x2050 (h)	1

Условные обозначения:

- контур наружных стен
- контур ж/б конструкций
- монтируемые перегородки
- монтируемая перегородка из ГКЛ/В
- 800 - выдержать размер с учетом чистовой отделки

Примечание:

- Все высоты указаны от уровня чистого пола.
- За отметка 0.000 принята отметка чистого пола со стяжкой.
- Все стены выровнять, монтажные углы вывести строго под 90 градусов.
- Размеры проемов согласовать с поставщиком дверей.
- Модель и размеры радиатора уточнить в соответствии с технической документацией.
- В санузлах выполнить гидроизоляцию пола.
- Необходимость монтажа закладных деталей уточнять на месте и в соответствии с визуализациями.

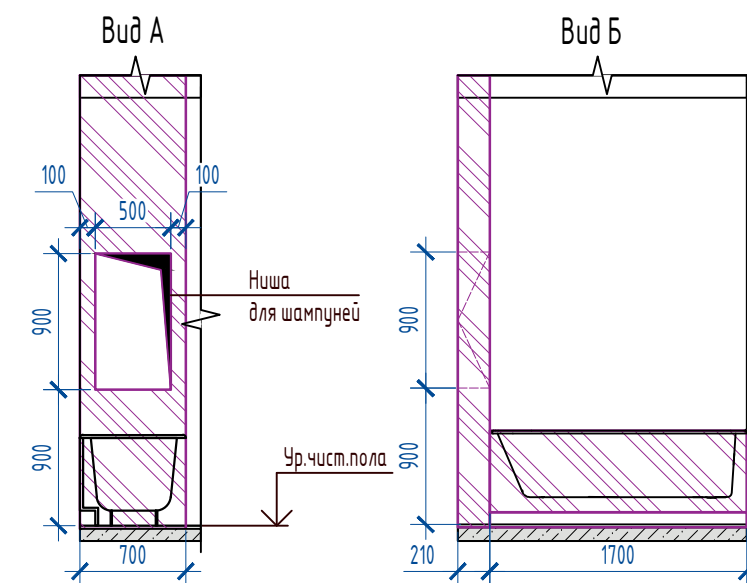


Изм.	Кол.уч.	Лист	№ док.	Подп.	Дата	Лист
						3

План монтажа перегородок


Копировал

Формат А3

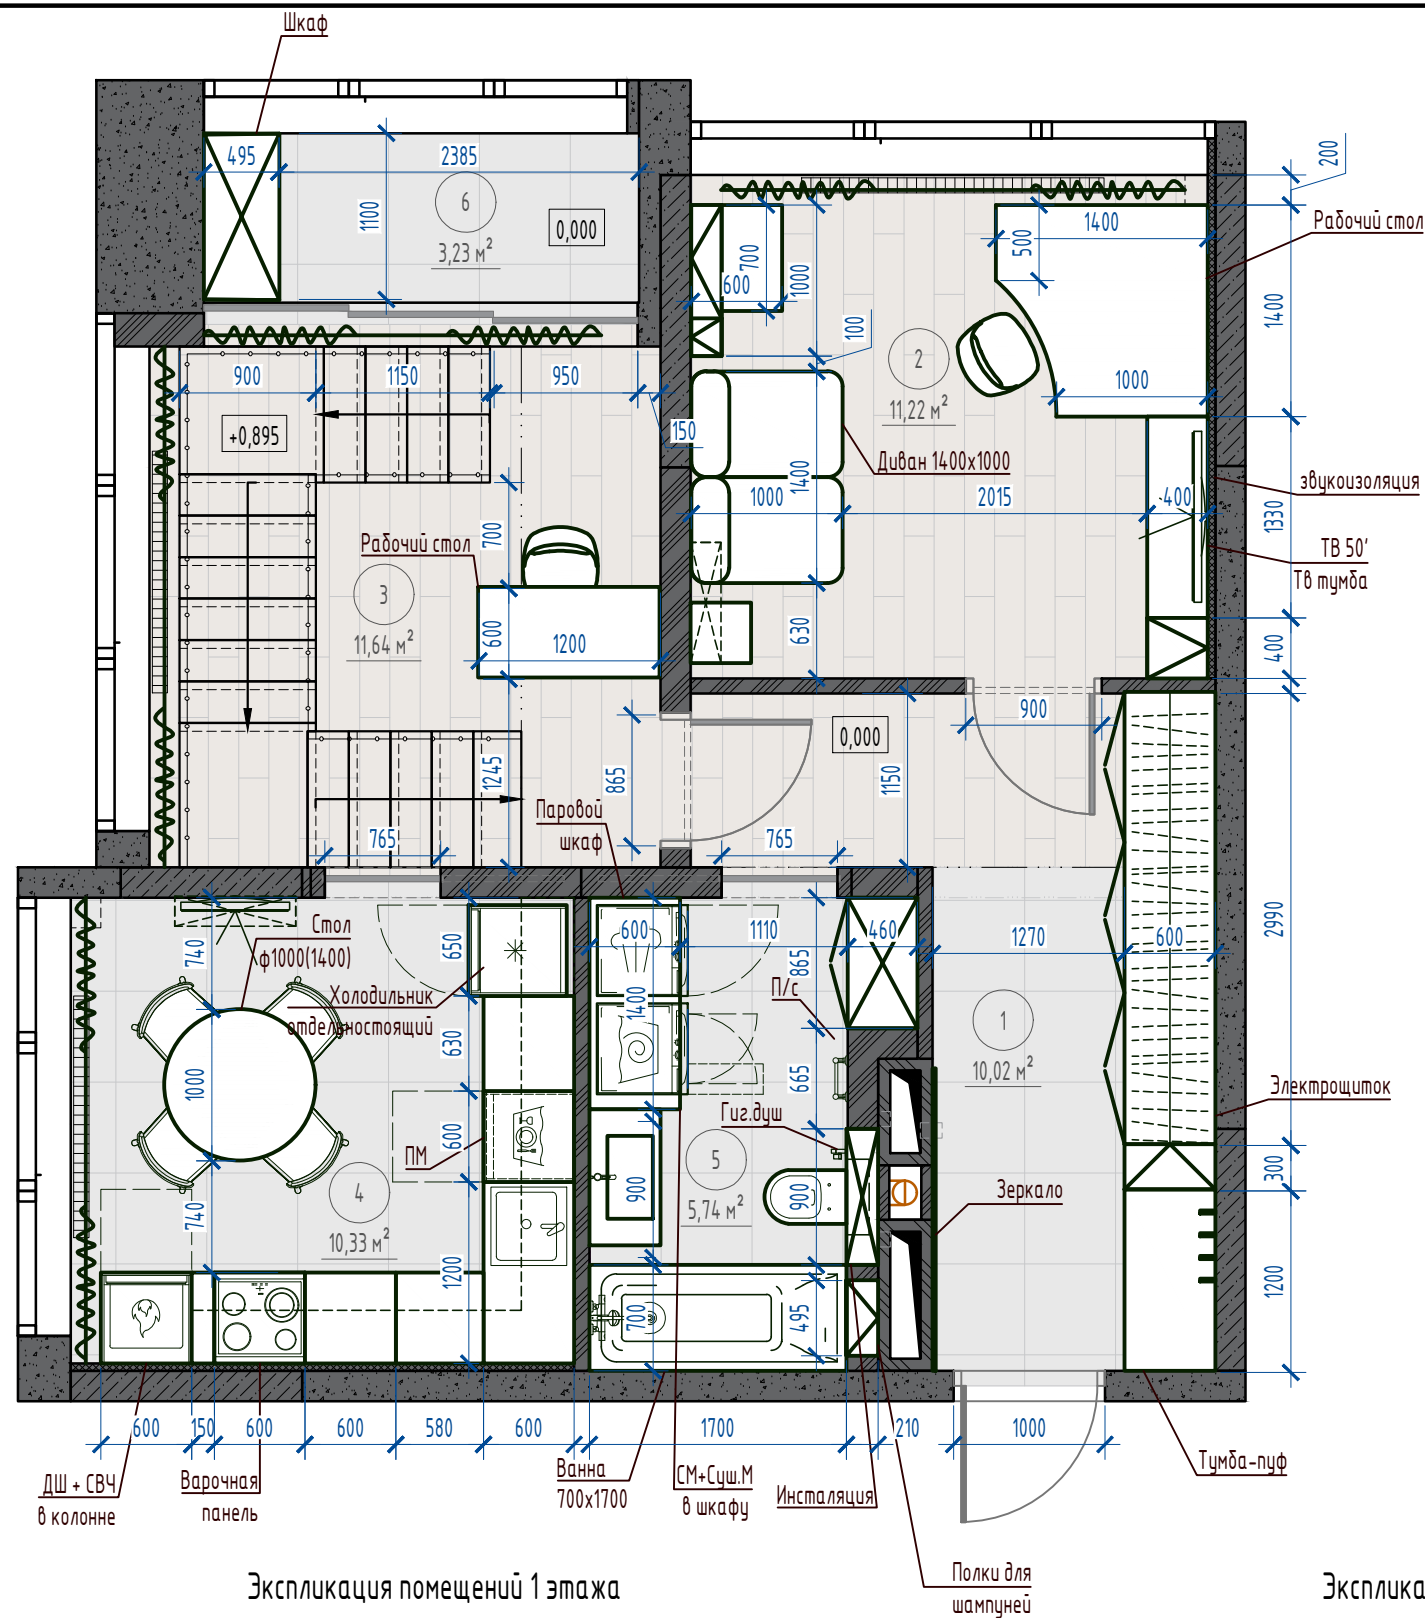

Экспликация помещений 1 этажа

Номер помеще-ния	Наименование	Площадь, м²
1	Прихожая	10,02
2	Гостиная	11,22
3	Холл	11,64
4	Кухня	10,33
5	Ванная комната	5,74
6	Лоджия	3,23
		52,18

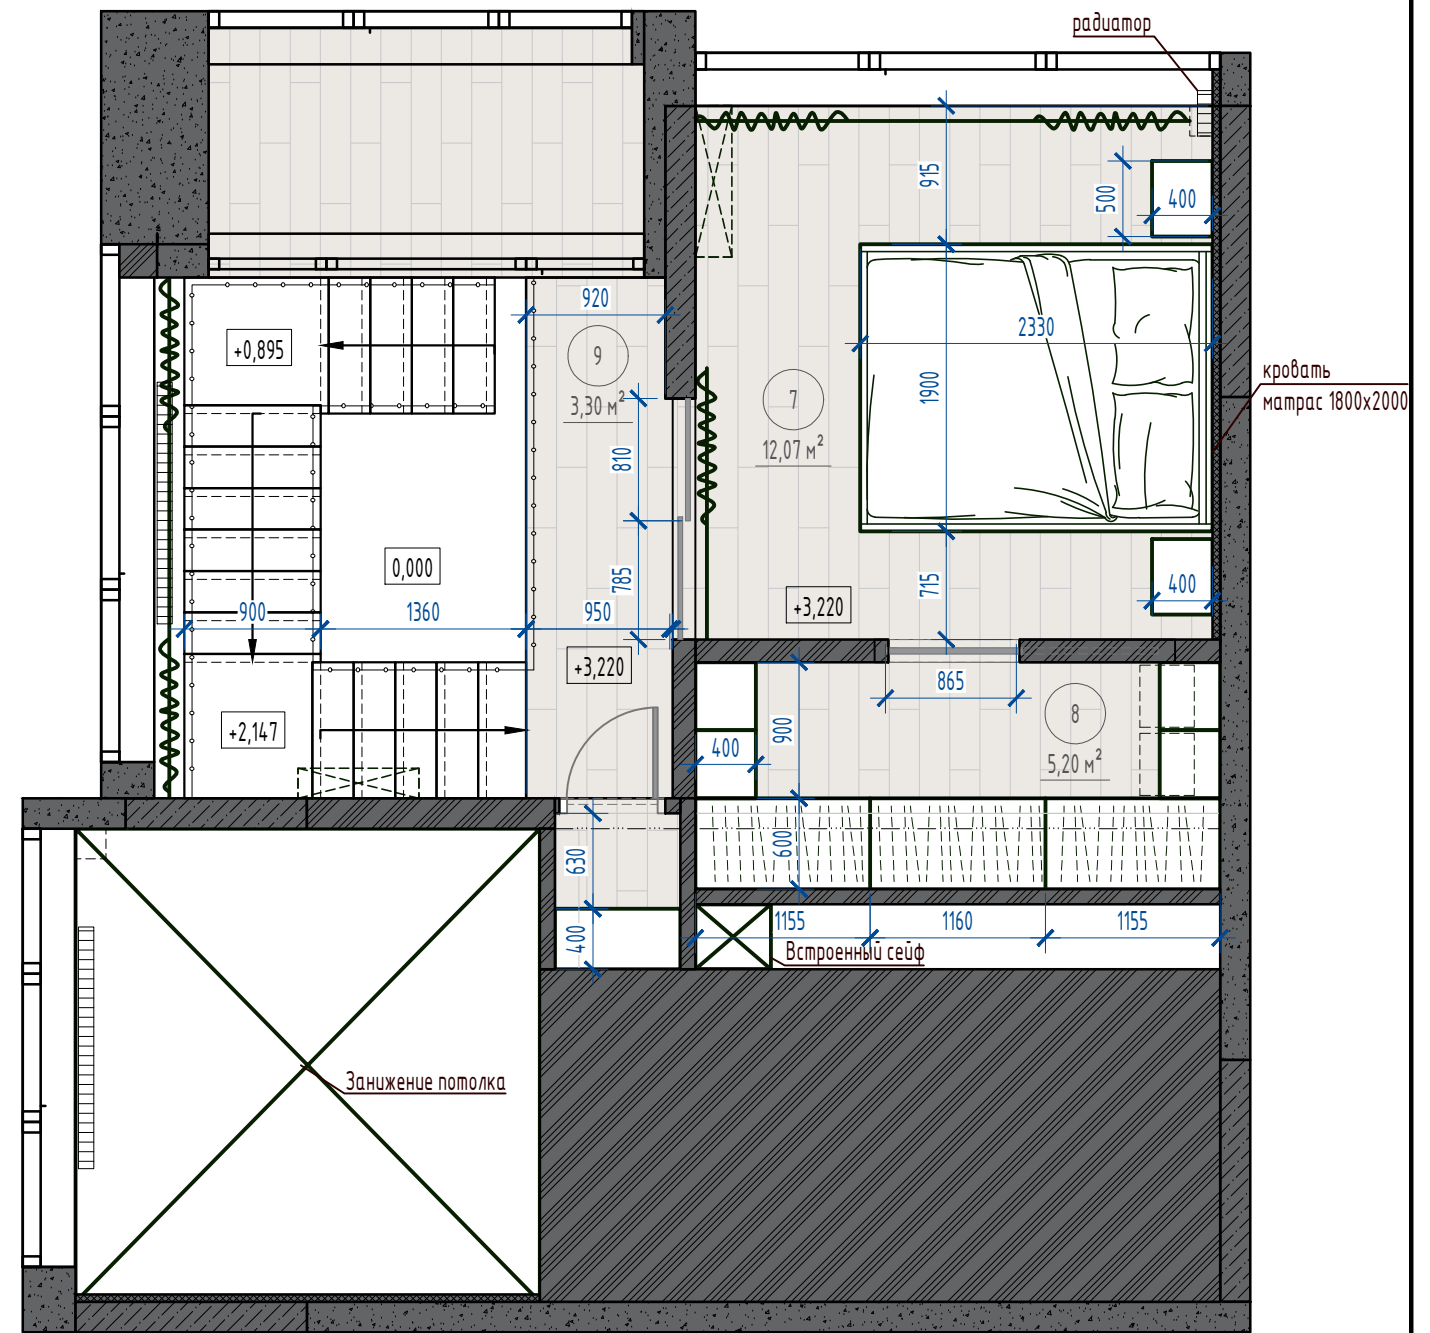

Экспликация помещений 2 этажа

Номер помеще-ния	Наименование	Площадь, м²
7	Спальня	12,07
8	Гардероб	5,20
9	Коридор	3,30
		20,57

Условные обозначения:

- контур наружных стен
- контур ж/б конструкций
- контур внутренних перегородок



Изм.	Кол.уч.	Лист	№ док.	Подп.	Дата

План расстановки мебели

Лист
4

Копировал

Формат А3

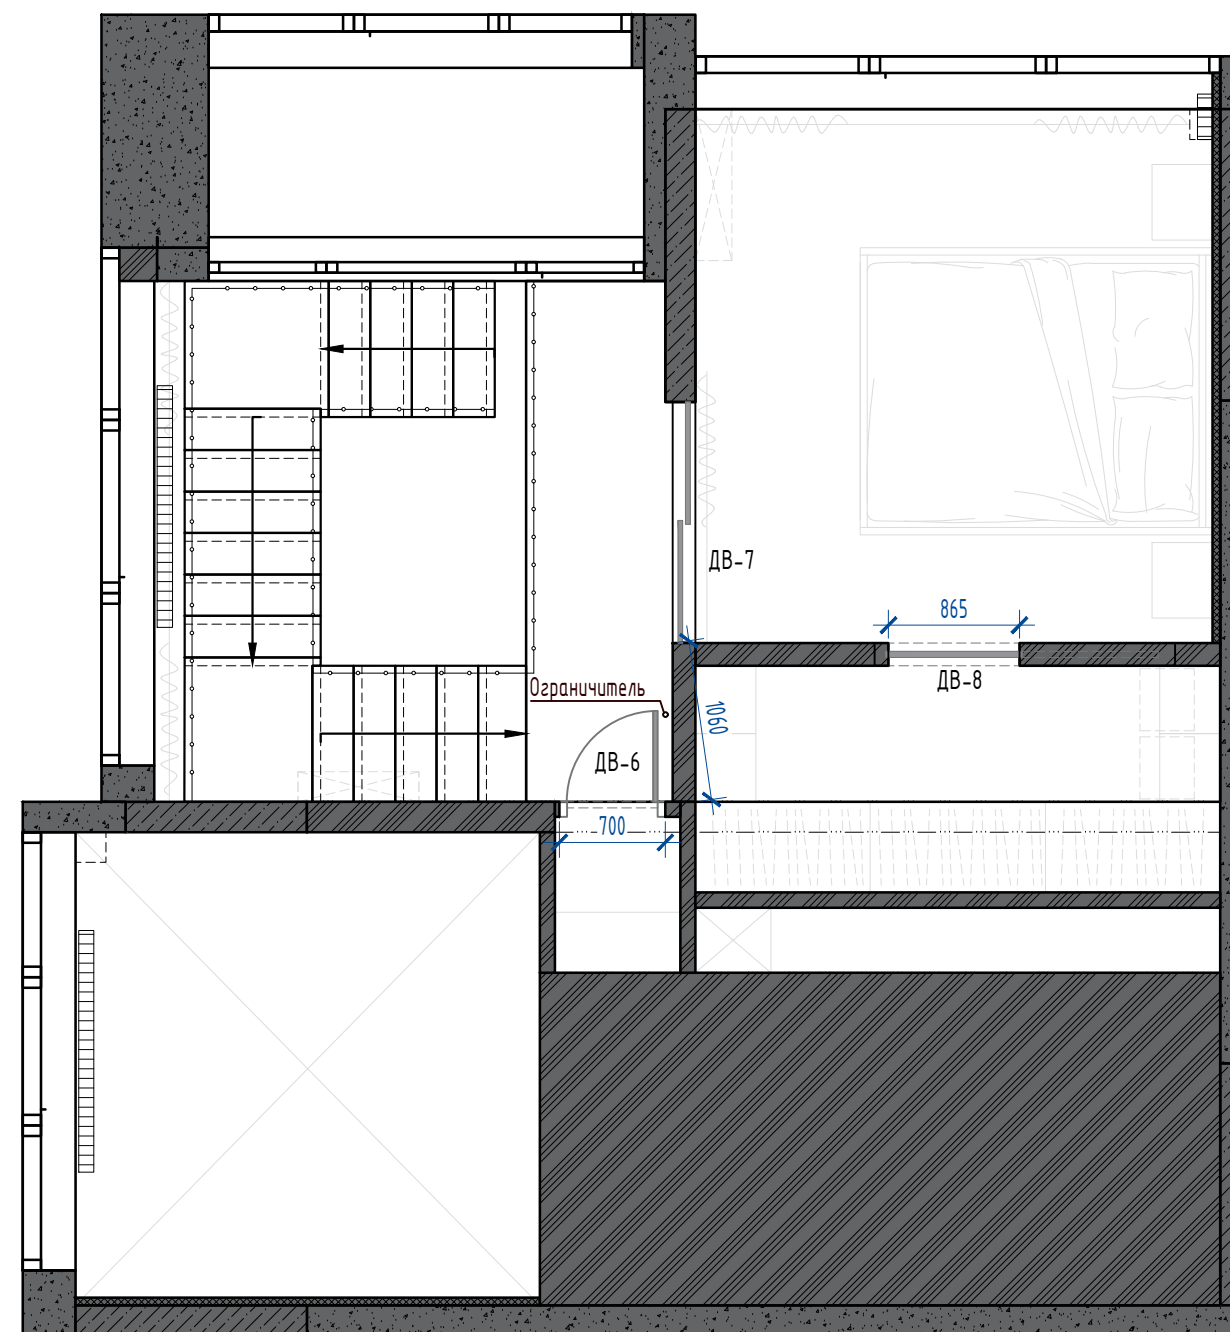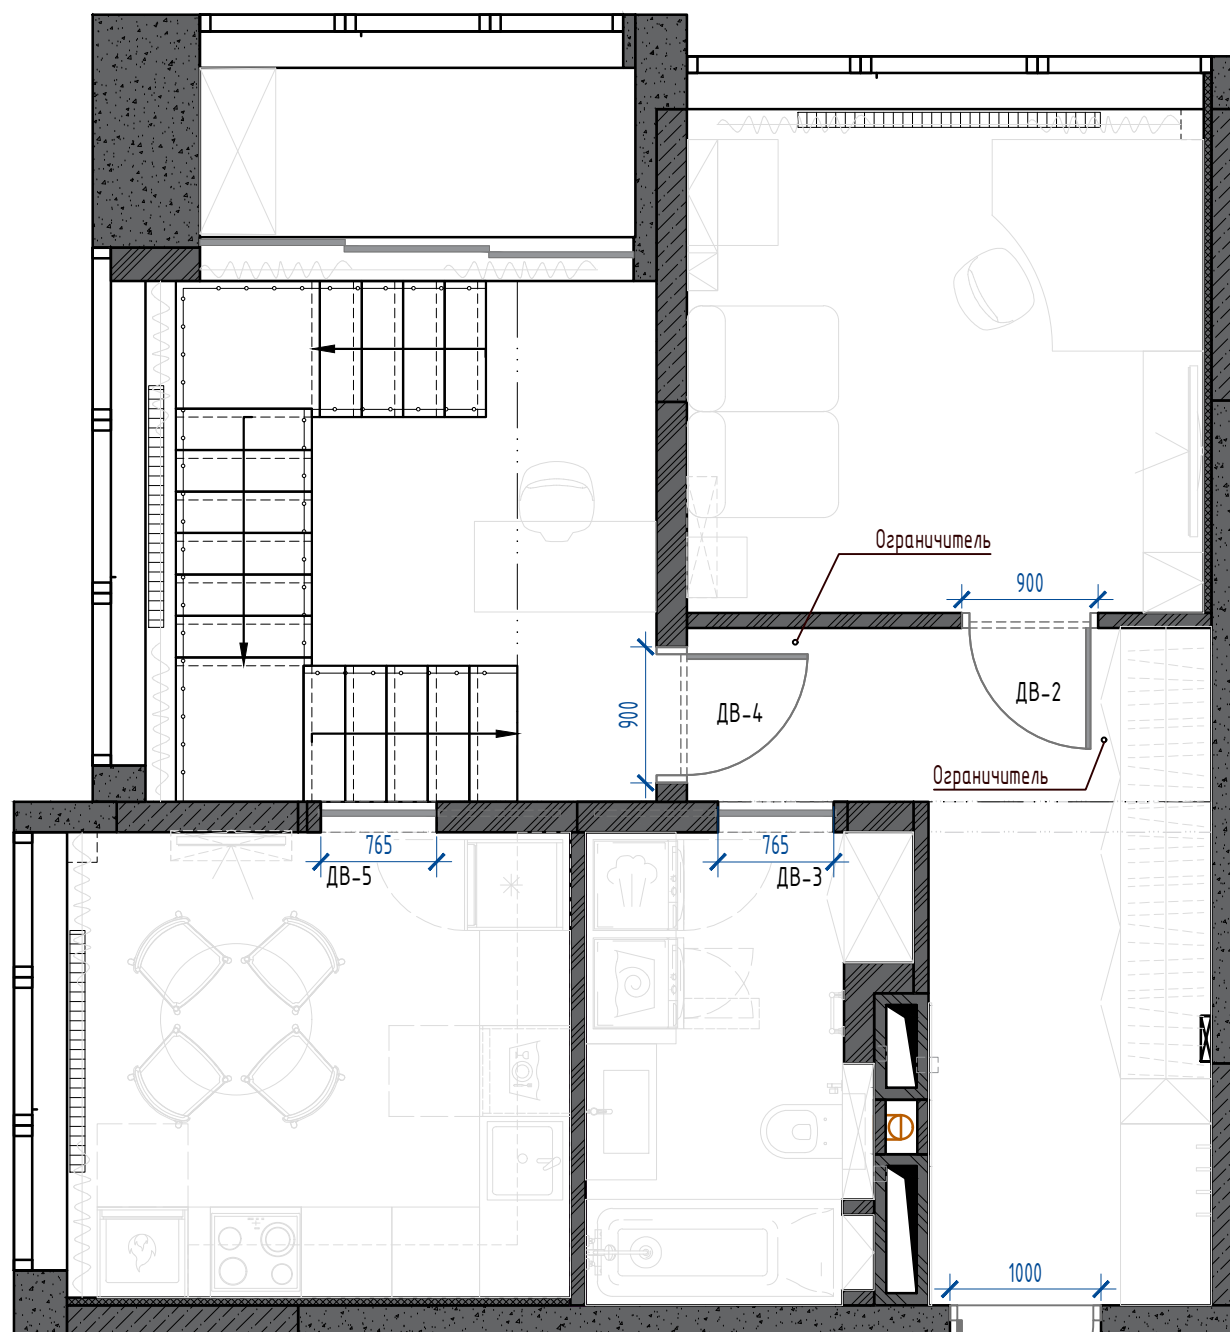

Спецификация заполнения дверных проемов

Обозначение	Наименование	Размеры проема (LxH)	Размеры полотна (LxH)	Открытие	Завертки	Кол-во
ДВ-1	Входная дверь - внутренняя панель белого цвета	1000x2070		левое	-	1
ДВ-2	Дверь на скрытом коробе под покраску	900x2370	800x2300	правое прямое	-	1
ДВ-3	Раздвижная дверь в скрытый пенал	765x2370	800x2300	правое	+	1
ДВ-4	Дверь на скрытом коробе под покраску	900x2370	800x2300	правое прямое	-	1
ДВ-5	Раздвижная дверь в скрытый пенал	765x2370	800x2300	левое	-	1
ДВ-6	Дверь на скрытом коробе под покраску	700x1670	600x1600	левое прямое	-	1

ДВ-7	Раздвижная дверь	1595x2130		левое	-	1
ДВ-8	Раздвижная дверь в скрытый пенал	865x2050	900x2000	левое	-	1
	Завертки - черные					1
	Дверные ручки - черный					7
	Ограничитель открывания дверей (скрытый) - черный					4

Примечание:

1. Все распашные двери оборудовать напольным фиксатором. Определить на месте его расположение и осуществить монтаж.
2. Для дверей в санузел предусмотреть завертки.

Изм.	Кол.уч.	Лист	№ док.	Подп.	Дата


План заполнения дверных проемов

Лист


5

Копировал

Формат А3

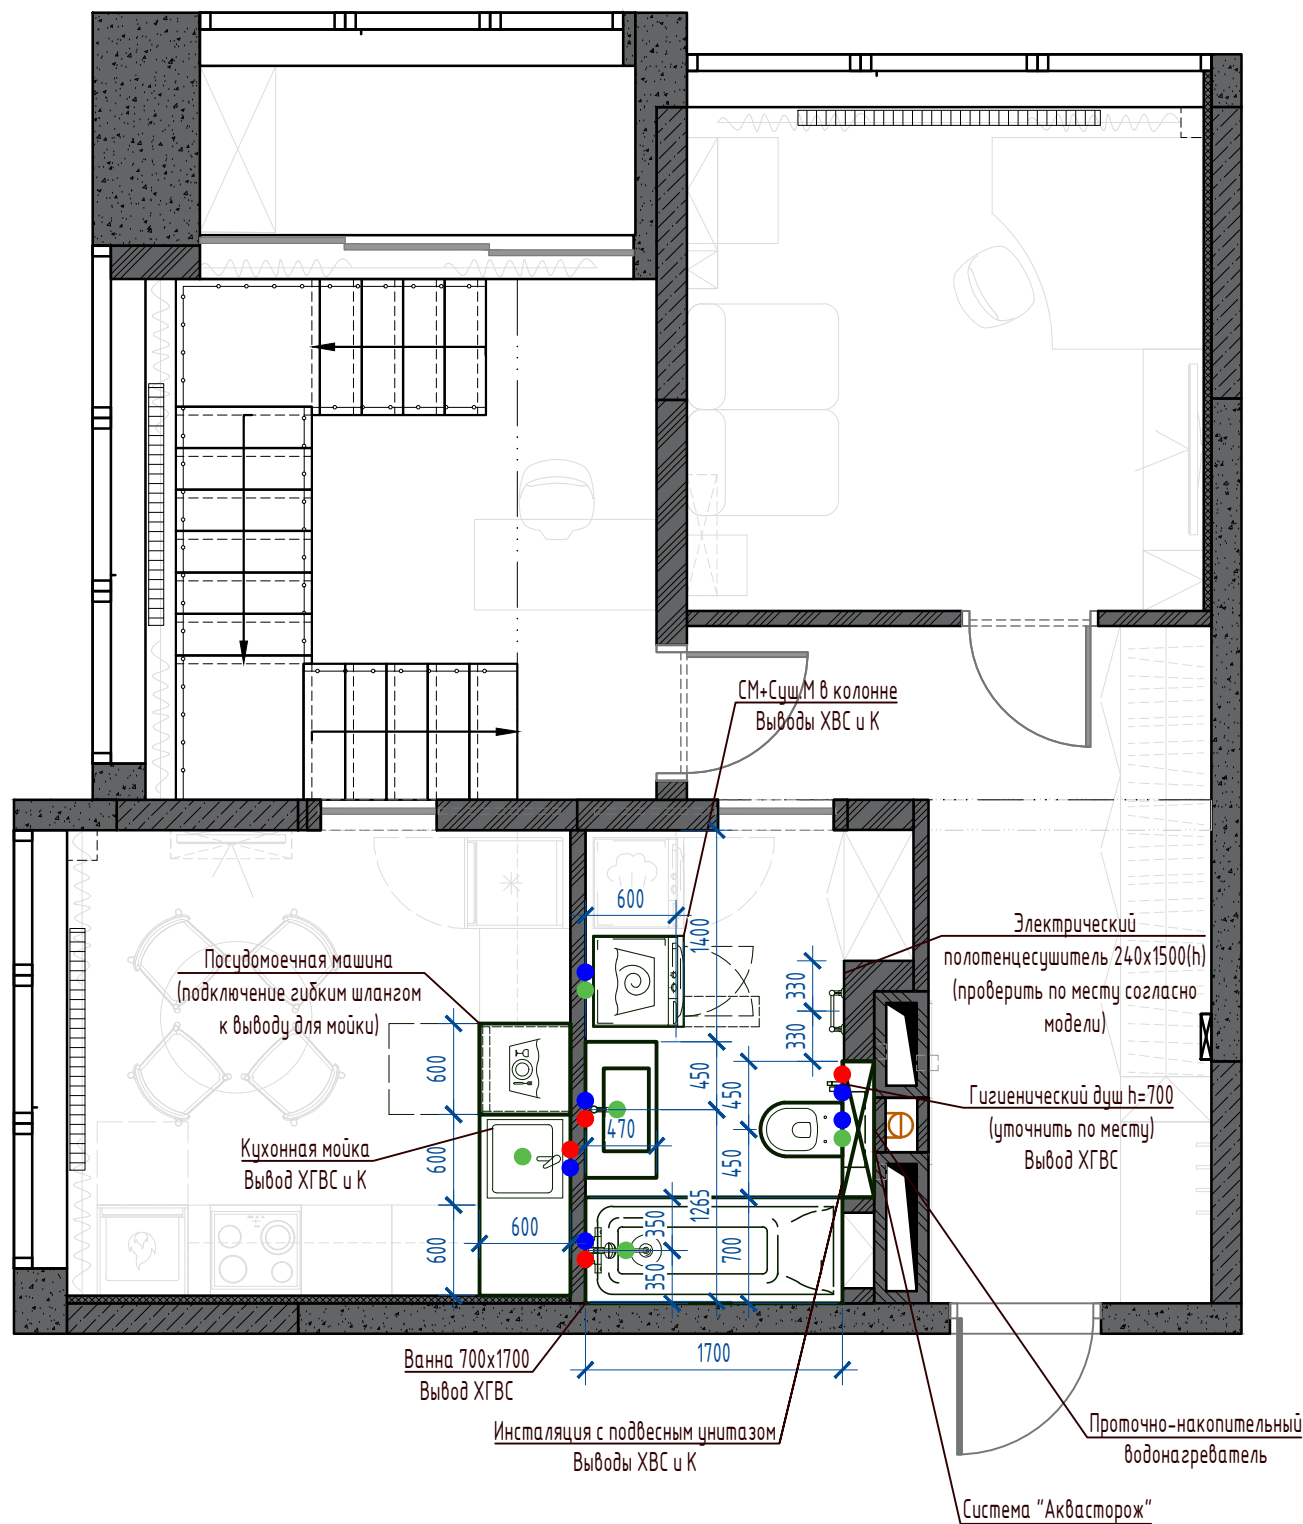

Ориентировочные привязки выводов ХГВС и канализации для сан.тех. приборов

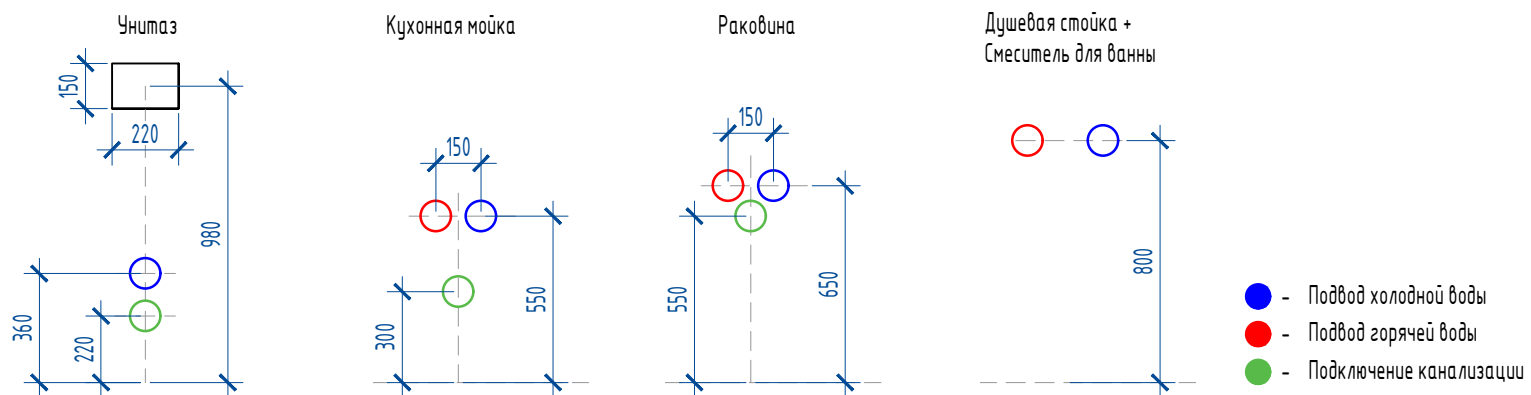



Примечание:

1. Все размеры уточнить по месту.
2. Даны оптимальные размеры сантехники. Уточнить выходы после подбора оборудования.
3. Подводы воды и канализации для сантехнического оборудования производить согласно техническим рекомендациям на данное оборудование.
4. Выводы ГВС, ХВС и канализацию расположить по центру сантехнического оборудования
5. Расположение и количество датчиков протечек воды согласовать с сантехником.
6. Предусмотреть ревизионные люки-невидимки для доступа к сантехнической разводке и счетчикам в местах их выхода.
7. Люки инженерных коммуникаций выполнить в скрытом виде.
8. См. совместно с развертками.

Изм.	Кол.уч.	Лист	№ док.	Подп.	Дата	План расположения сантехнического оборудования	Лист
							6

Копировал

Формат А3

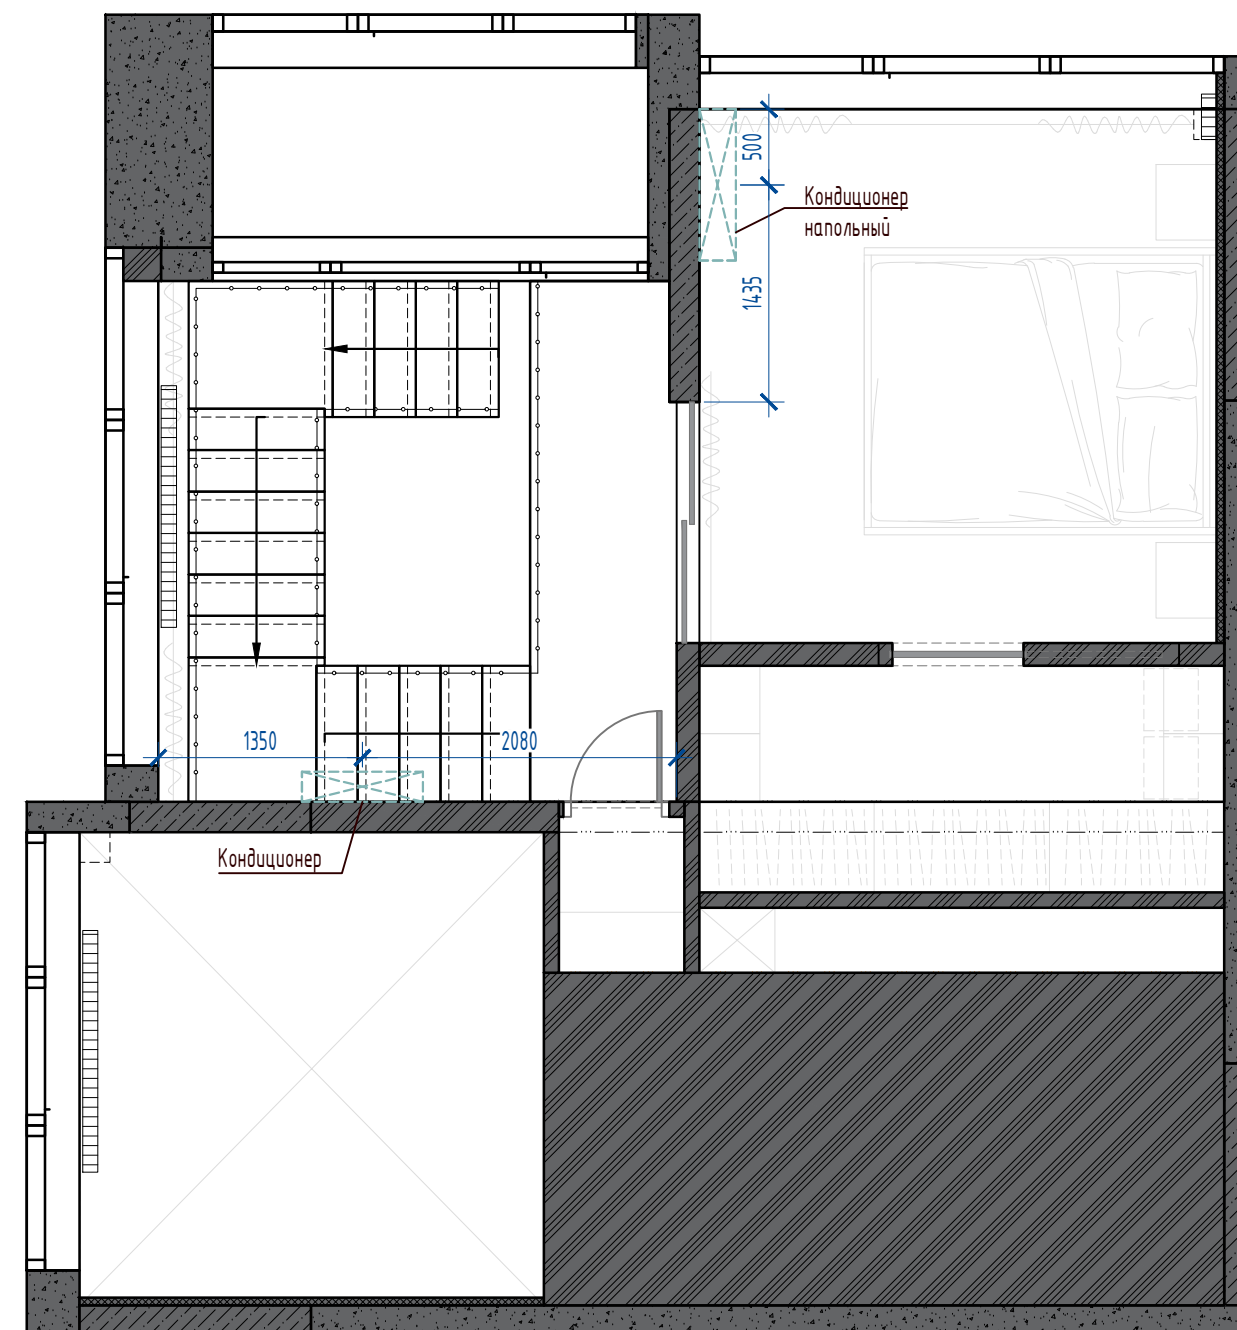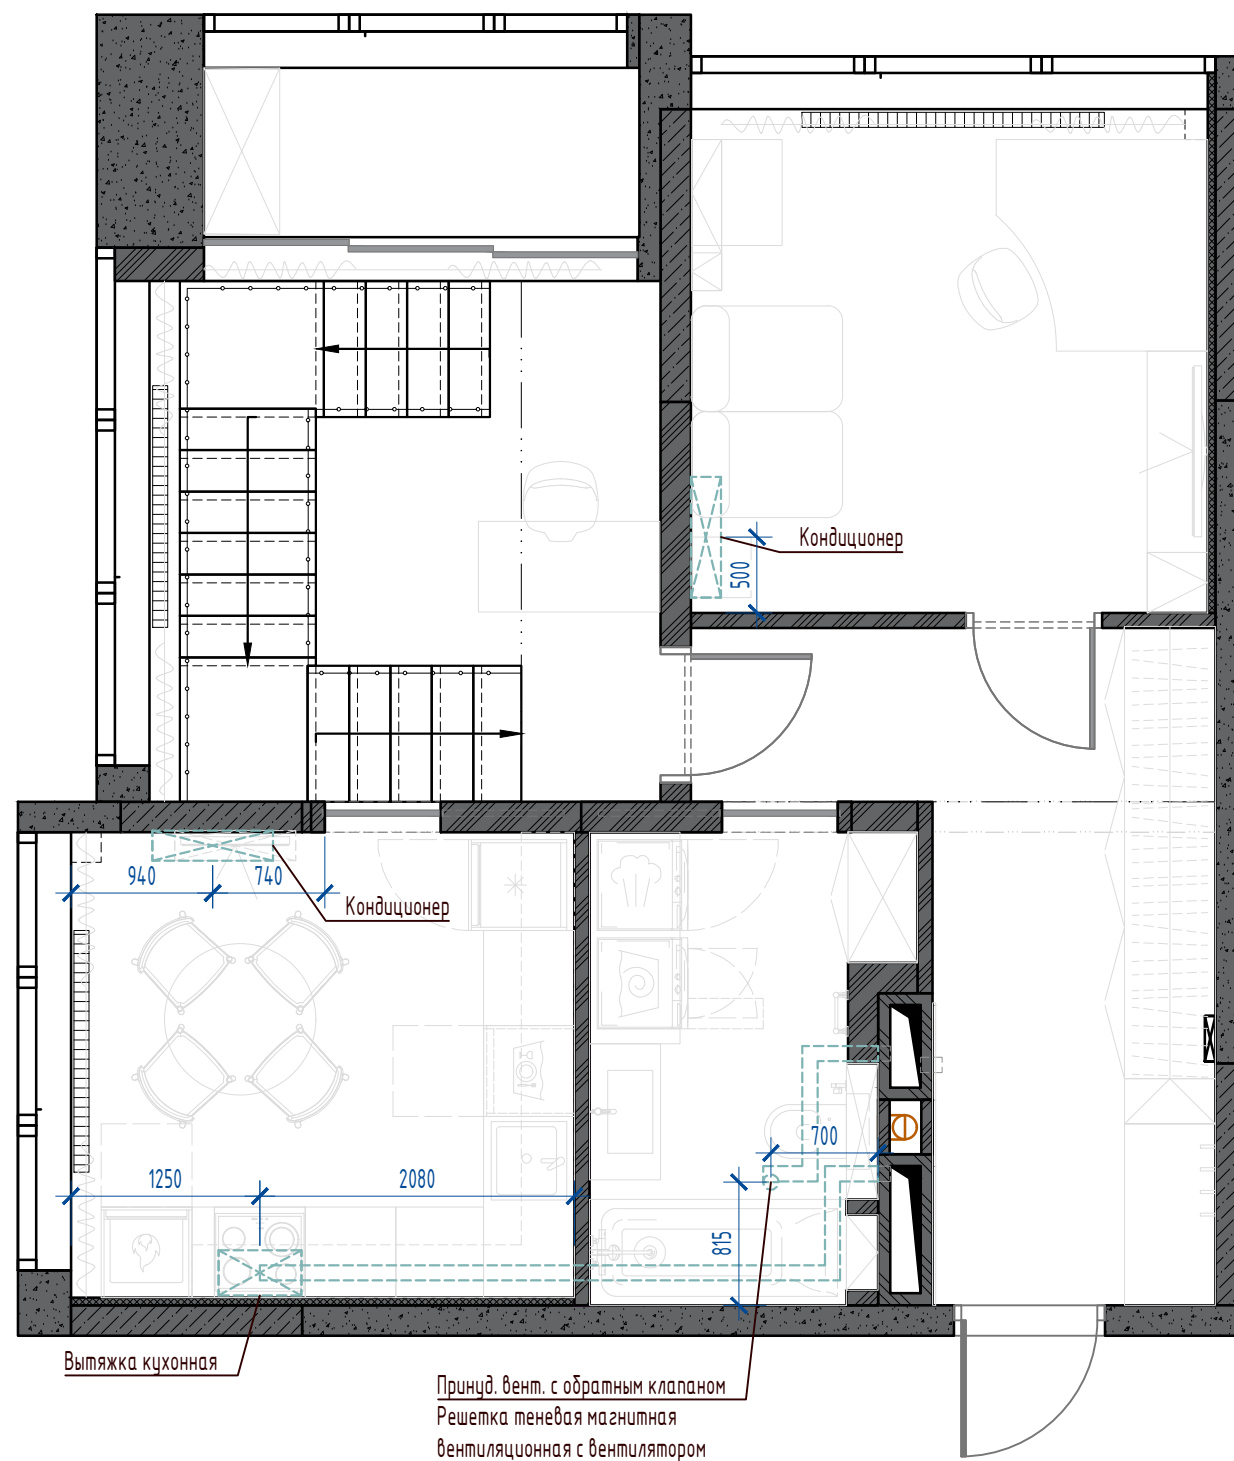



Примечание:

1. Высоту установки кондиционеров и размещение наружных блоков согласовать с монтажниками. Кондиционеры подобрать под каждое помещение отдельно.
2. Все размеры уточнить по факту после черновых отделочных работ.
3. Расположение и высоту эл. выводов уточнить после выбора кондиционера и консультации специалистов.
4. Расположение выводов, а также нюансы монтажа и отвода конденсата кондиционеров уточнить у специалистов ДО прокладки электрических кабелей и монтажа потолков
5. Прокладку вентиляции и расположение вент.решеток согласовать с специалистом.
6. Расположение эл. вывода для вентиляции согласовать по месту с производителем работ.

						План кондиционеров и вентиляции	Лист
							7
Изм.	Кол.уч.	Лист	№ док.	Подп.	Дата		

Копировал

Формат А3

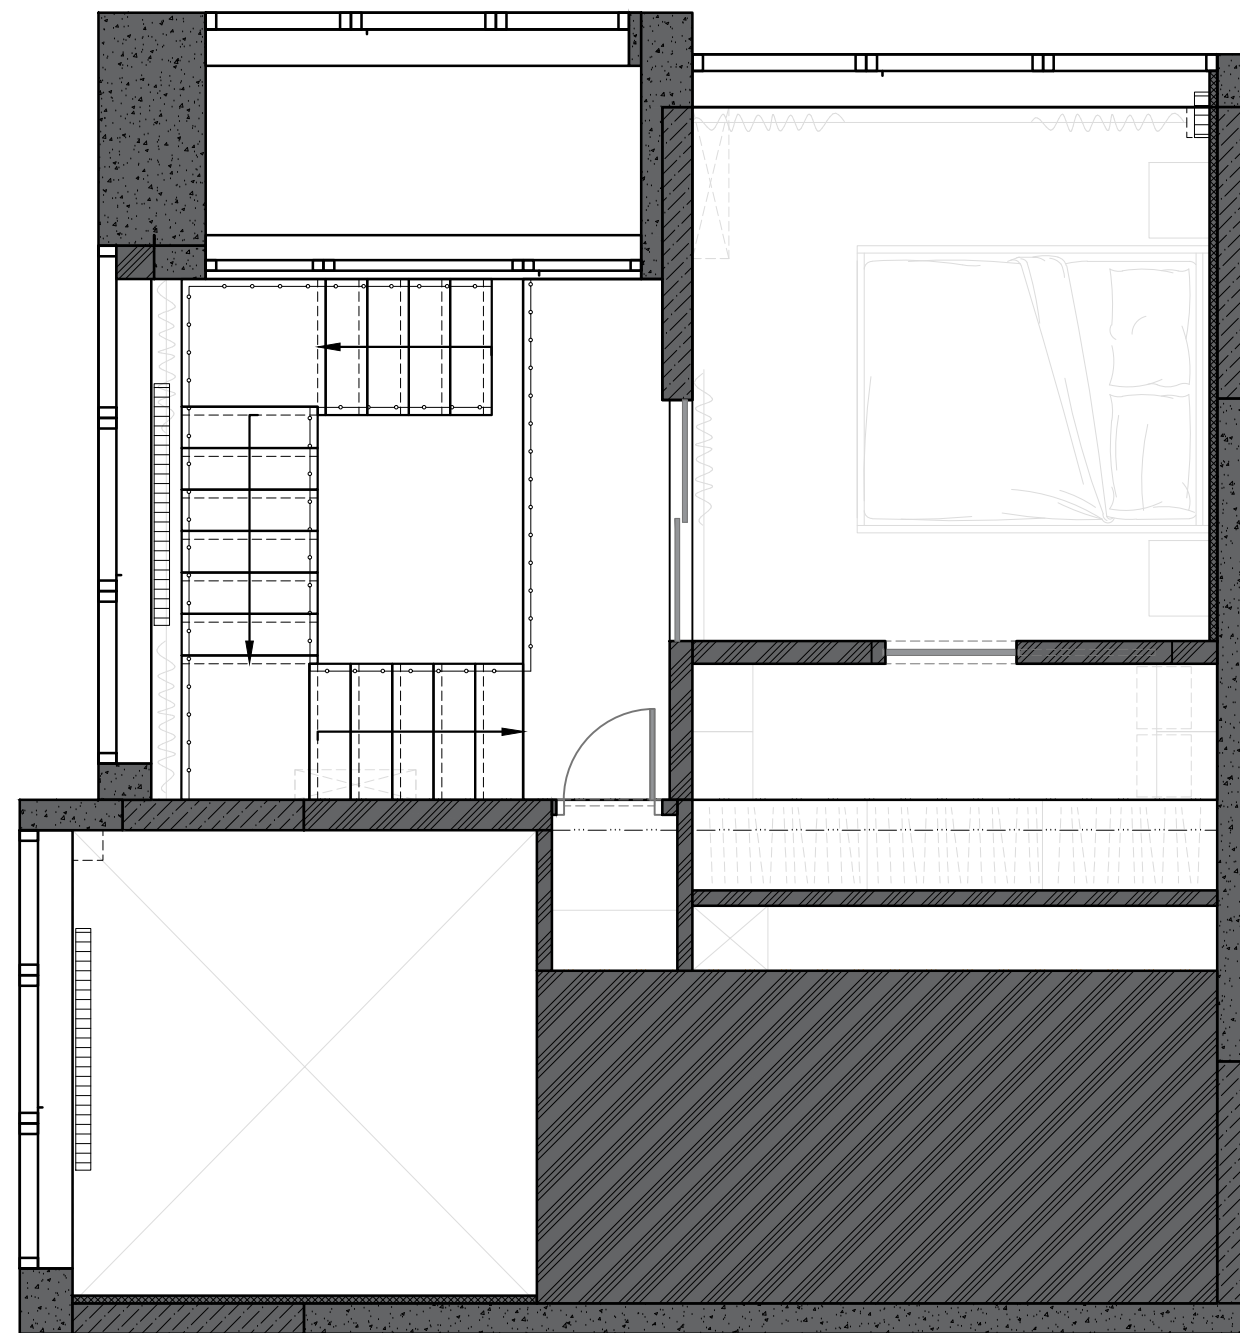
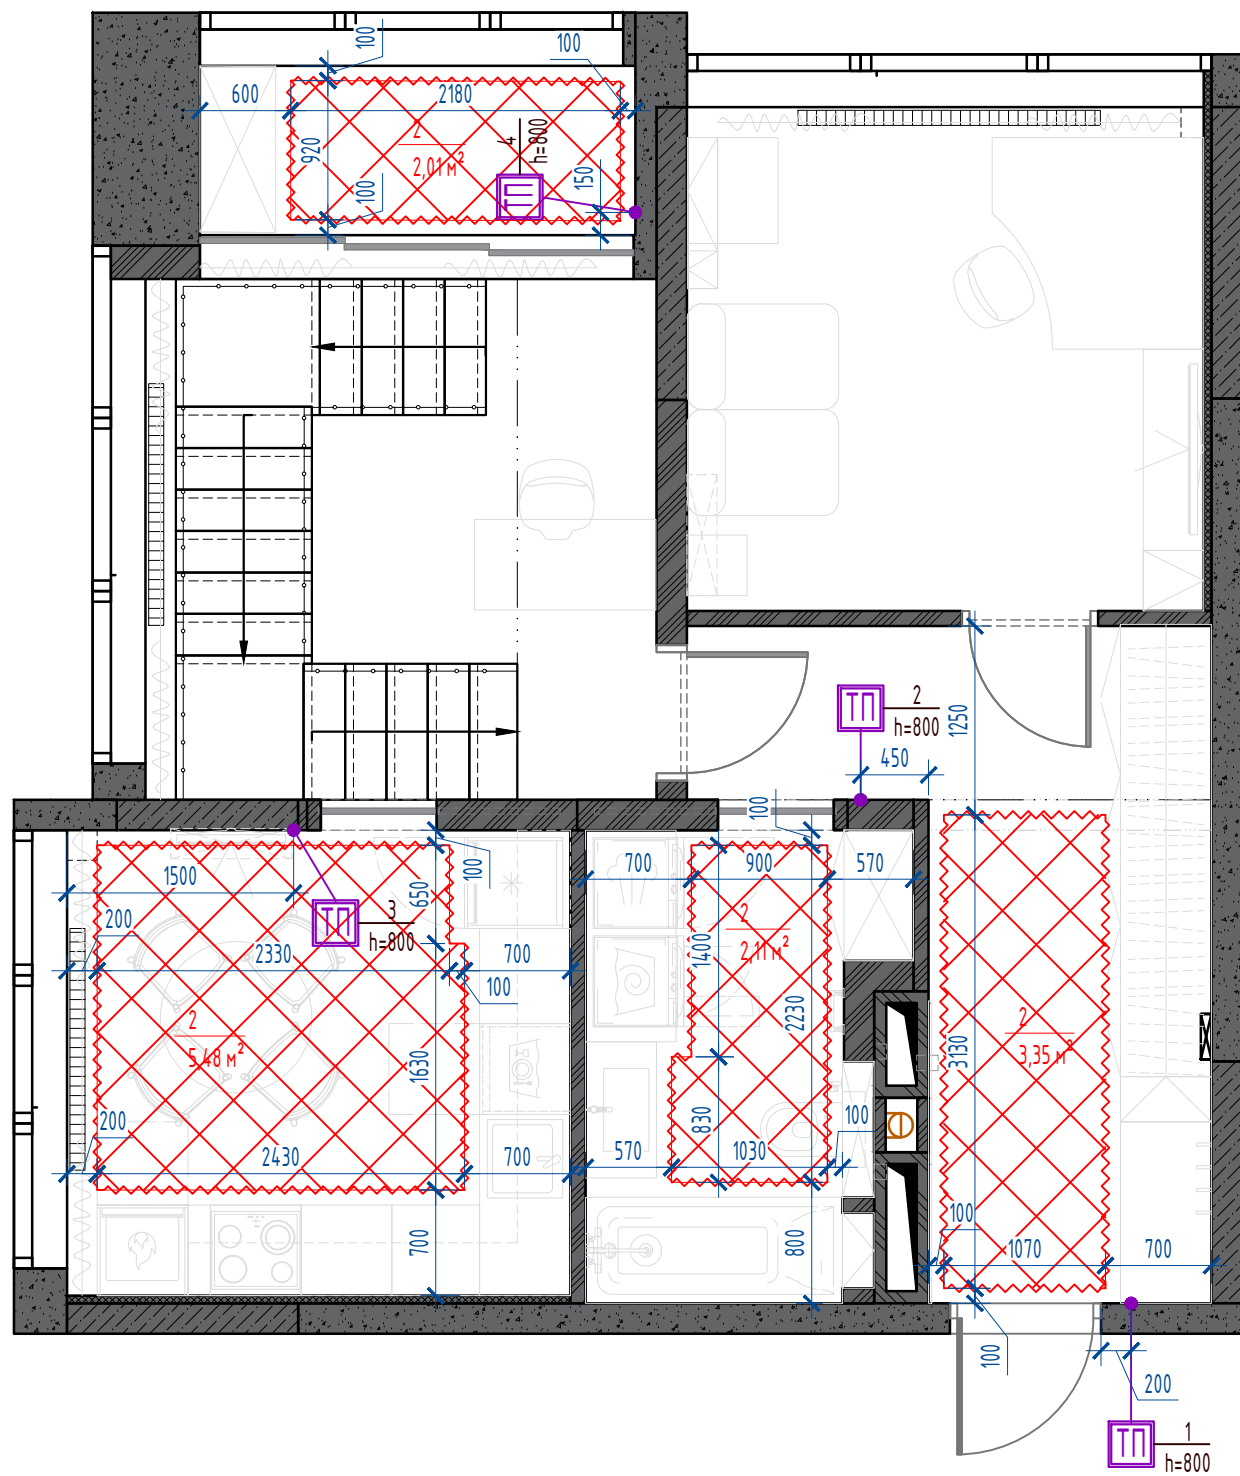


Условное обозначение	Наименование	Кол-во (м², м.п.)
	Теплый пол электрический	12.9

Изм.	Кол.уч.	Лист	№ док.	Подп.	Дата	План теплого пола	Лист
							8



Копировал

Формат А3

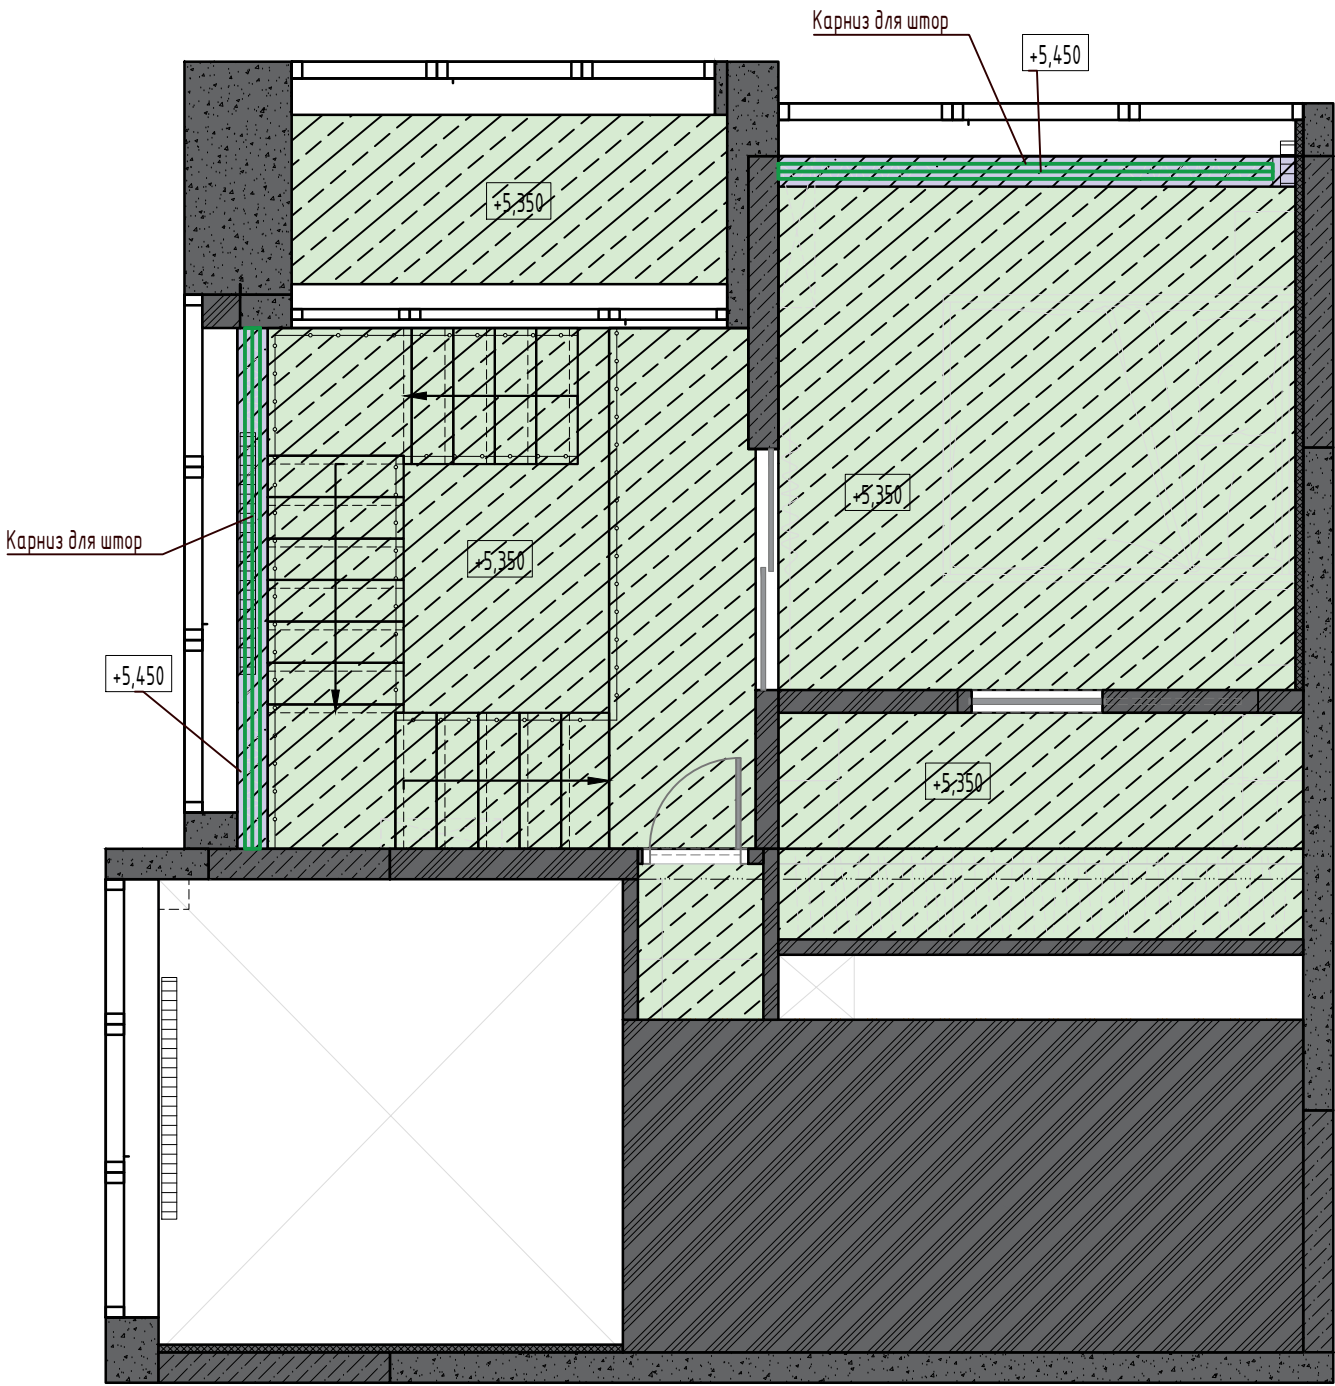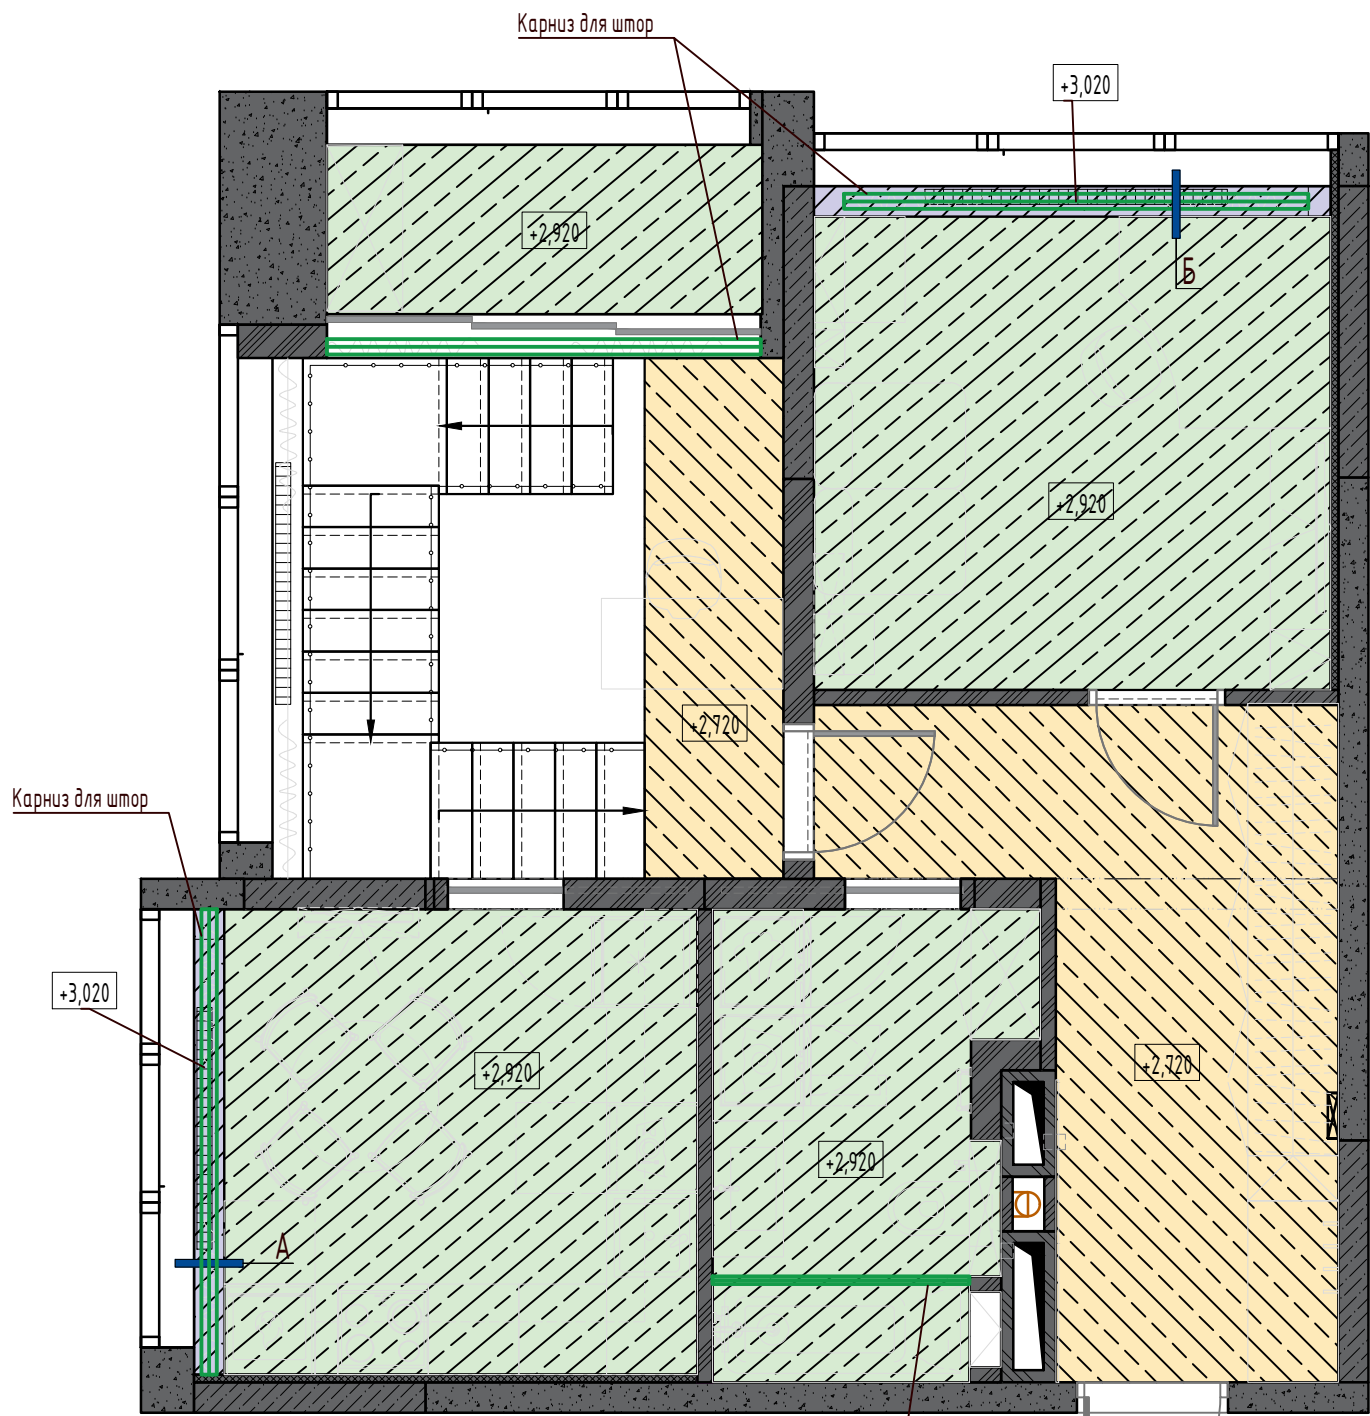



УЗЕЛ А
Формирование ниши для штор

УЗЕЛ Б
Формирование ниши для штор с LED подсветкой

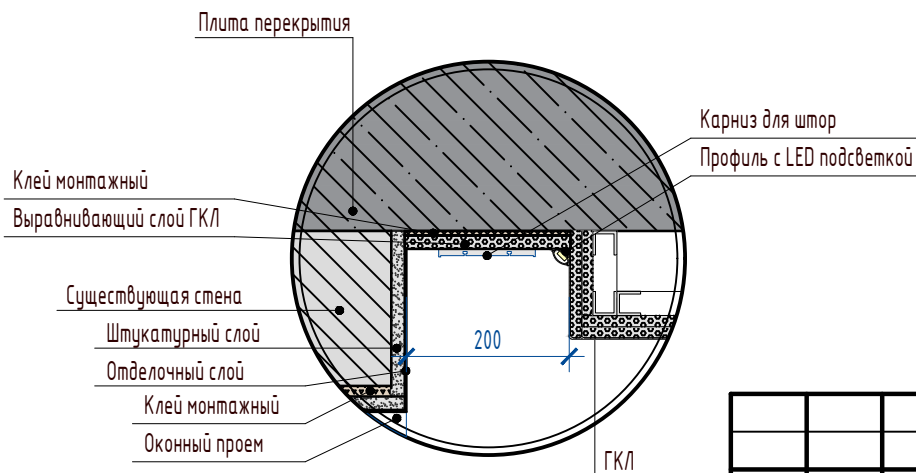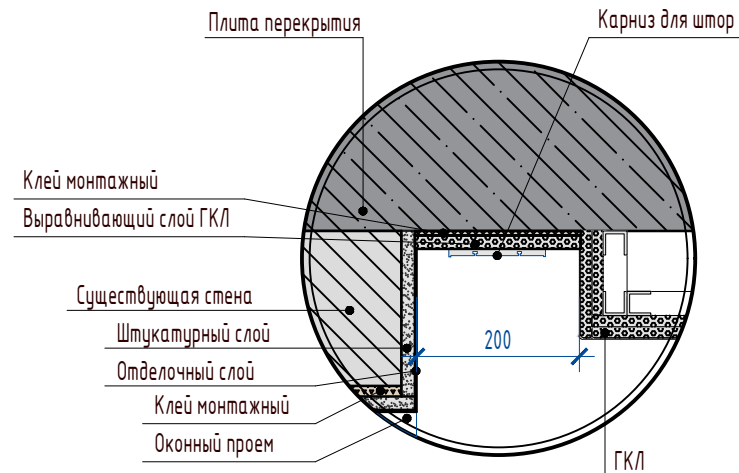

Ведомость отделки потолков

№ Типа потолка	Условное обозначение	Тип отделки	Кол-во (м², м.п.)
		Потолок ГКЛ(ГКЛВ) + покраска в белый цвет	61.3
			13.4
			2.7
			77.4

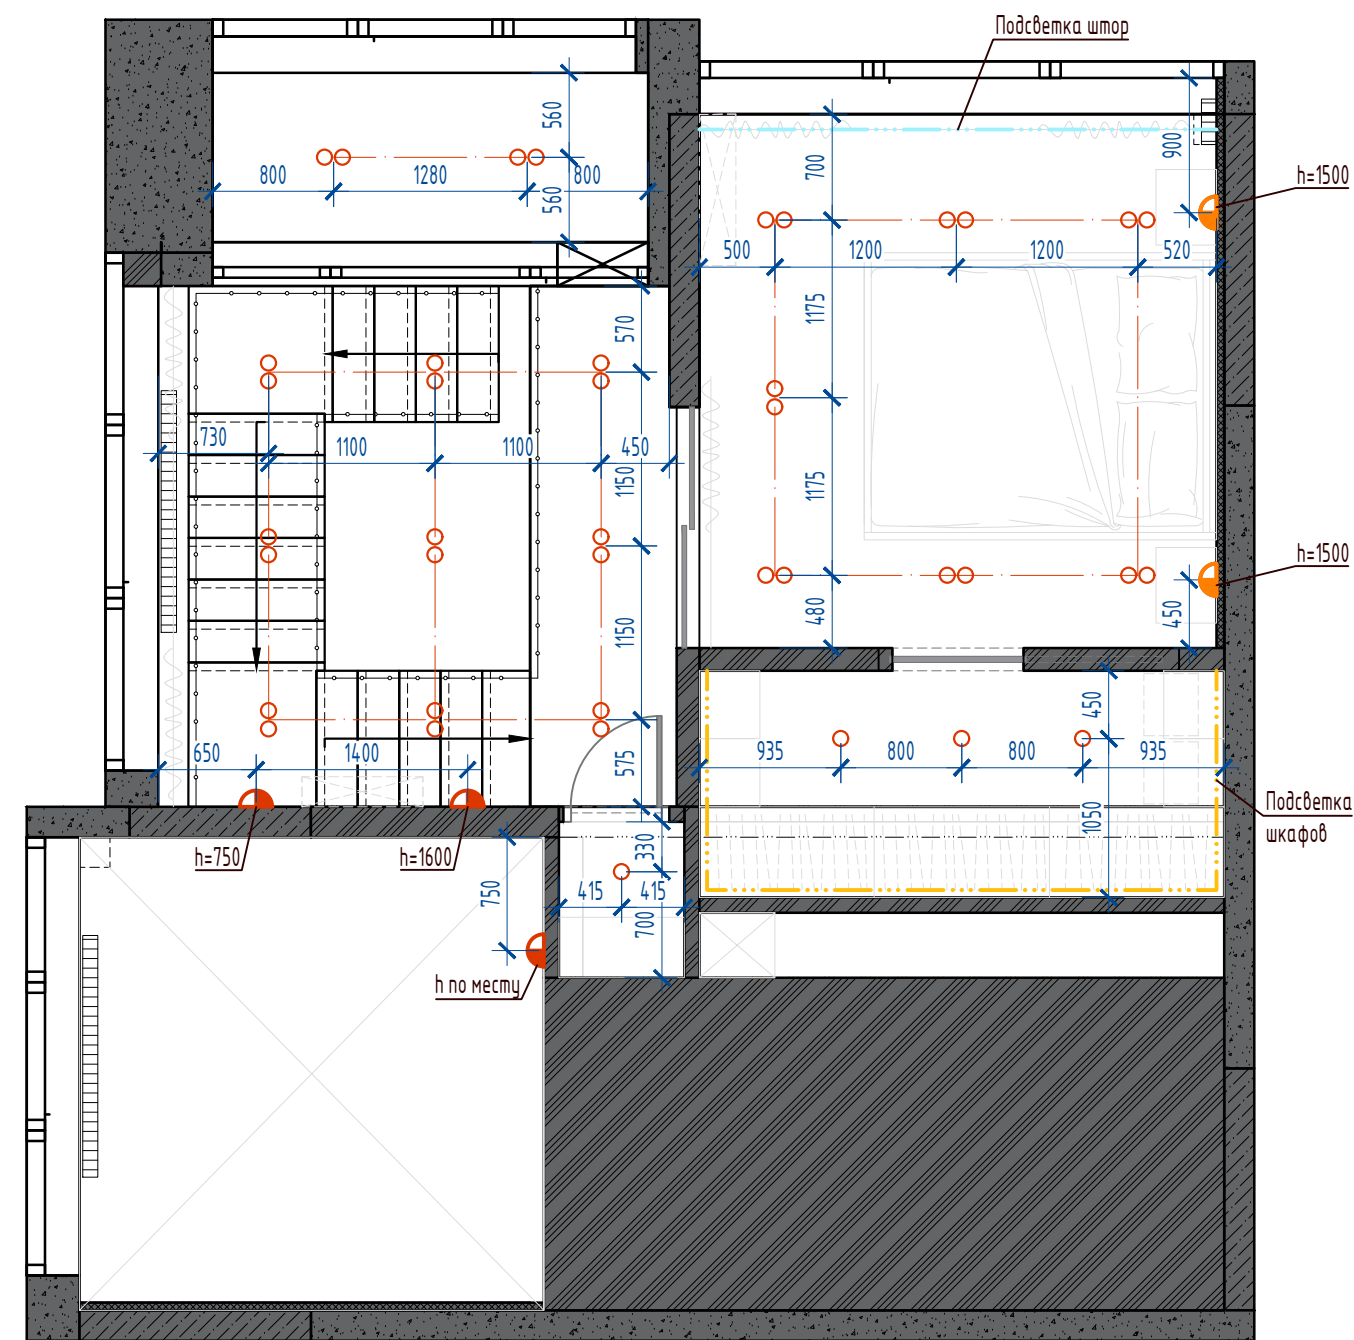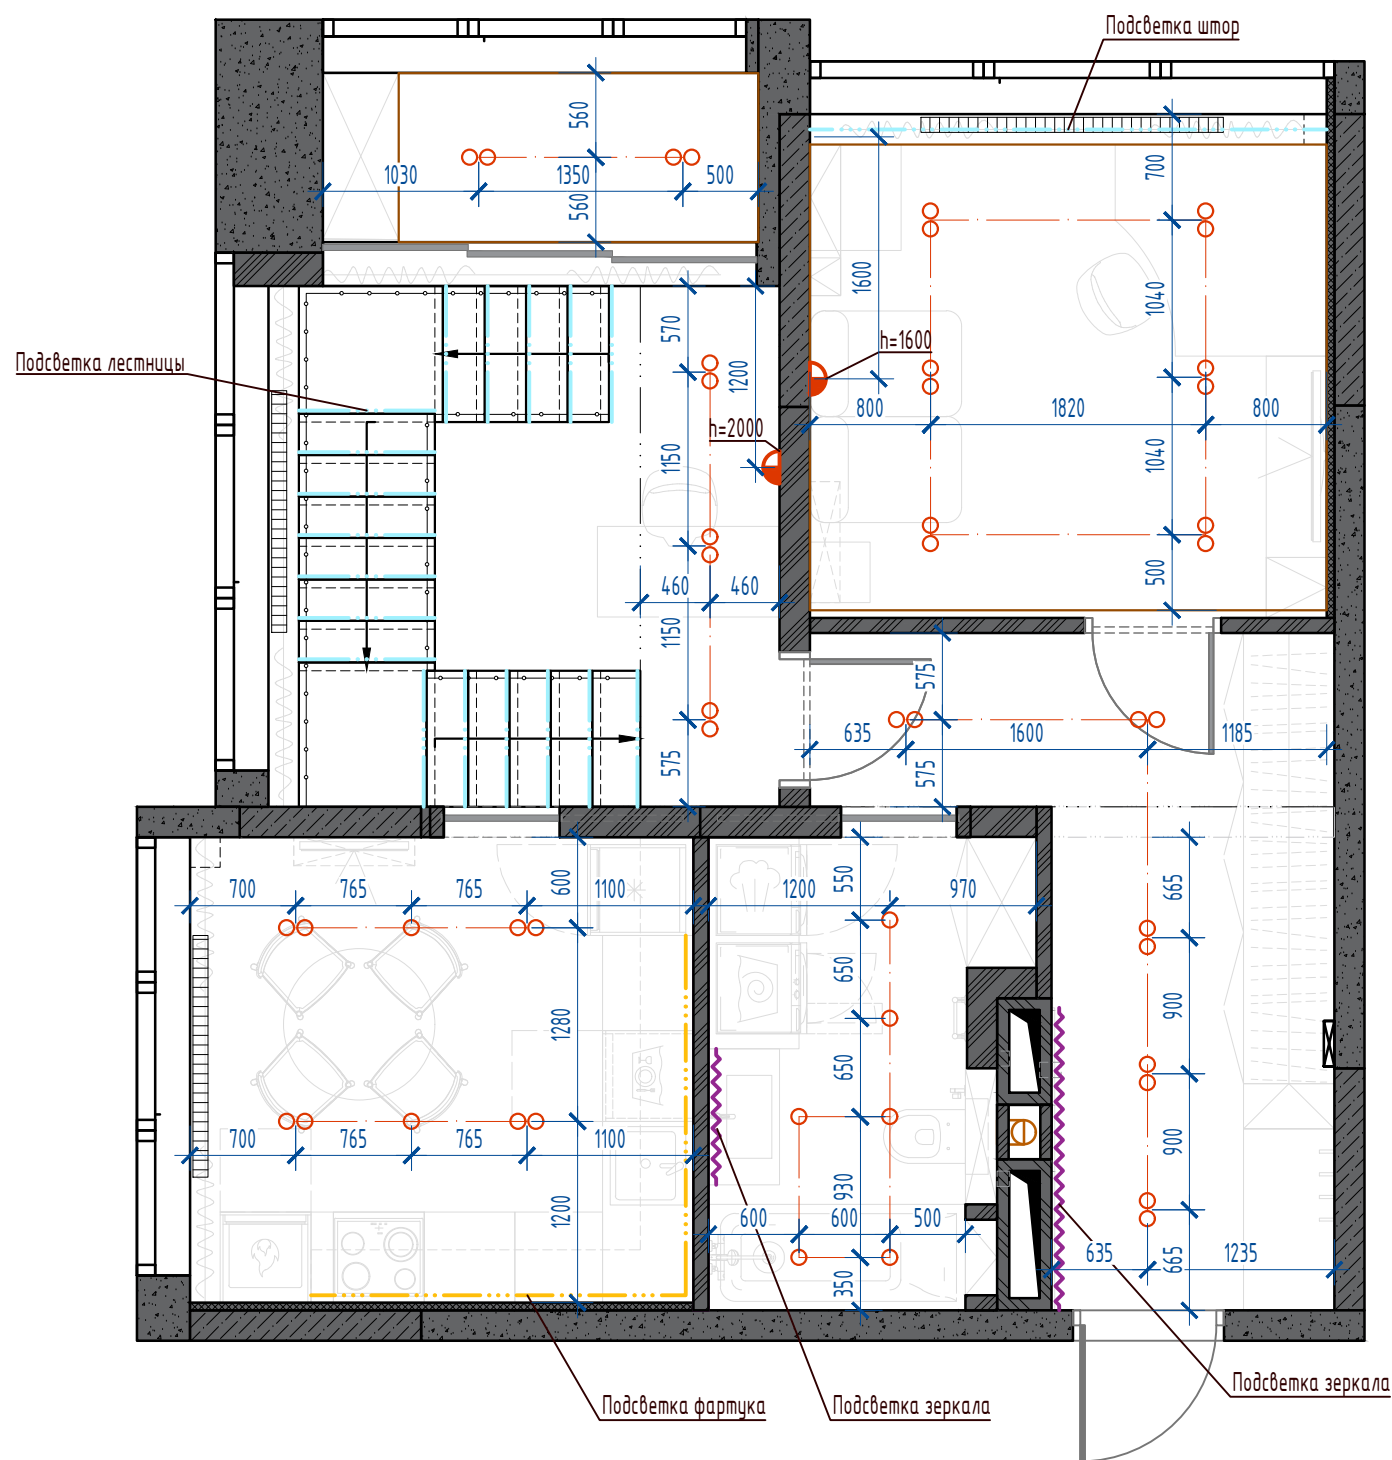

Ведомость осветительных приборов



Вид	Наименование	Кол-во (шт, м.п)
○	Встраиваемый точечный светильник	88
◐	Настенный светильник (бра) №1	5
◑	Настенный светильник (бра) №2	2
— — — — —	Мебельная светодиодная подсветка	
~~~~~	Светодиодная подсветка в составе зеркала	
— · — · — · —	Светодиодная подсветка	

- Примечание:
- Все размеры указаны до центра светильника. Все высоты даны от УЧП.
  - Все размеры и привязки уточнить и корректировать по месту в связи с конструктивными особенностями элементов интерьера.
  - Для возможности редактирования рекомендуется оставлять выводы достаточной длины.
  - Тип и способ установки светильников уточнить при выборе у поставщика.
  - При замене светильников может измениться их расположение и кол-во.
  - Предусмотреть доступ ко всем трансформаторам светодиодного освещения.
  - Светодиодную ленту относящуюся к мебели, заказать вместе с мебелью.
  - В спецификацию не включена светодиодная лента относящаяся к мебели.

Изм.	Кол.уч.	Лист	№ док.	Подп.	Дата	План расположения осветительных приборов	Лист
							11

Копировал

Формат А3

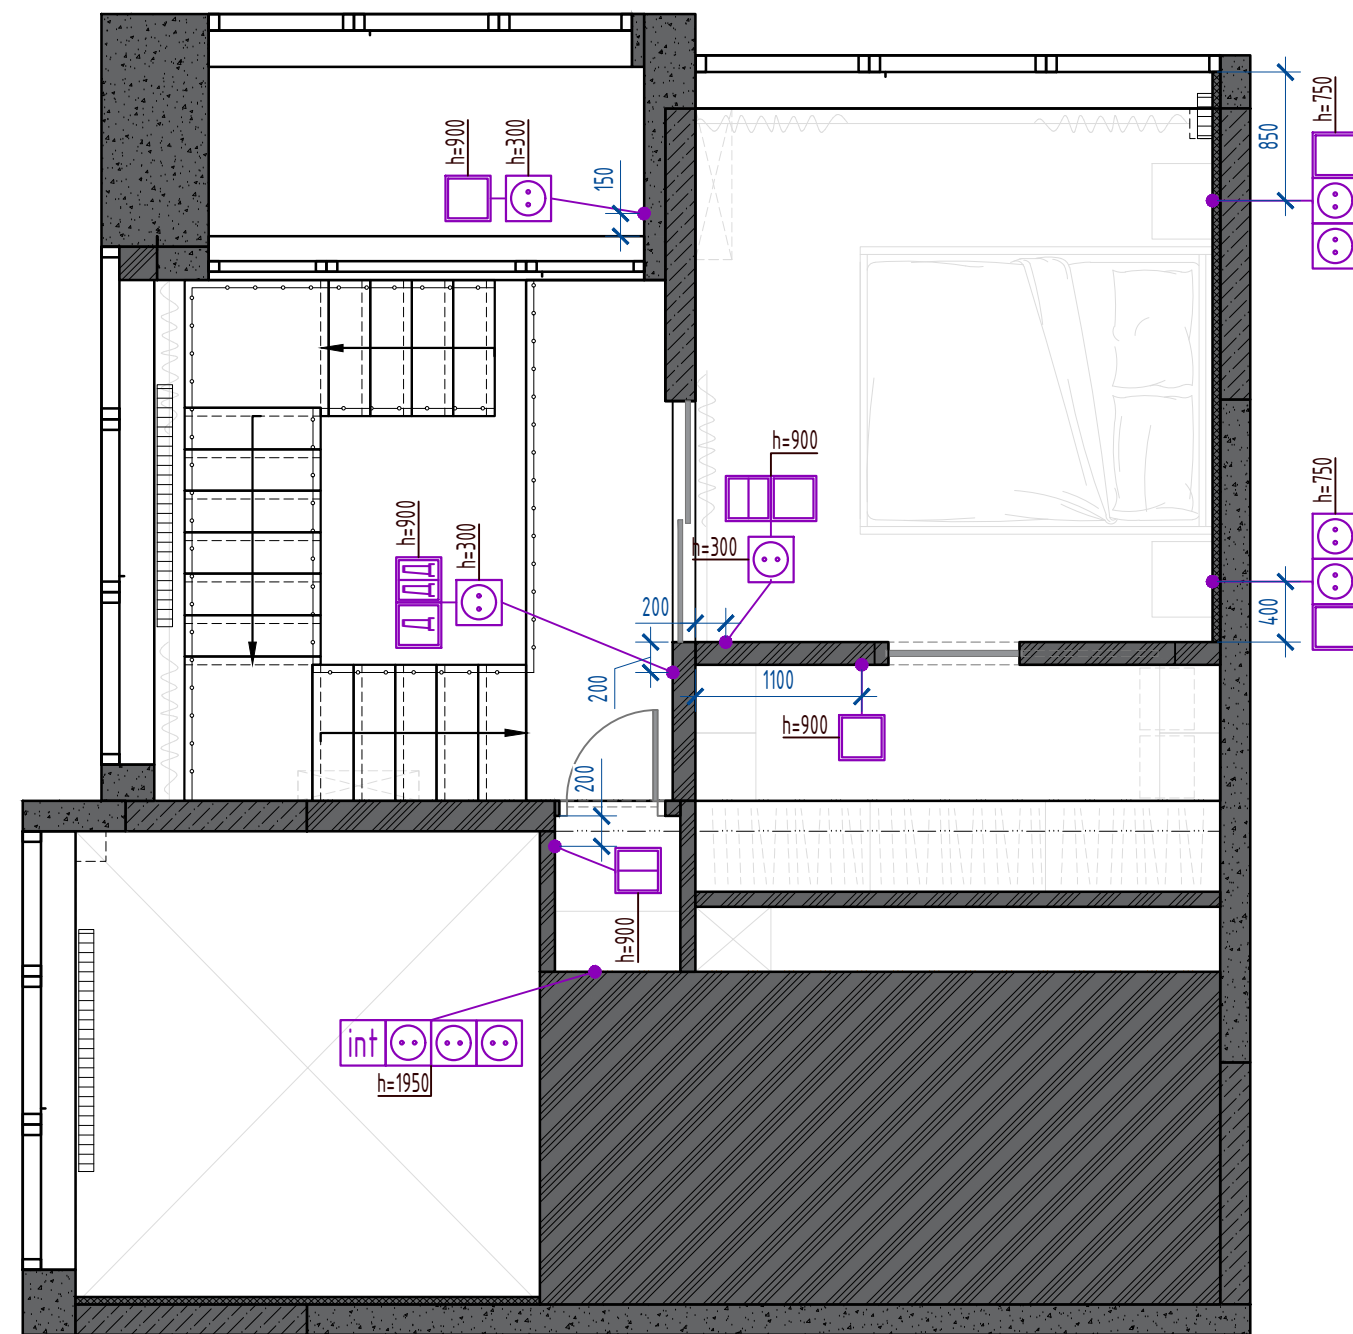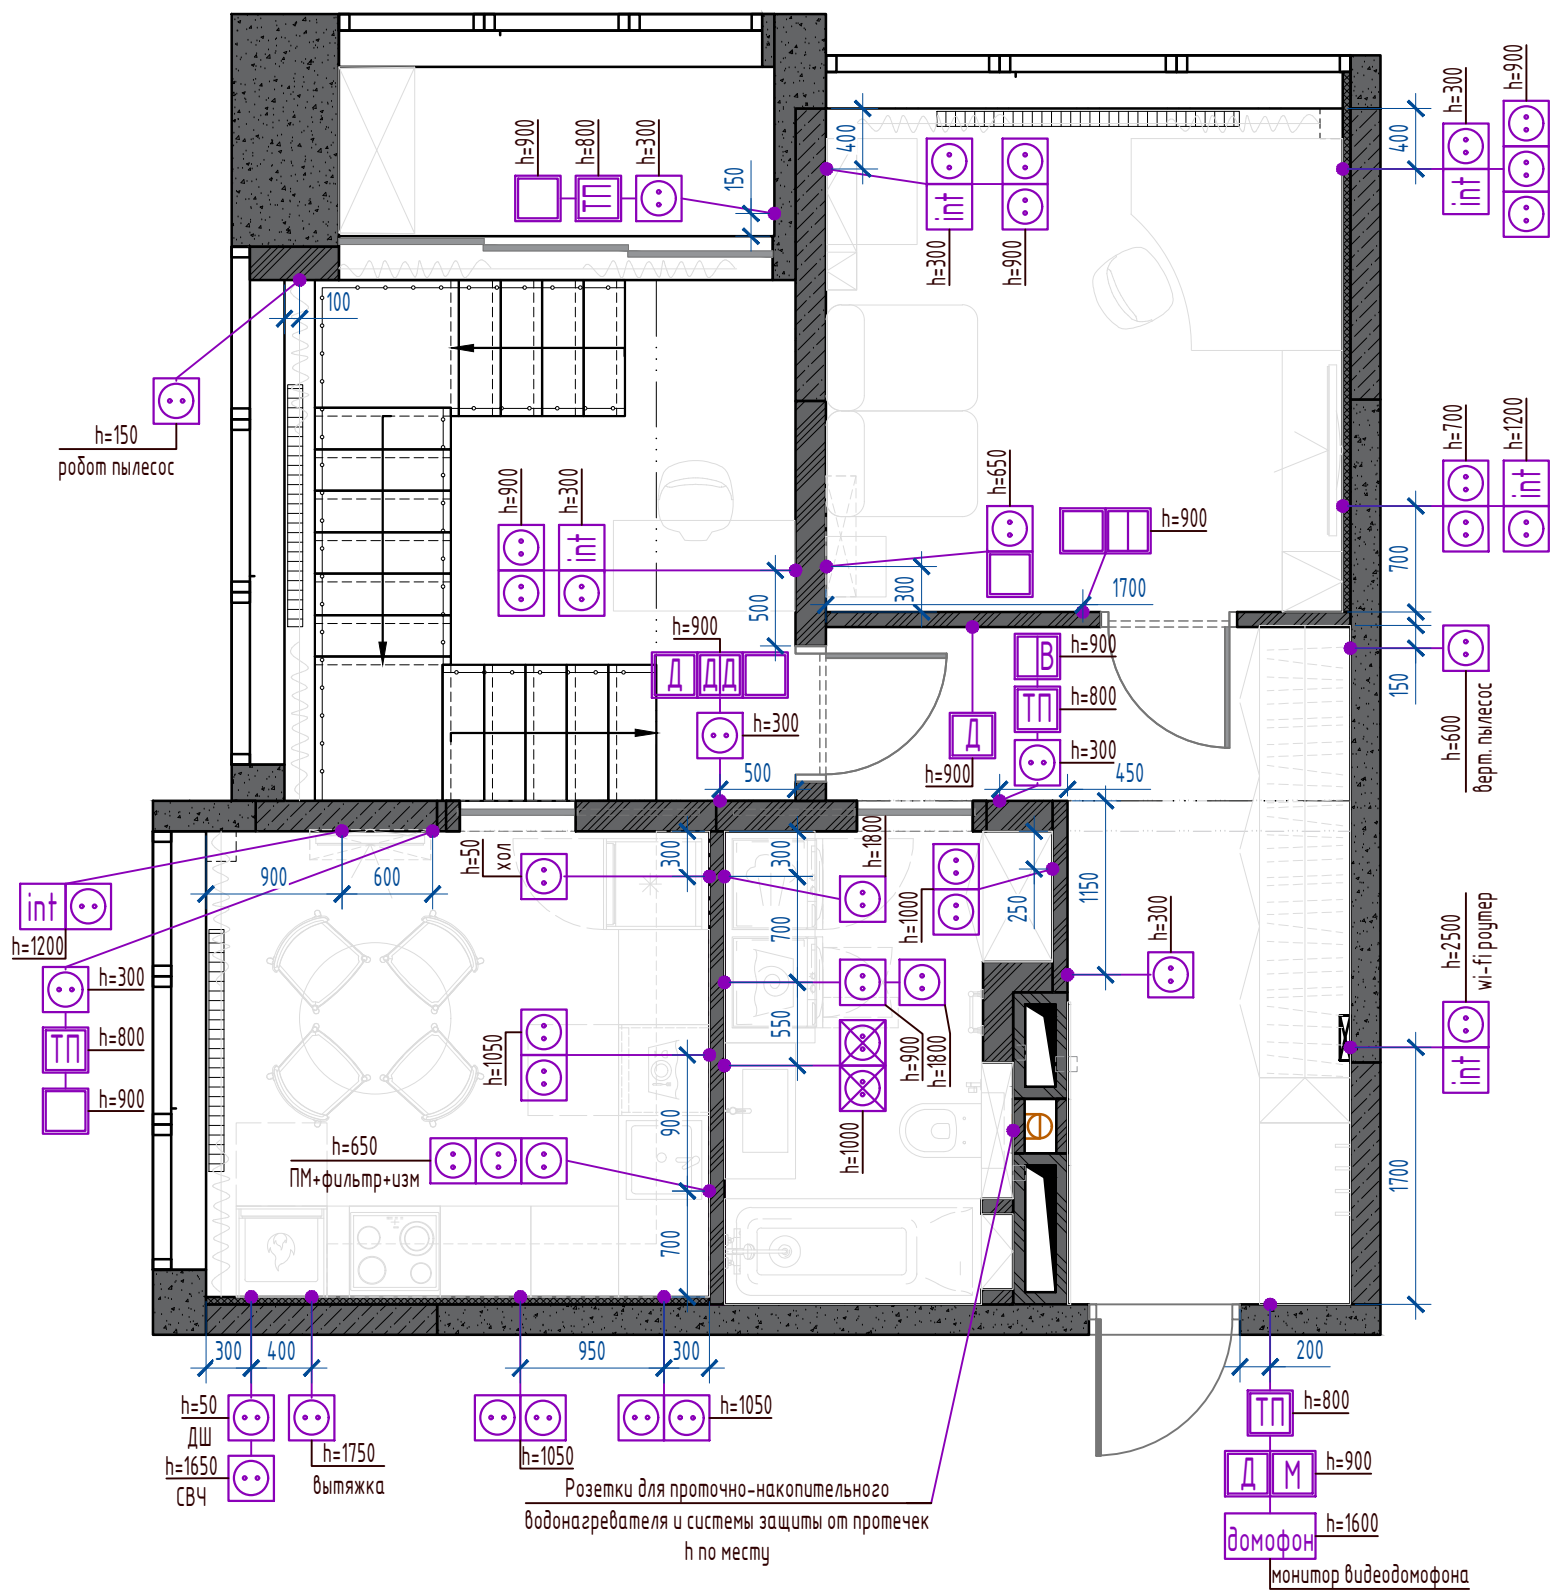

Экспликация электрики

Вид	Наименование	Кол-во
	Розетка 220V	51
	Розетка 220В влагозащищенная	2
	Выключатель 1-клавишный	14
	Выключатель 2-клавишный	6
	Терморегулятор (в своей рамке)	4
	Internet-розетка	7
	Домофон	1

Сводная таблица рамок

Вид	Тип	Кол-во
	Рамка 1 поста	28
	Рамка 2 поста	20
	Рамка 3 поста	4
	Рамка 4 поста	1

Условные обозначения:

	- розетка 220В		- электровывод
	- розетка 220В влагозащищенная		- Internet-розетка
	- выключатель 1-кл.		-розетка для вывода кабеля
	- выключатель 1-кл. дублер		-терморегулятор (в отдельной рамке)
	- выключатель 2-кл. дублер		- мастер выключатель (вся электрика, кроме приоритетной группы)

Примечание:



- Высота установки до центра розеток h=300мм от чистого пола, если не указано иное.
- Высота установки до центра выключателей h=900мм от чистого пола, если не указано иное.
- Все размеры указаны до центра механизма и центра рамки. Все высоты даны от УЧП.
- Все размеры и привязки уточнить и корректировать по месту в связи с конструктивными особенностями элементов интерьера.

Изм.	Кол.уч.	Лист	№ док.	Подп.	Дата	Лист
						12

План расположения электрооборудования

Копировал

Формат А3

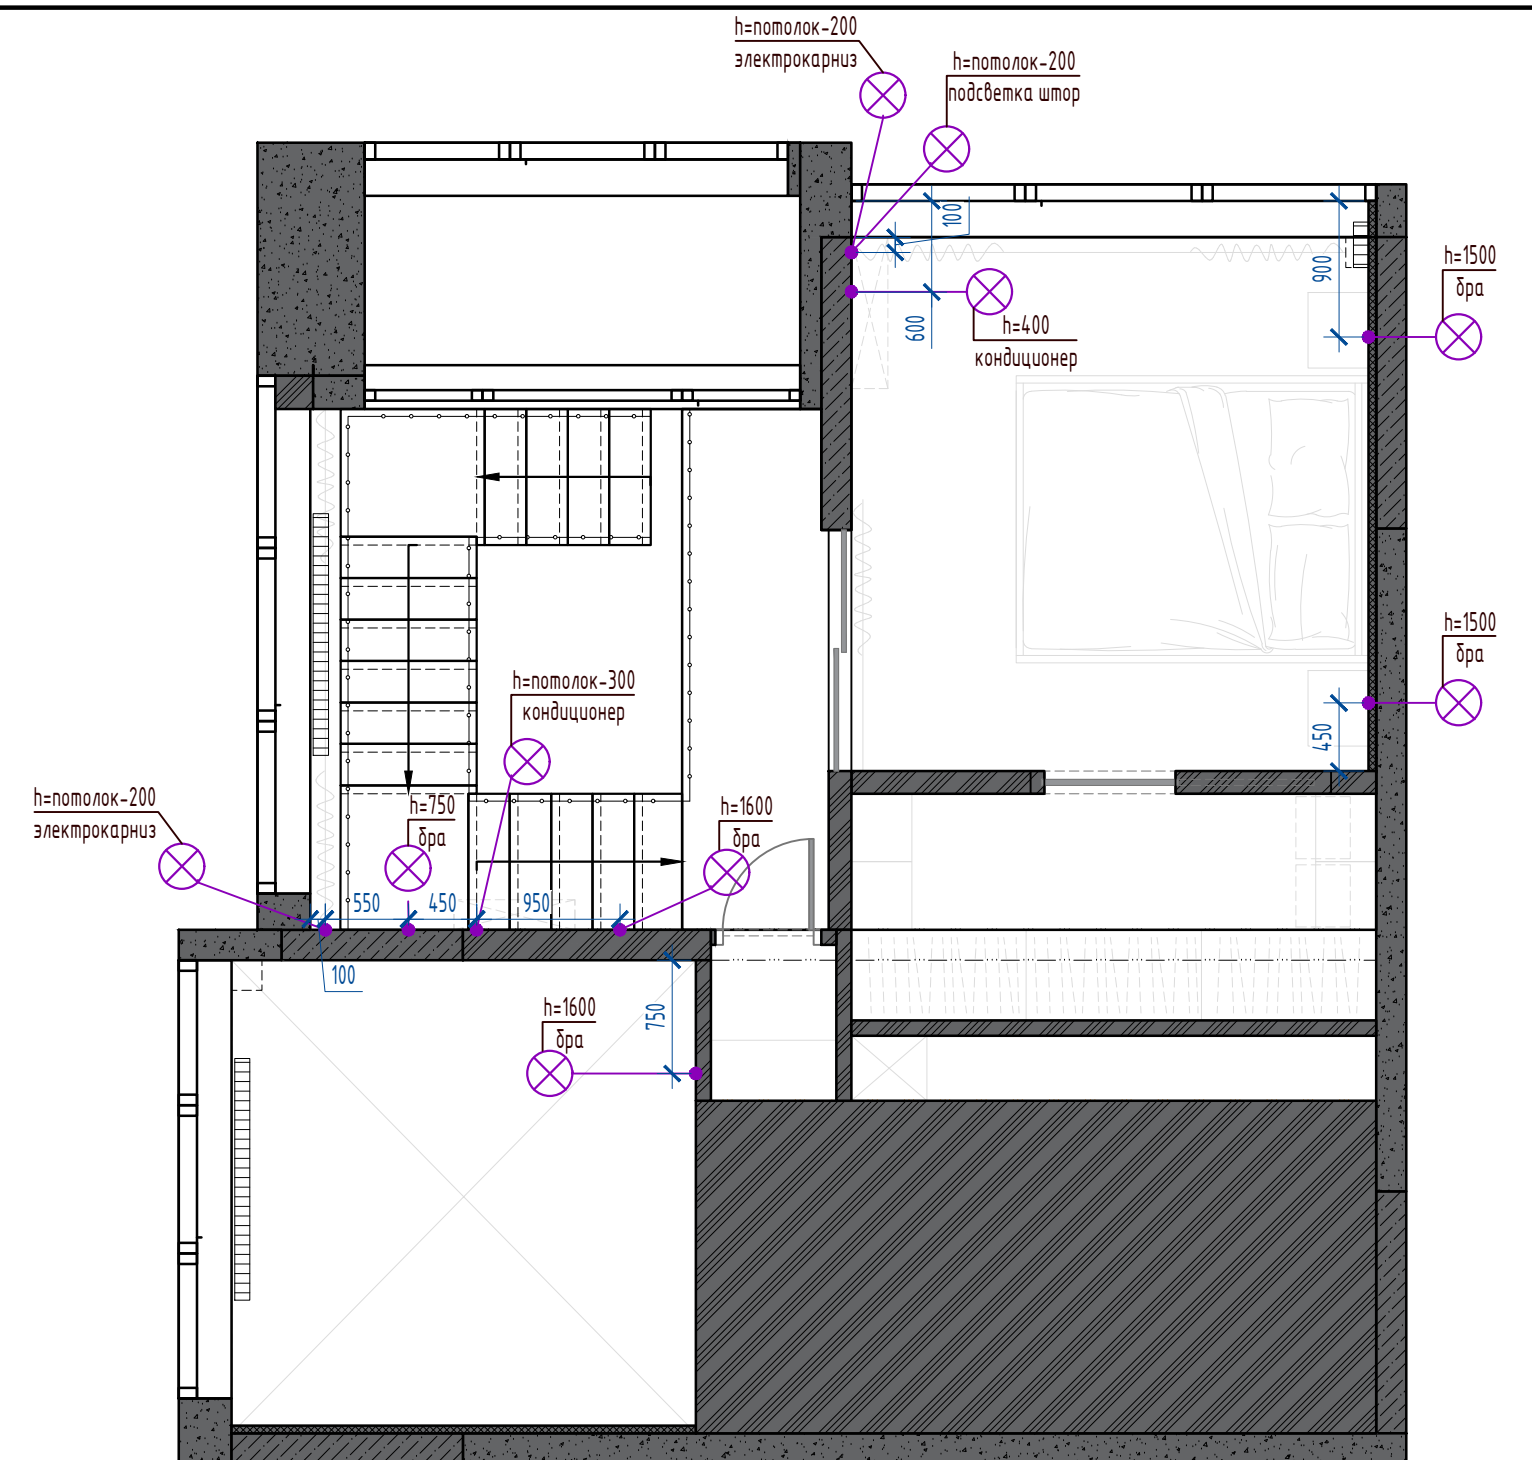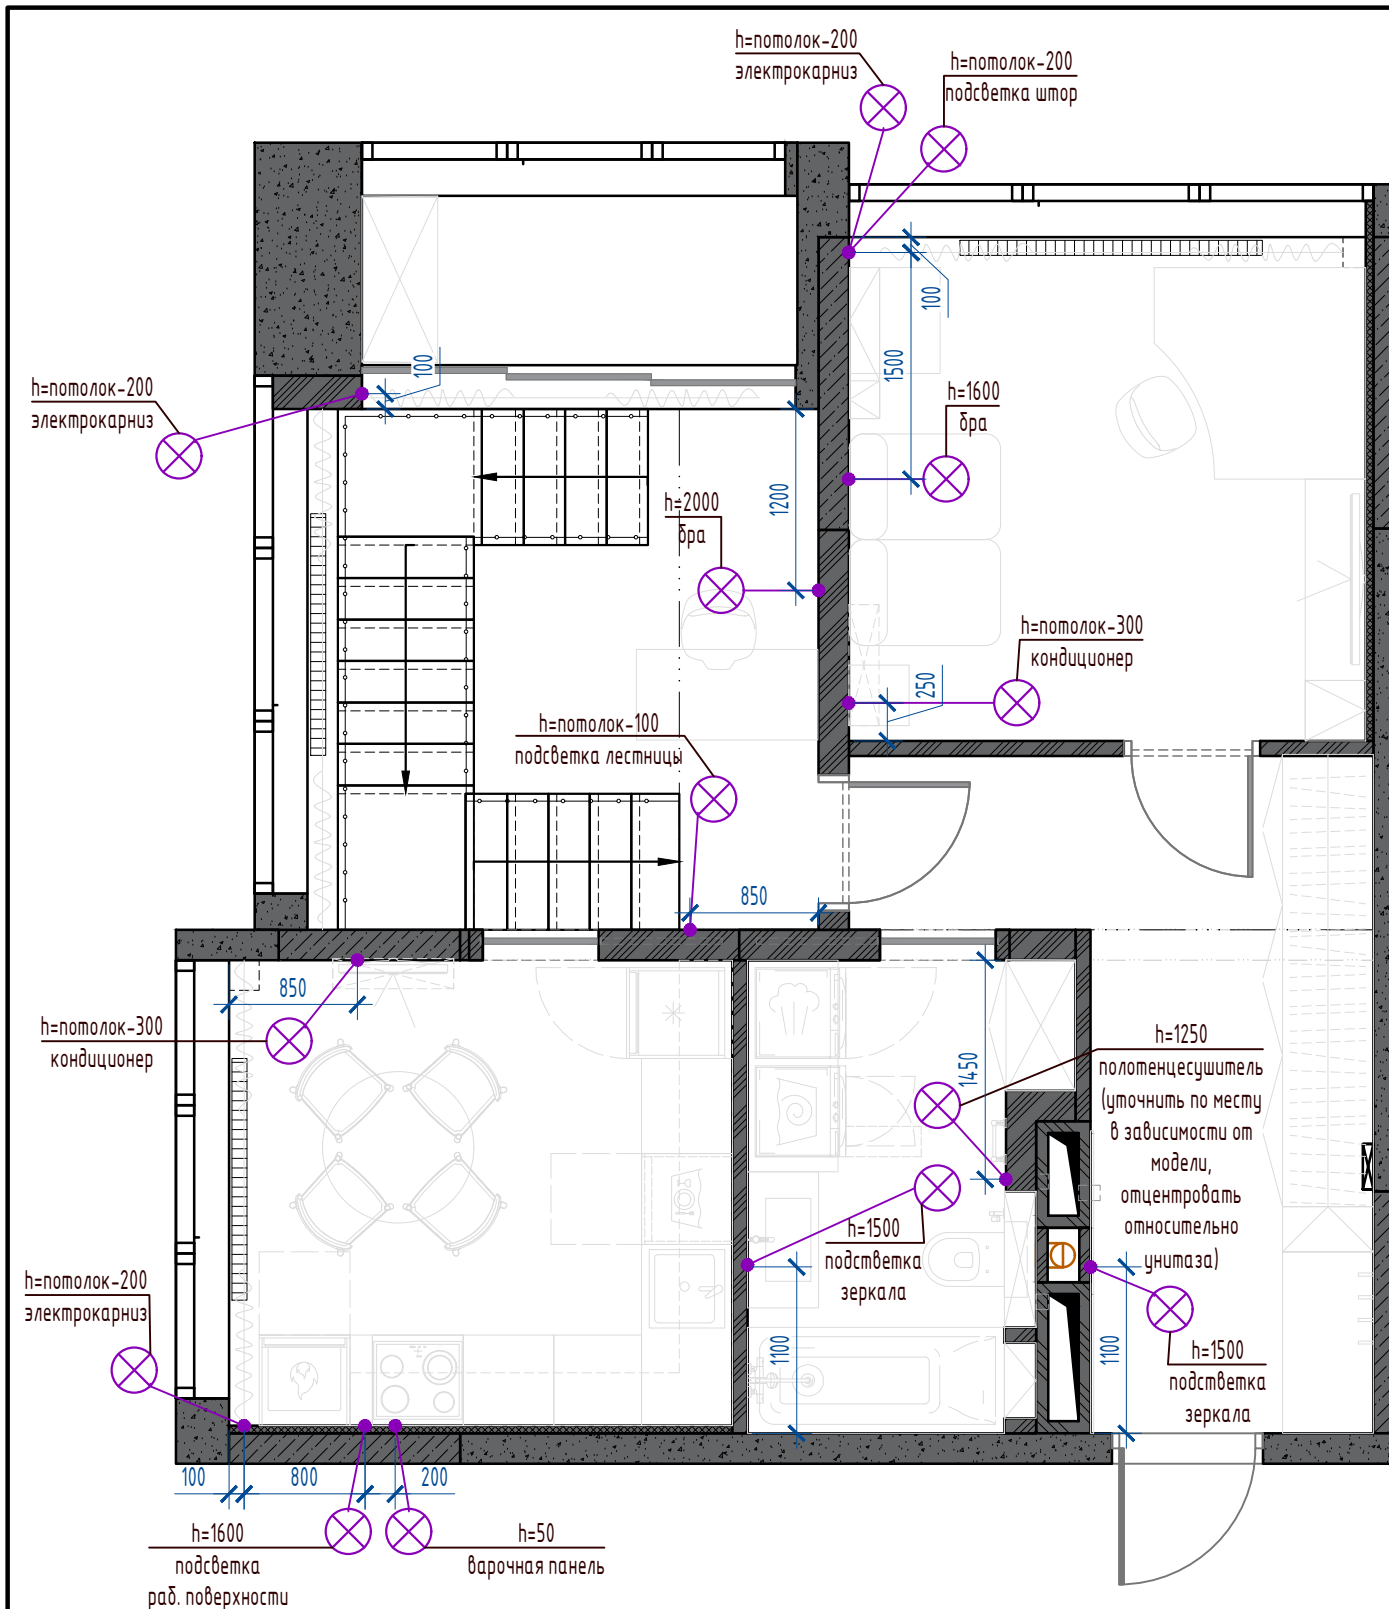

- Примечание:
1. Высота установки до центра розеток  $h=300$  мм от чистого пола, если не указано иное.
  2. Высота установки до центра выключателей  $h=900$  мм от чистого пола, если не указано иное.
  3. Все размеры указаны до центра механизма и центра рамки.
  3. Все высоты даны от УЧП.
  4. Все размеры и привязки уточнить и корректировать по месту в связи с конструктивными особенностями элементов интерьера.



- Условные обозначения:
- розетка 220В
  - розетка 220В влагозащищенная
  - выключатель 1-кл.
  - выключатель 1-кл. дублер
  - выключатель 2-кл. дублер
  - электровывод
  - Internet-розетка
  - розетка для вывода кабеля
  - терморегулятор (в отдельной рамке)
  - мастер выключатель (вся электрика, кроме приоритетной группы)

Изм.	Кол.уч.	Лист	№ док.	Подп.	Дата	План расположения электровыводов		Лист
								13

Копировал

Формат А3



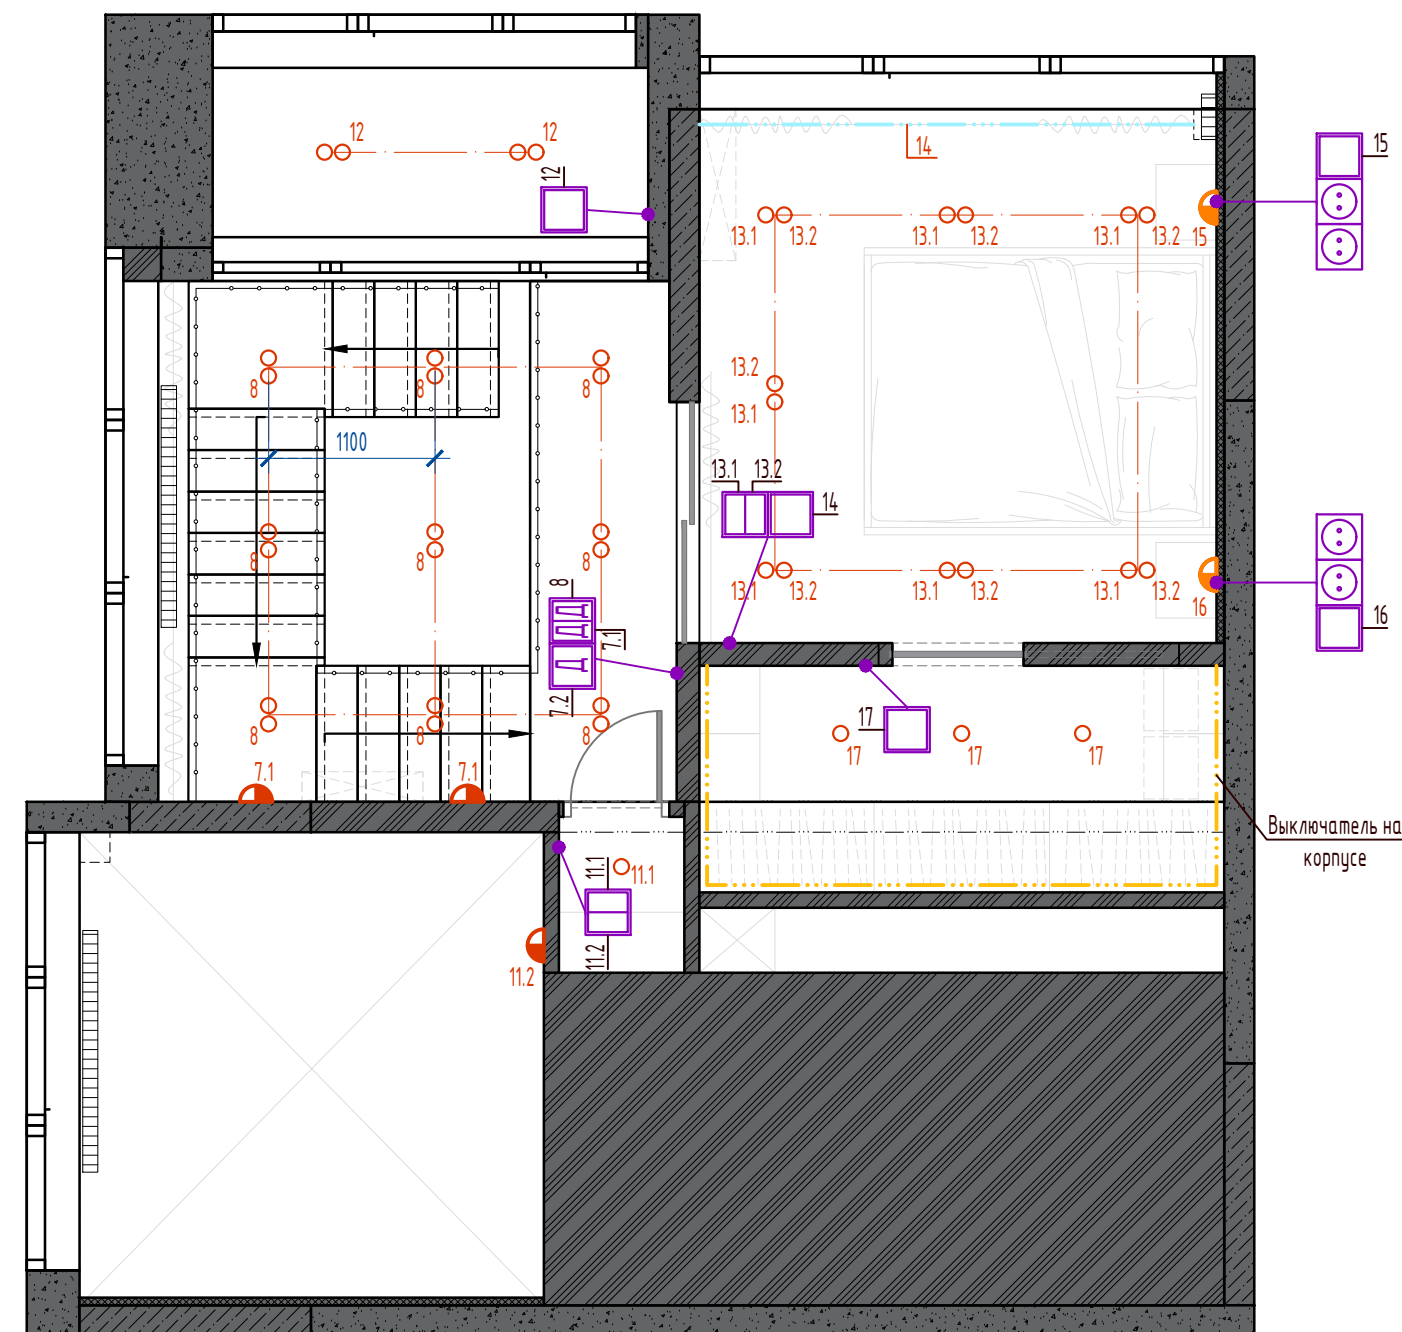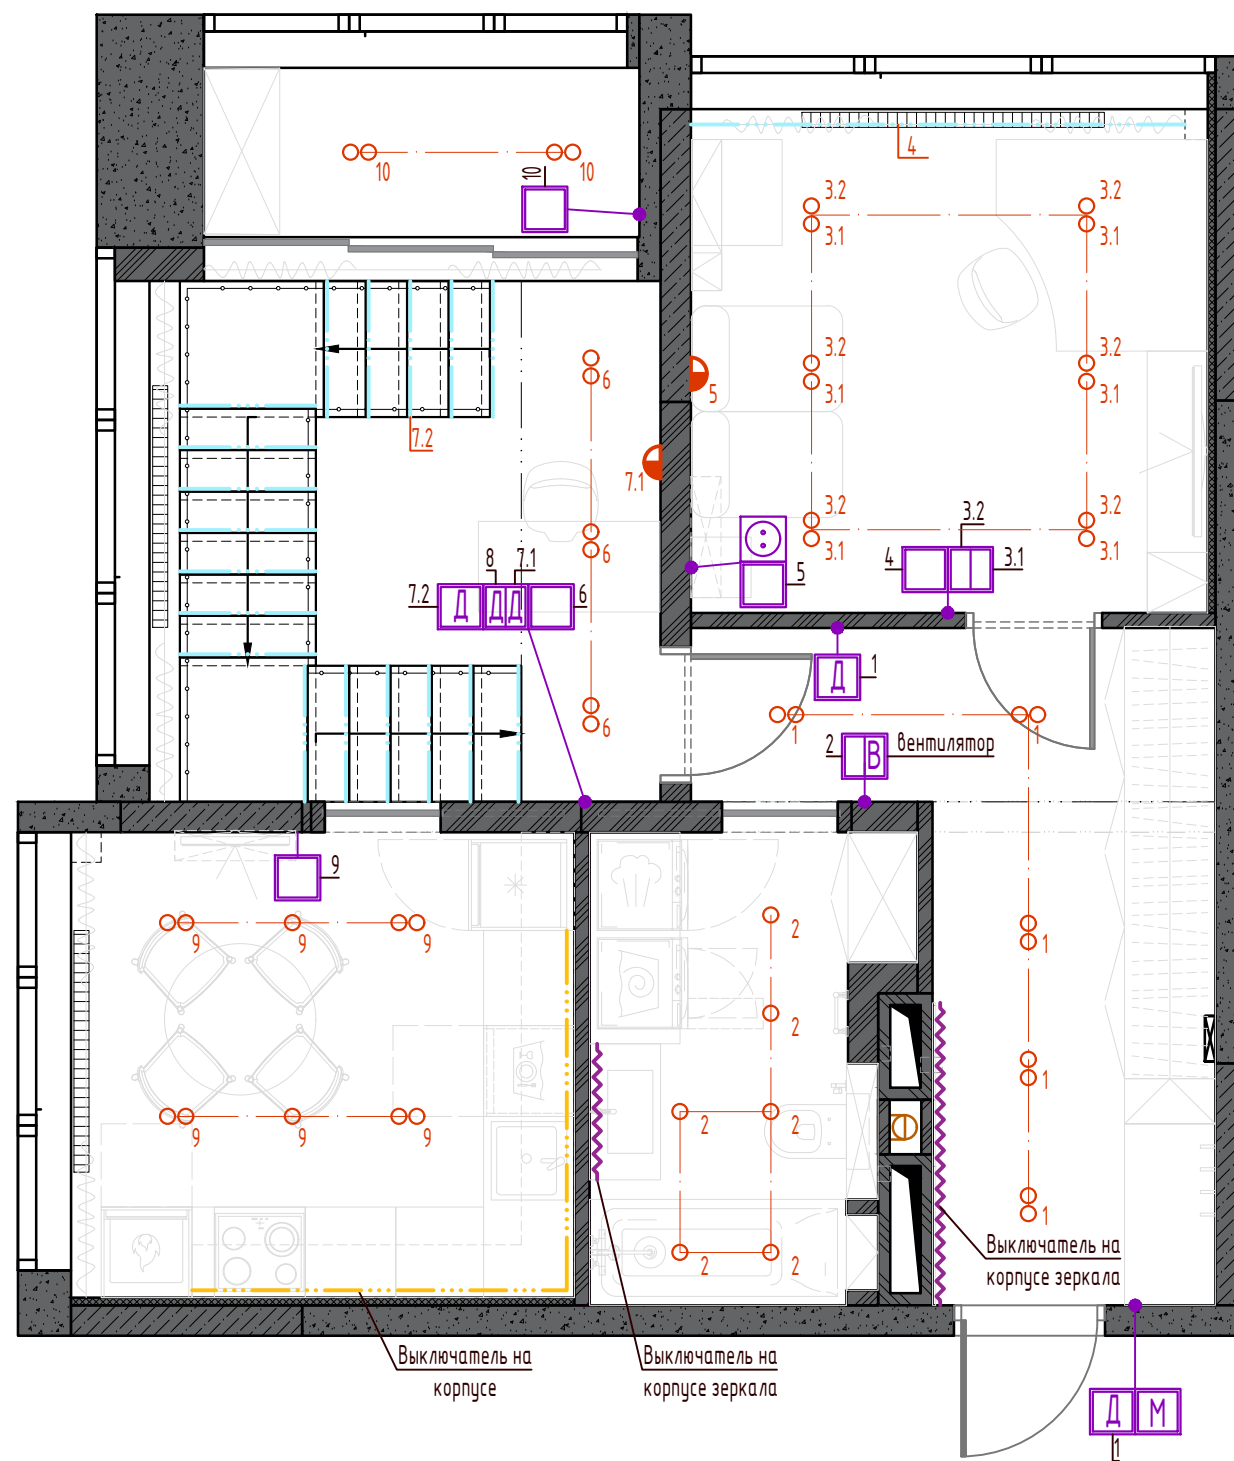





Примечание:

1. На светильники обозначенные * предусмотреть диммируемый блок управления светом.
2. Высота установки до центра розеток  $h=300\text{мм}$  от чистого пола, если не указано иное.
3. Высота установки до центра выключателей  $h=900\text{мм}$  от чистого пола, если не указано иное.
4. Все размеры указаны до центра механизма и центра рамки.
5. Все высоты даны от УЧП.
6. Все размеры и привязки уточнить и корректировать по месту в связи с конструктивными особенностями элементов интерьера.

Изм.	Кол.уч.	Лист	№ док.	Подп.	Дата	Схема привязки групп светильников к выключателям		Лист
								14


Копировал

Формат А3

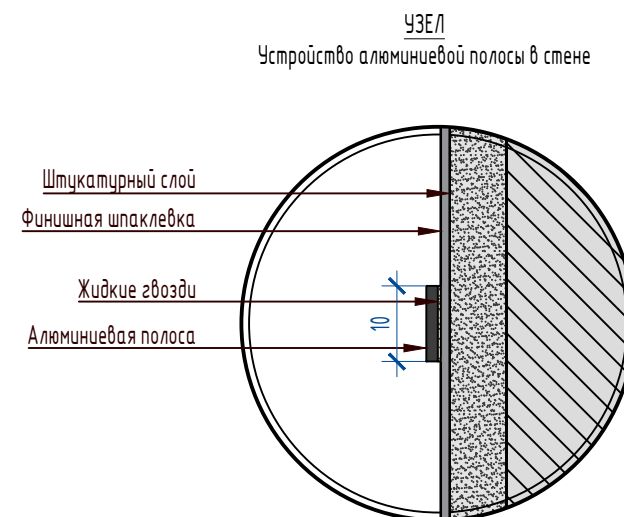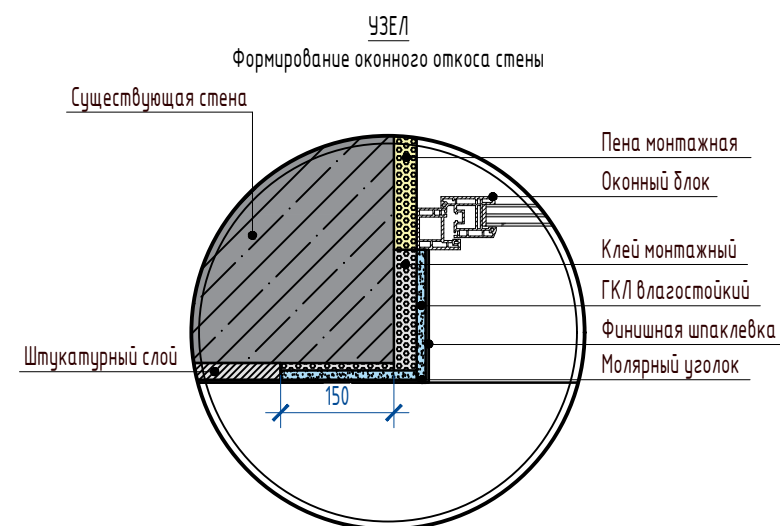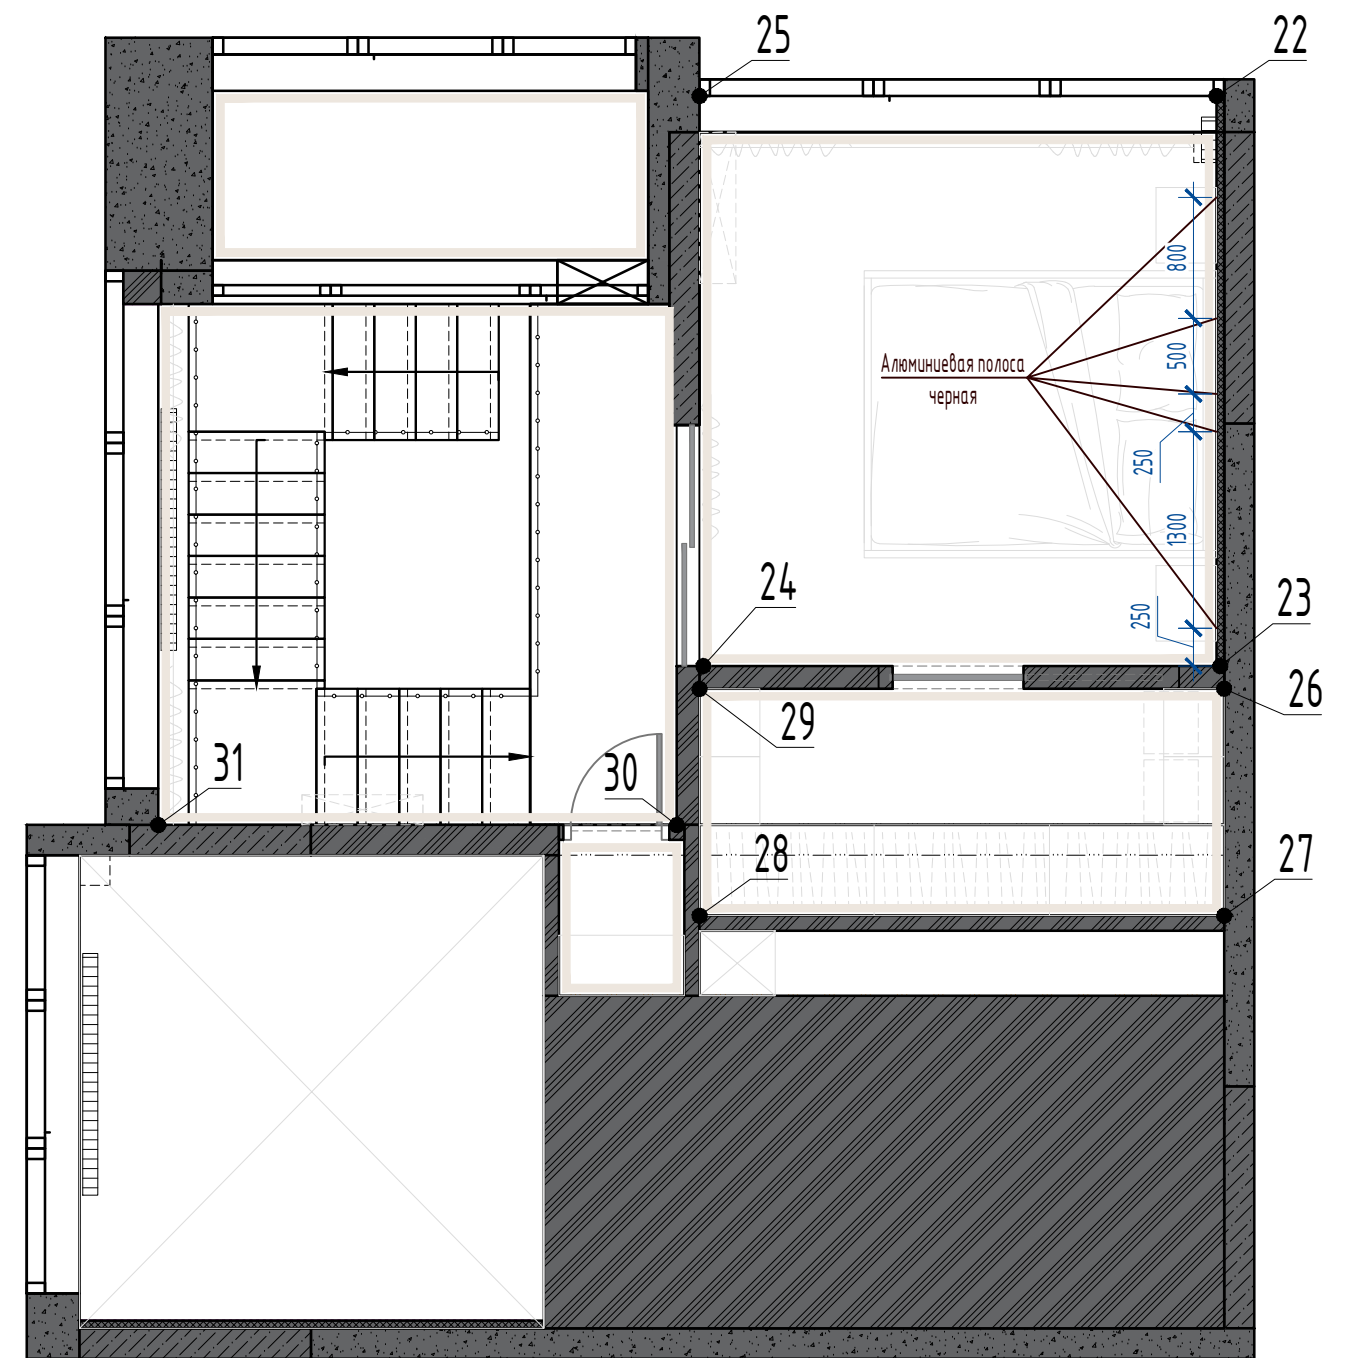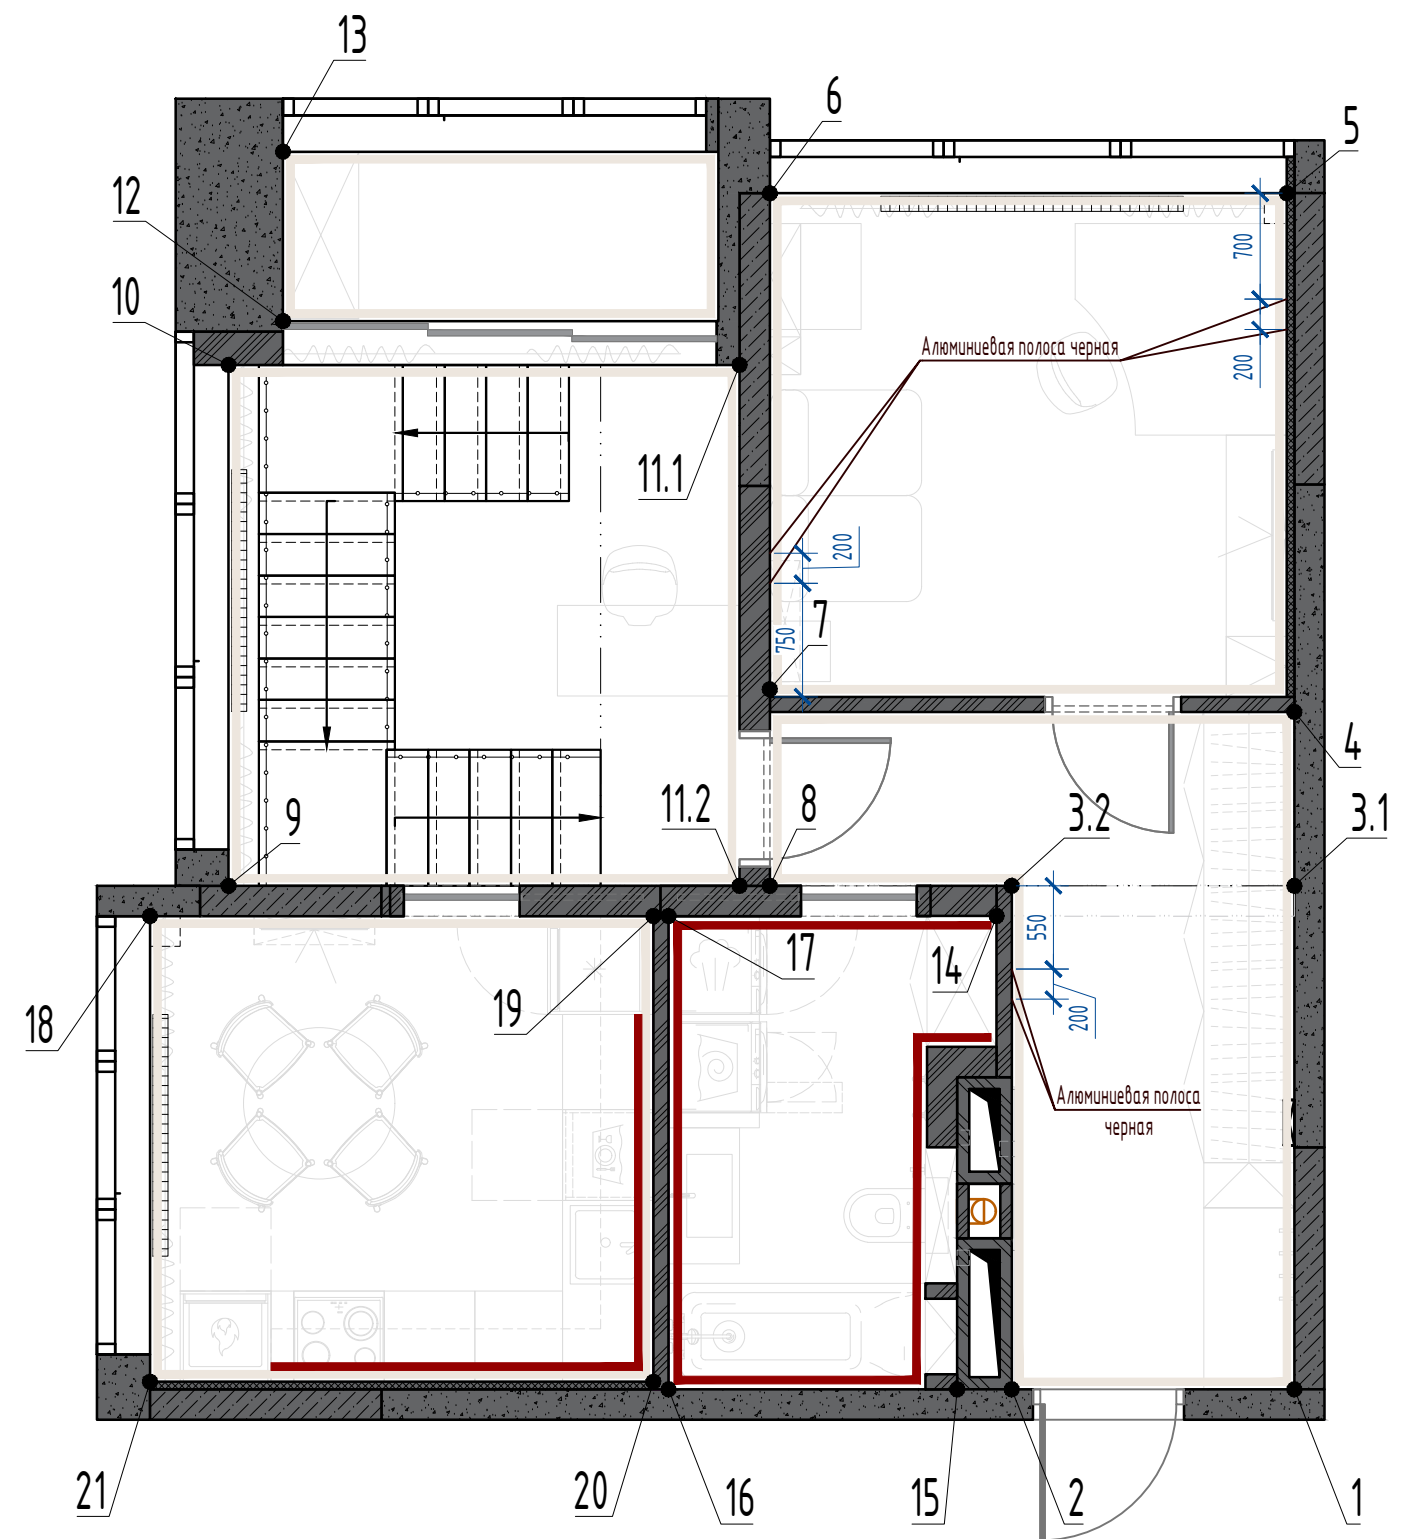


Изм.	Кол.уч.	Лист	№ док.	Подп.	Дата	План-схема отделки стен и маркировки разверток		Лист
						Копировал		15
						Формат А3		

Развертка 1-2

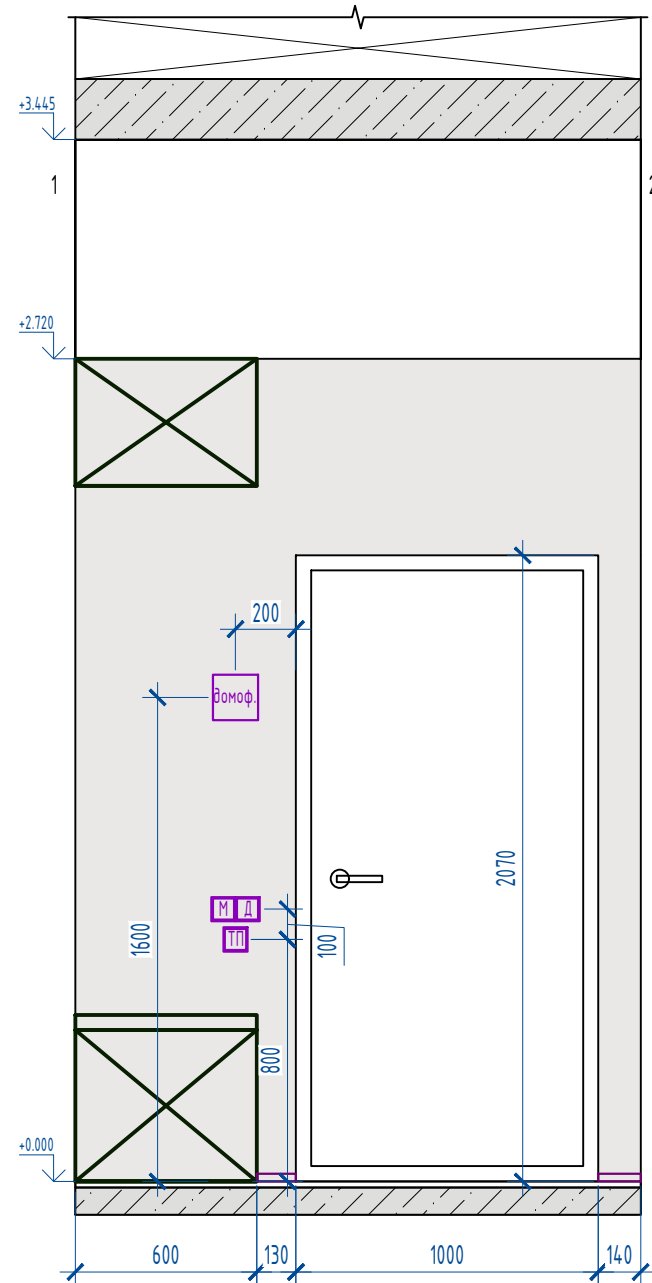

Развертка 2-3.2

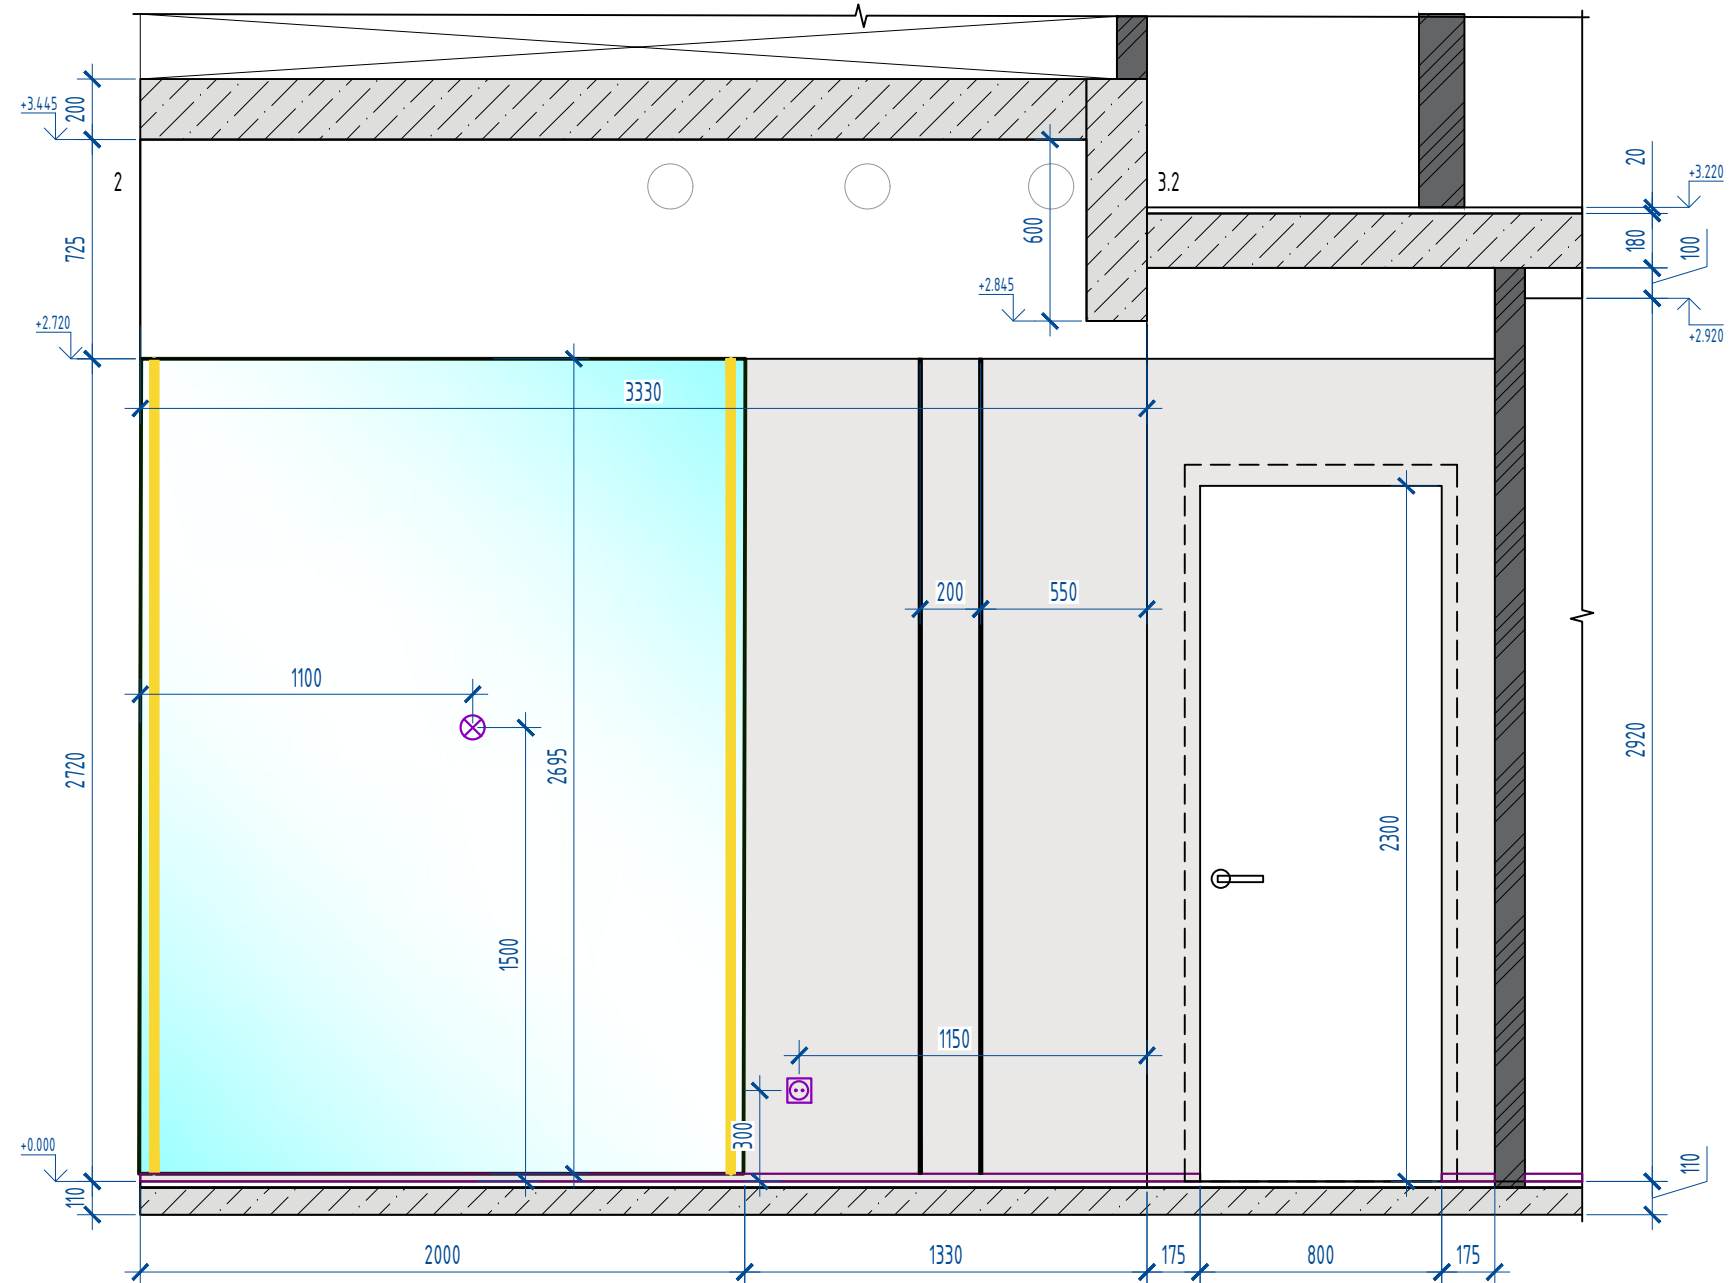

Изм.	Кол.уч.	Лист	№ док.	Подп.	Дата


Развертки 1...3. Прихожая.

Лист

17

Копировал


Формат А3

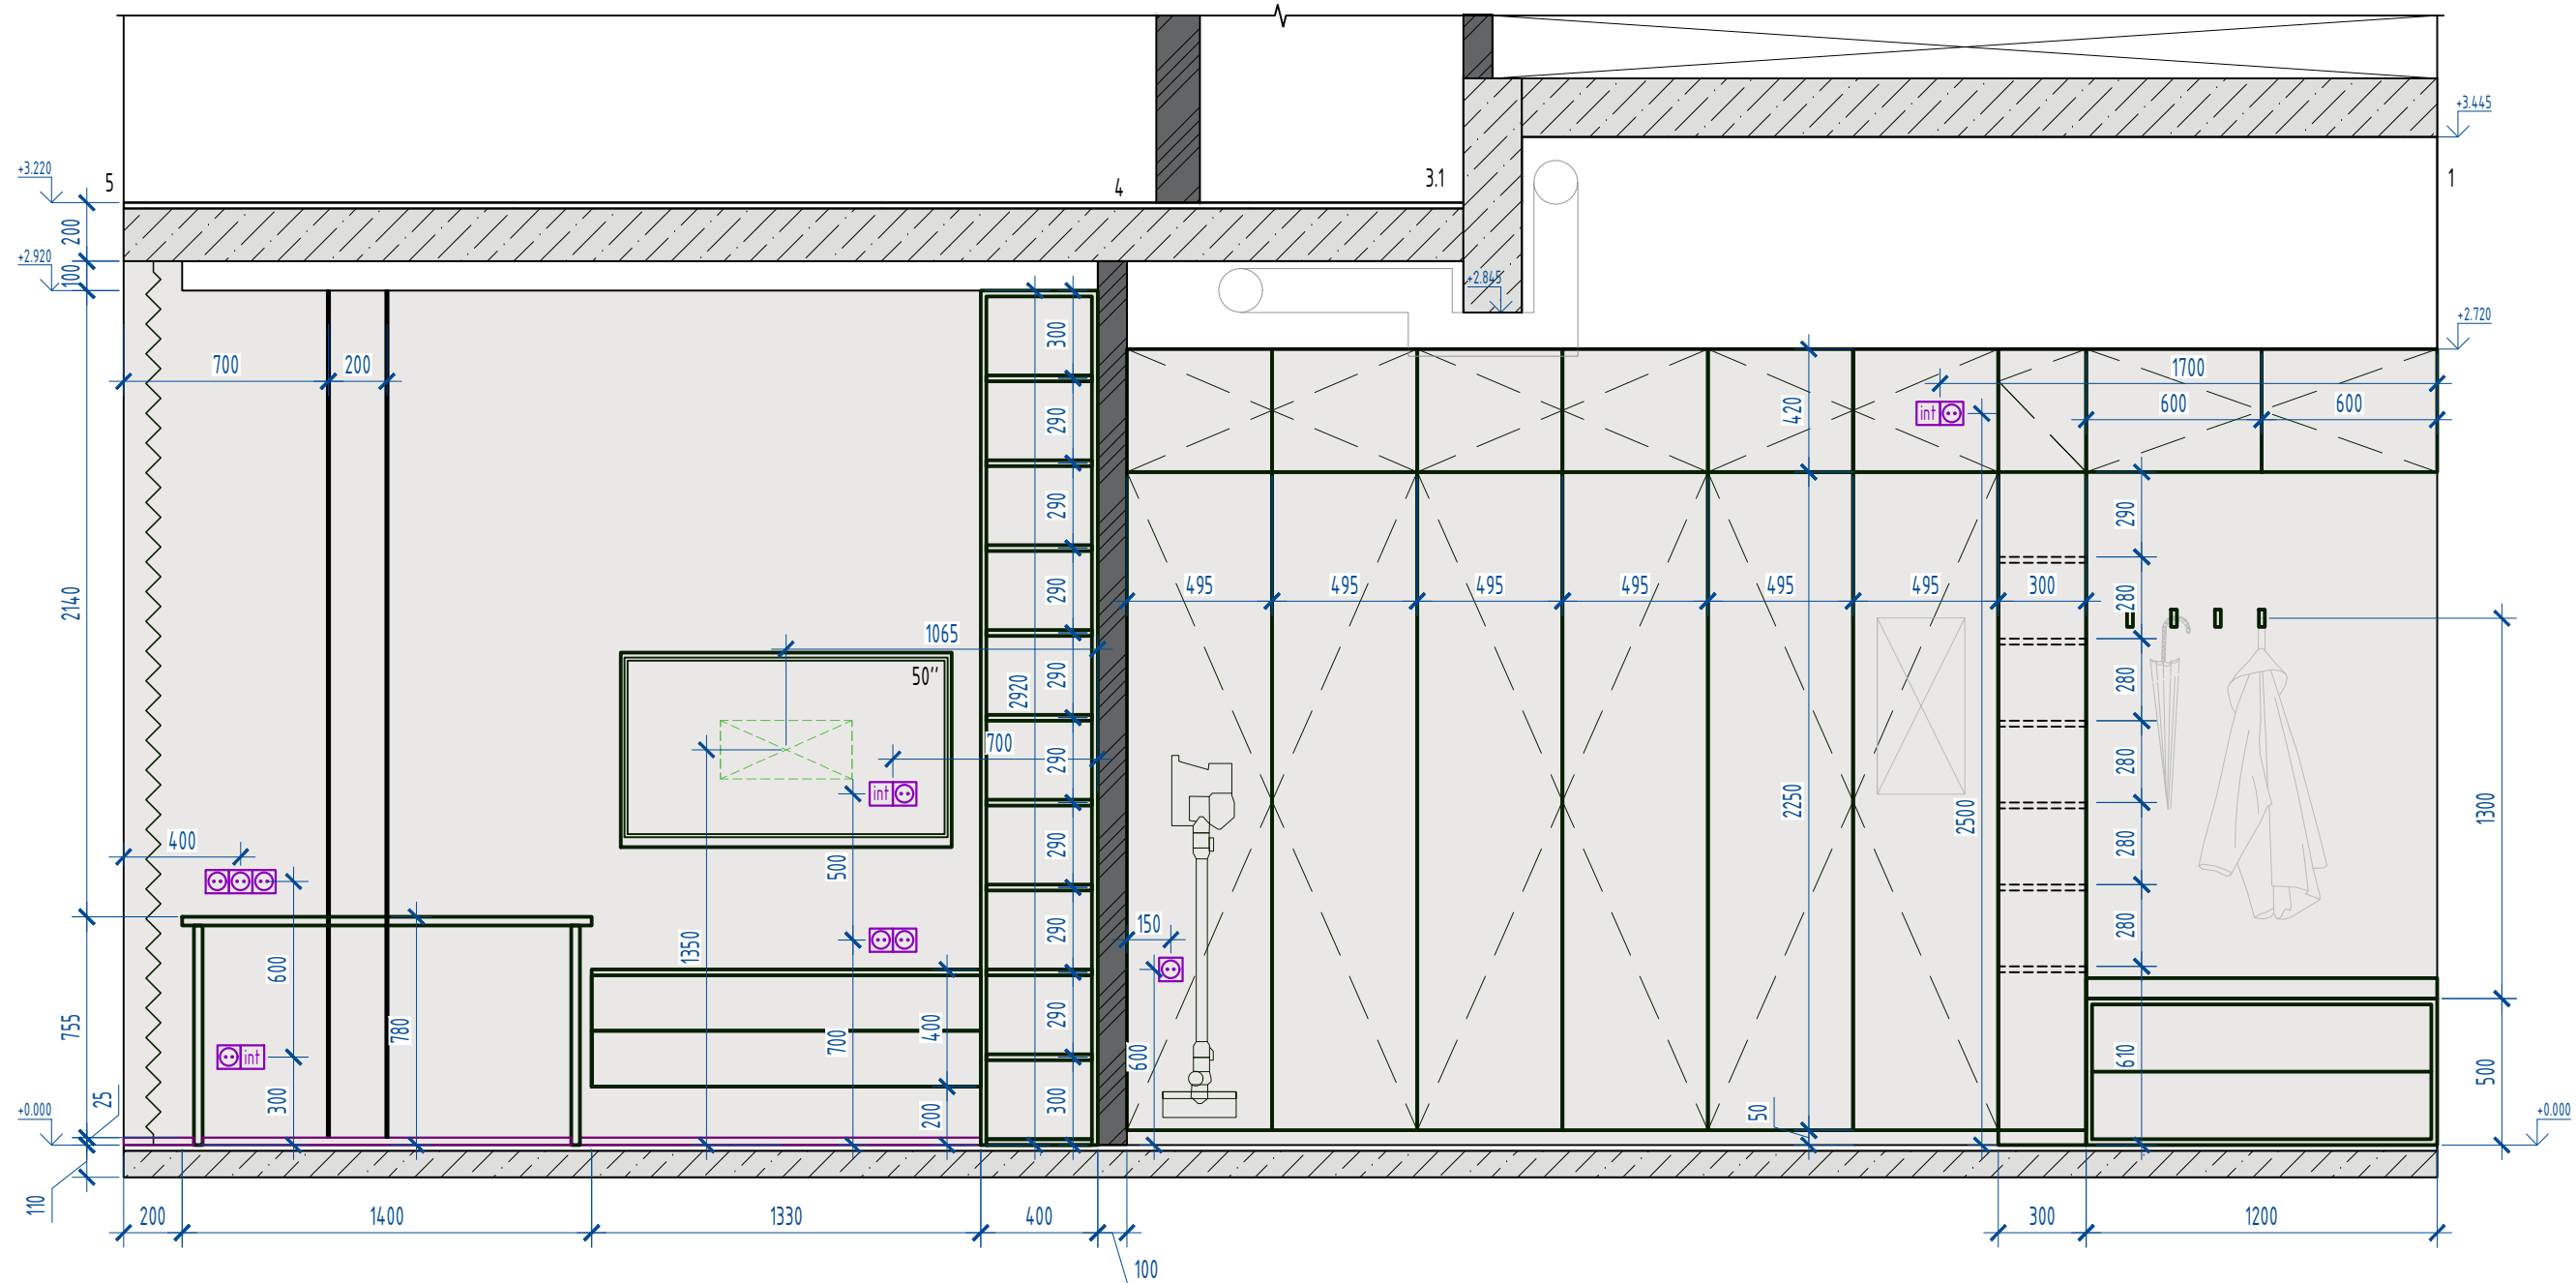


						Развертки 5...1. Прихожая. Гостиная	Лист
Изм.	Кол.уч.	Лист	№ док.	Подп.	Дата		18




Развертка 8-7-6

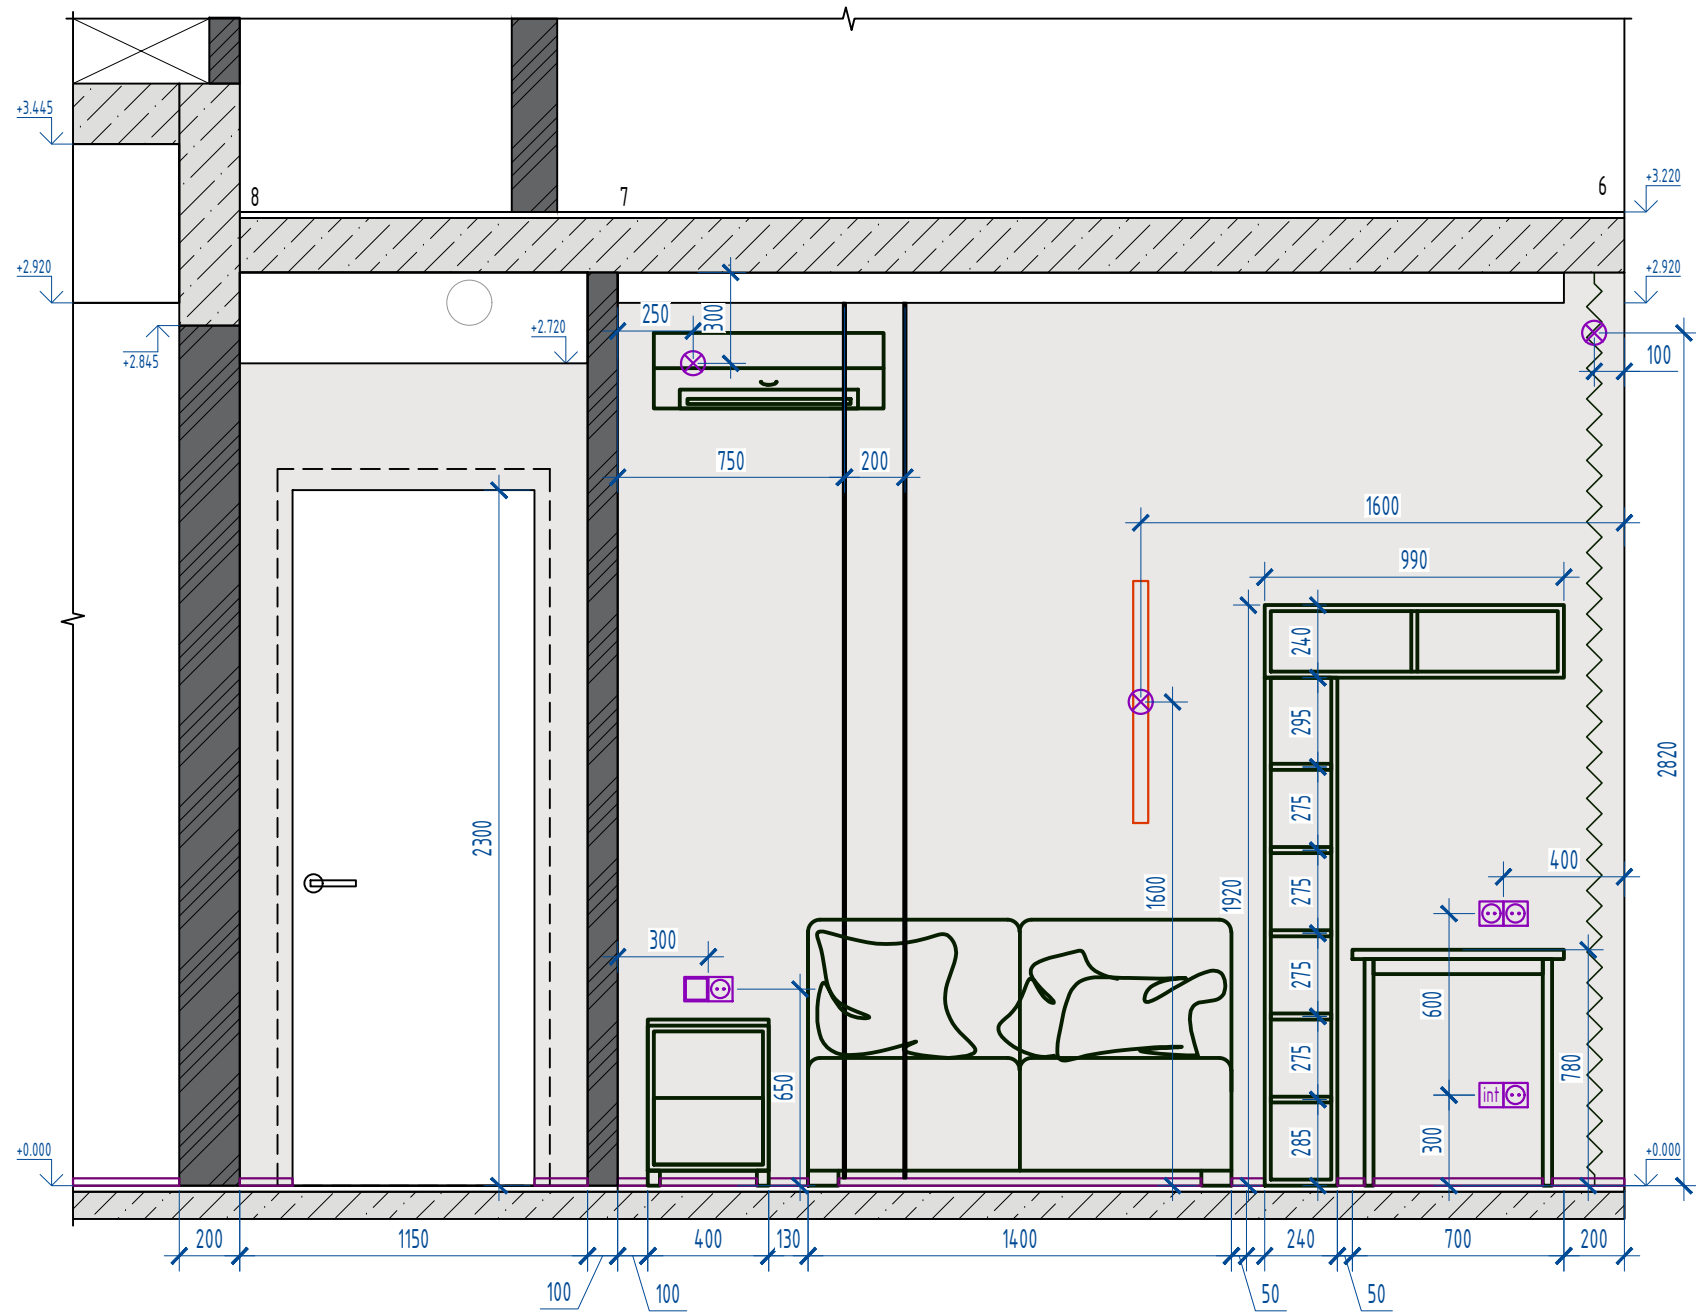

Развертка 11.1-11.2

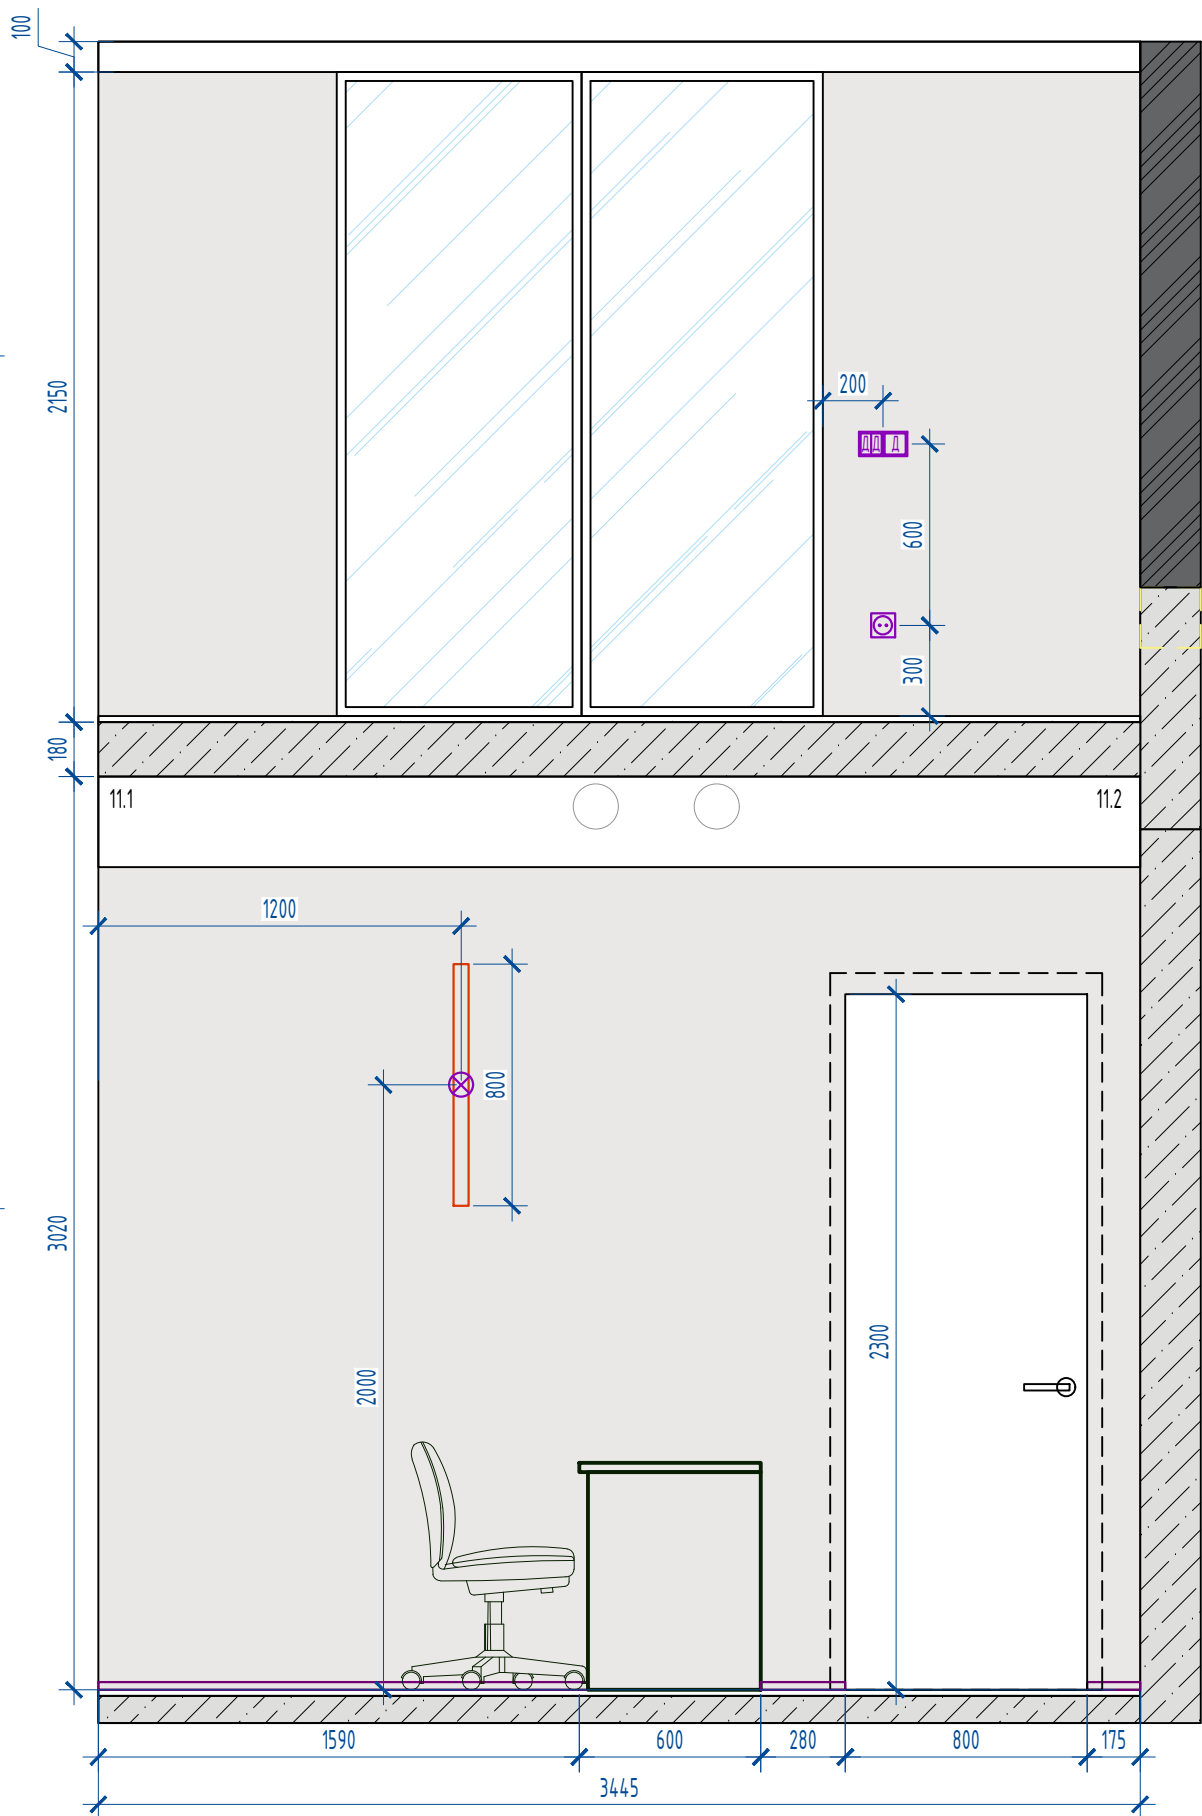

Развертка 4-3-8-9. Развертка 23-24-30-31.

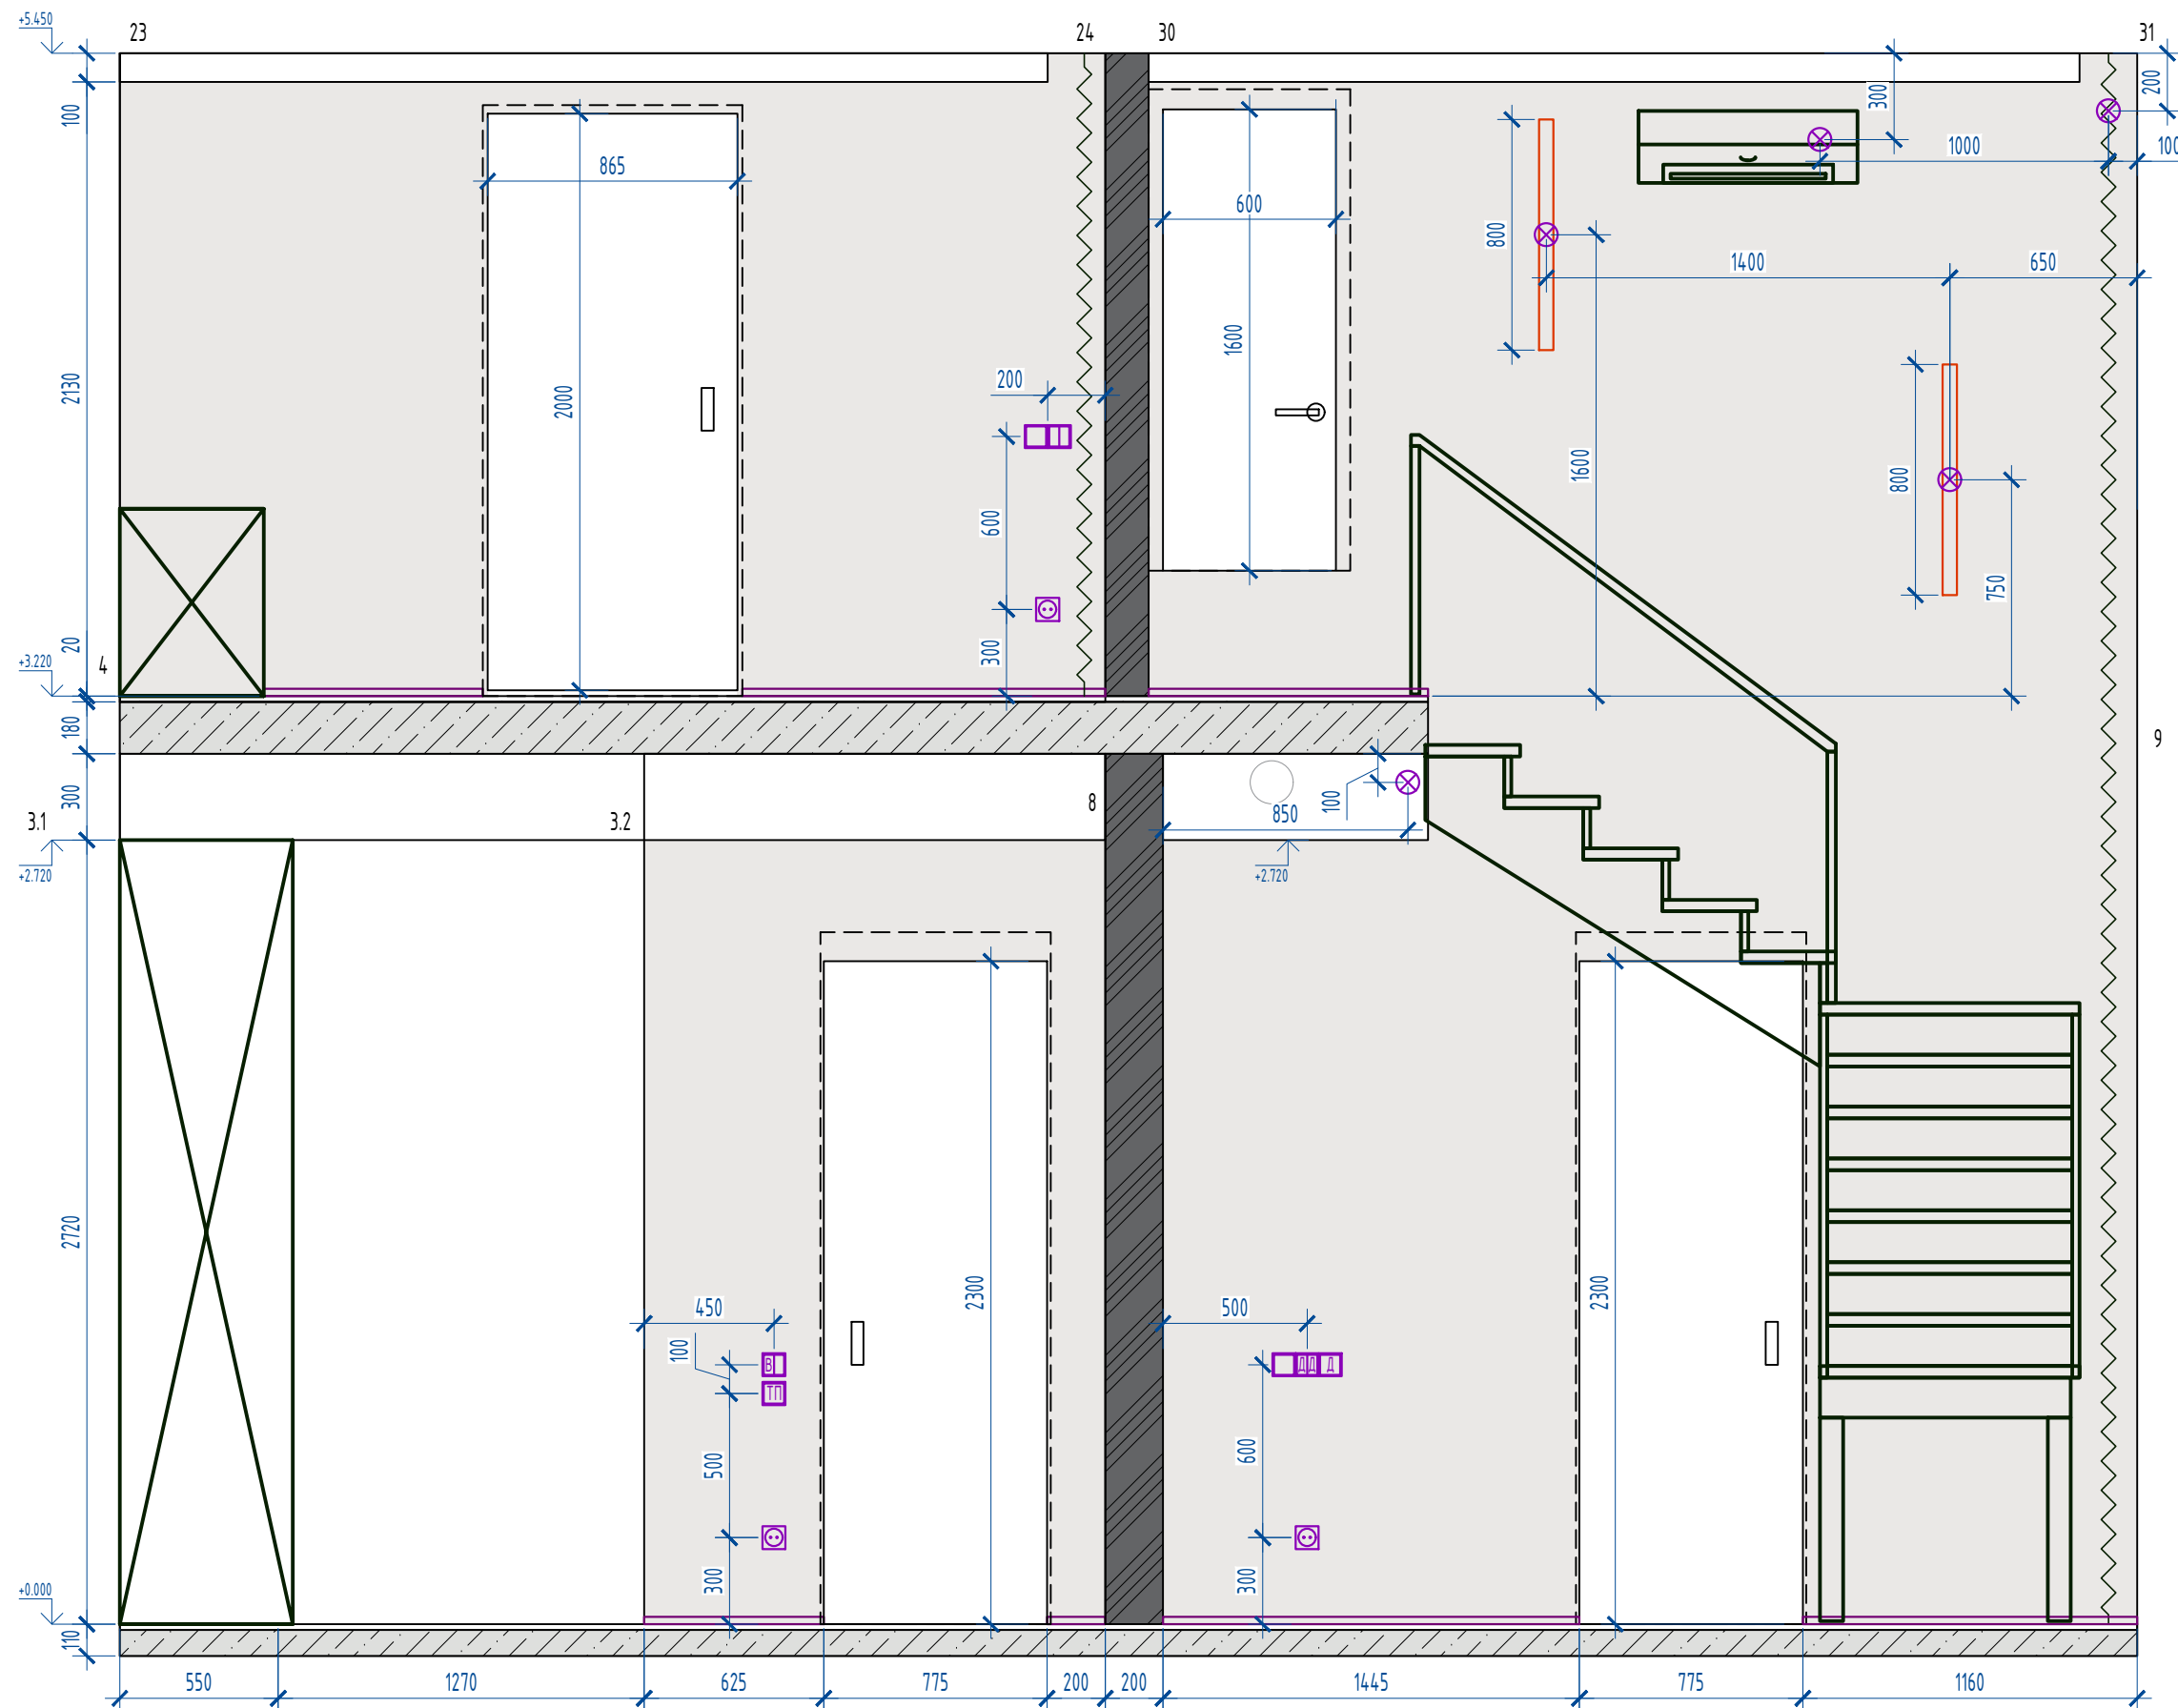

Изм.	Кол.уч.	Лист	№ док.	Подп.	Дата


Развертки 4...9. Гостиная.

Лист  
20


Копировал

Формат А3


Развертка 9-10

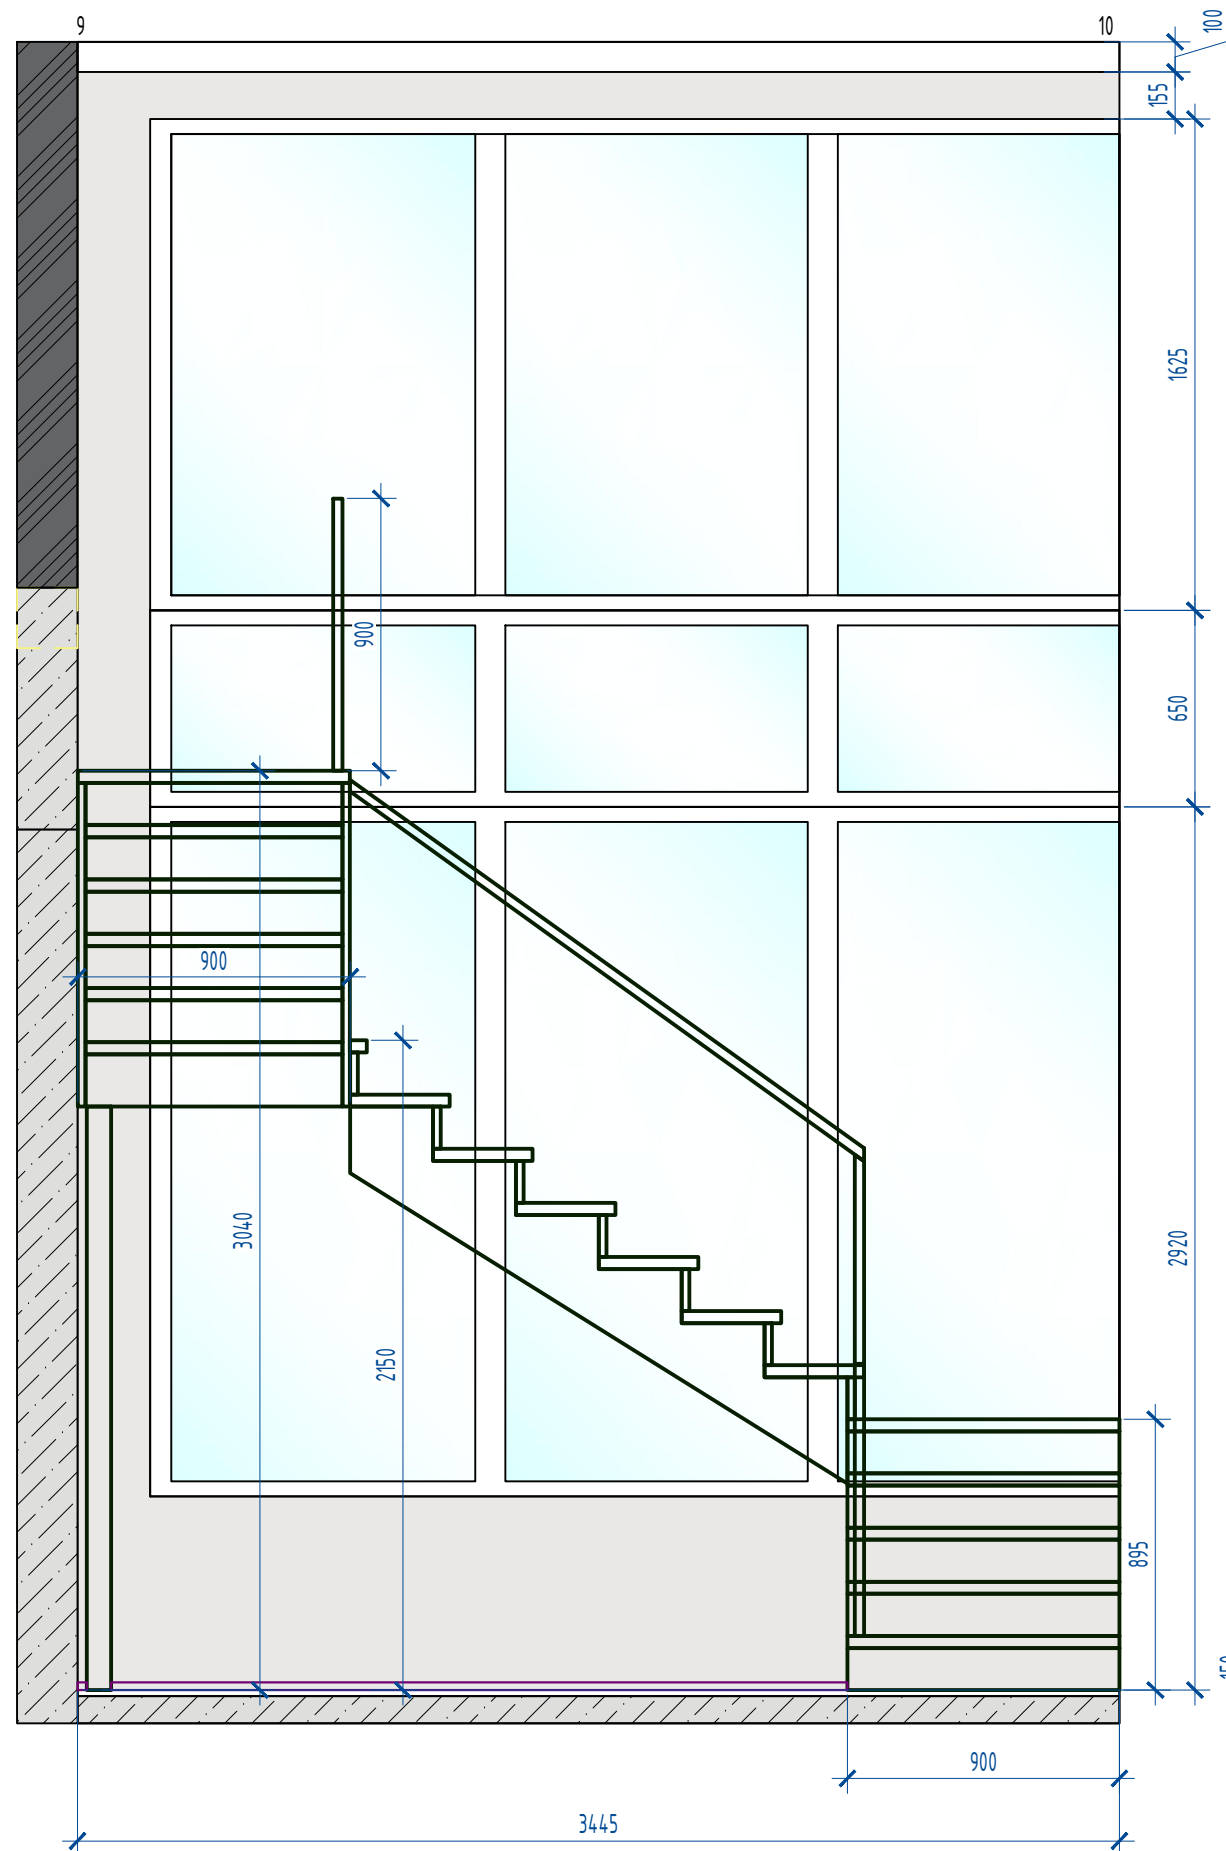

Развертка 9-10

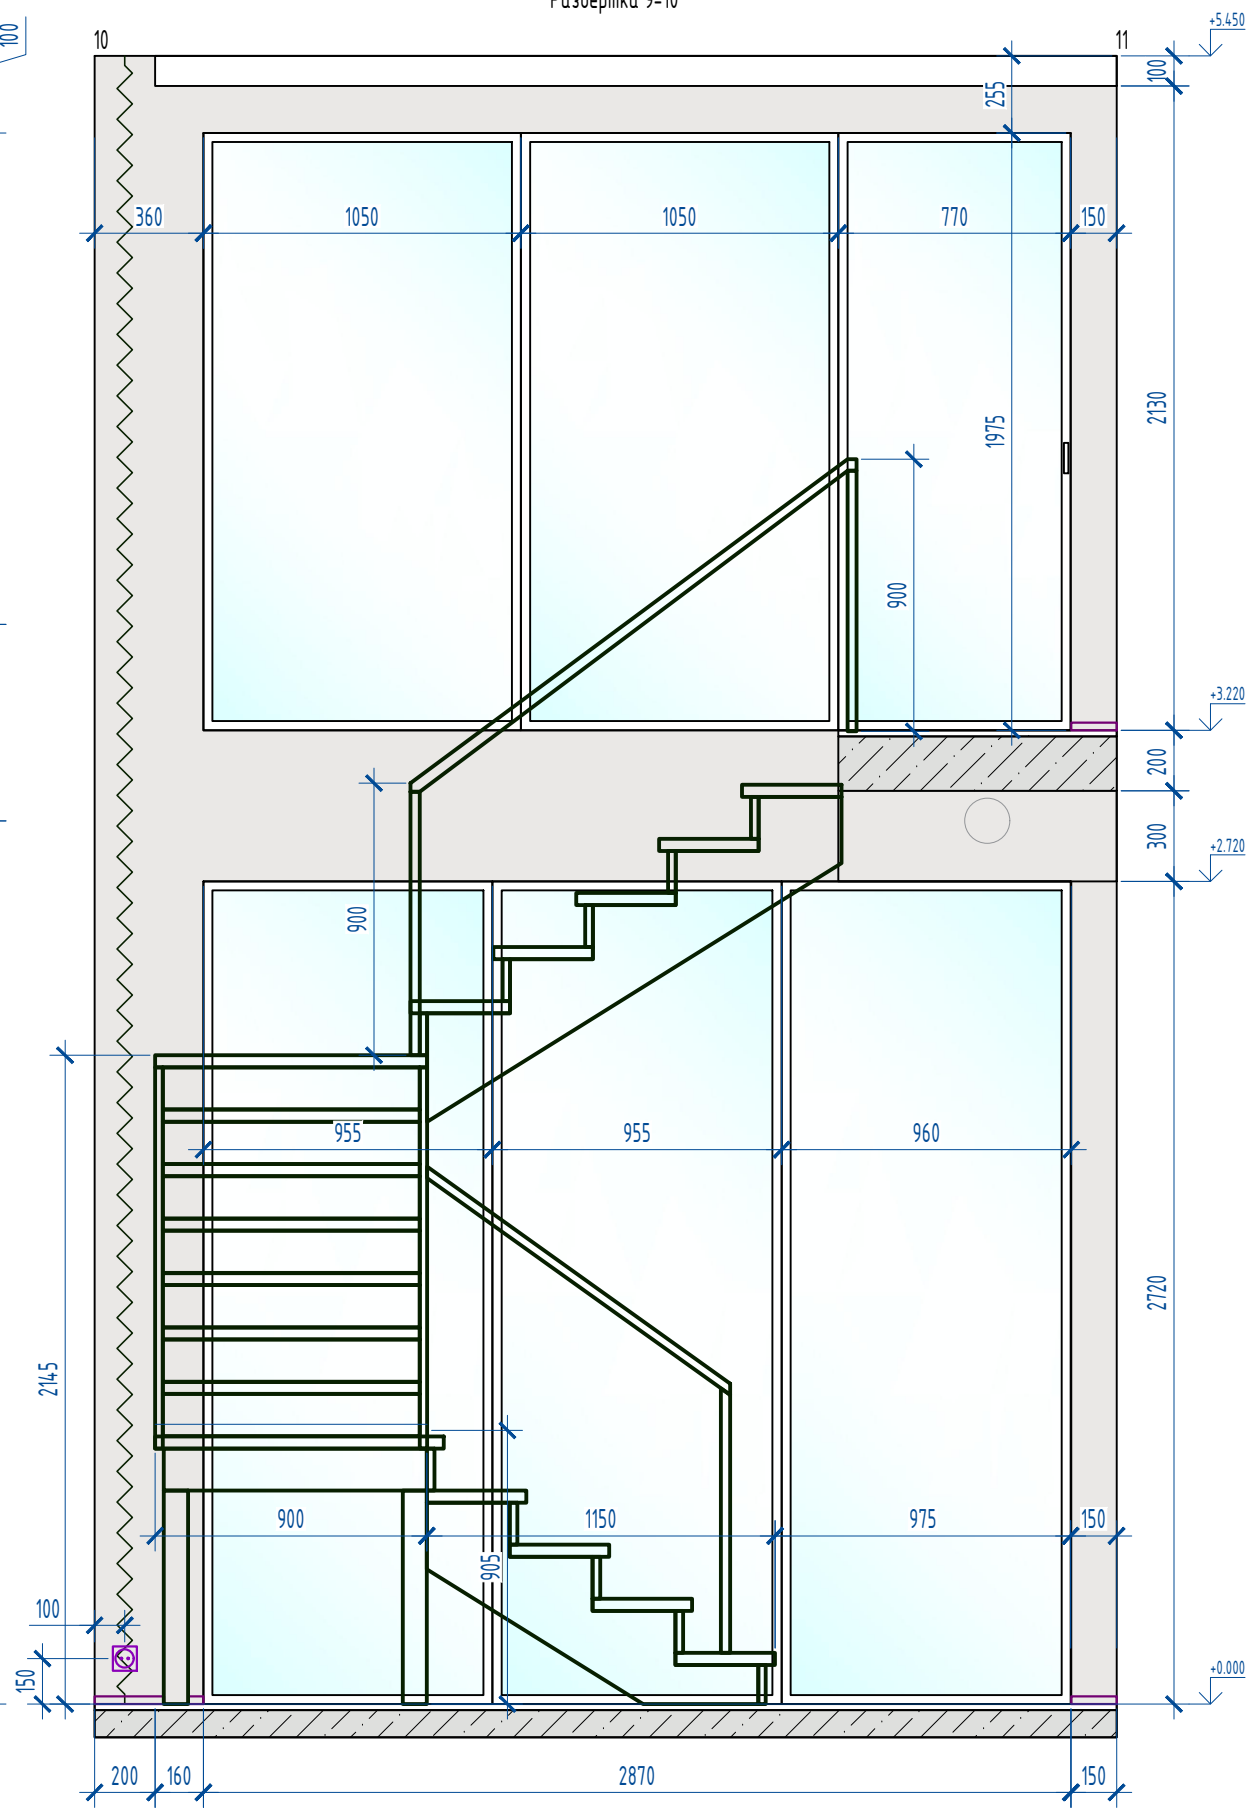

Развертка 12-13

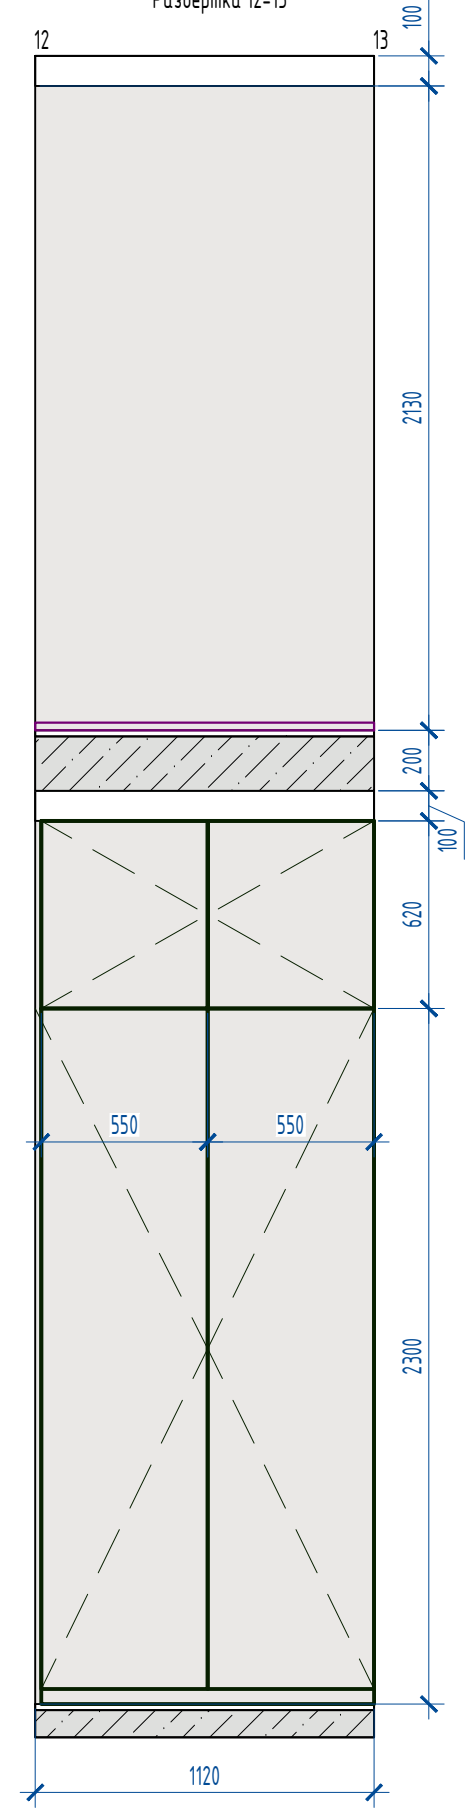

Изм.	Кол.уч.	Лист	№ док.	Подп.	Дата

Развертки 8...10. Гостиная.


Копировал

Формат А3


Лист

21

Развертка 14-15

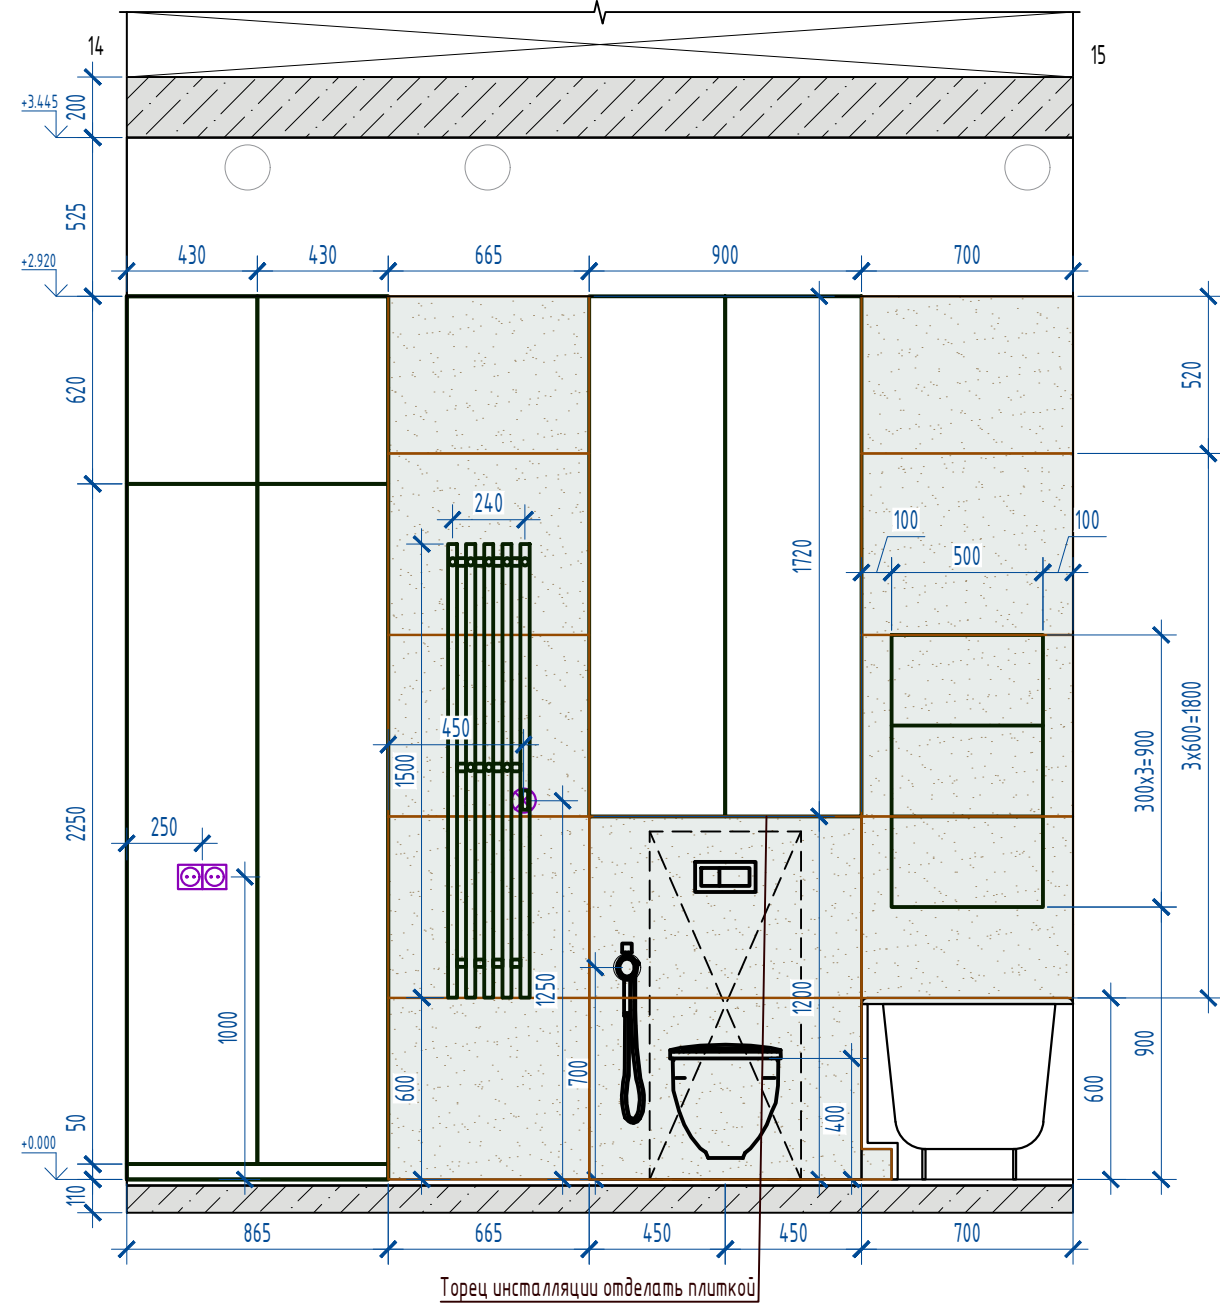

Развертка 15-16


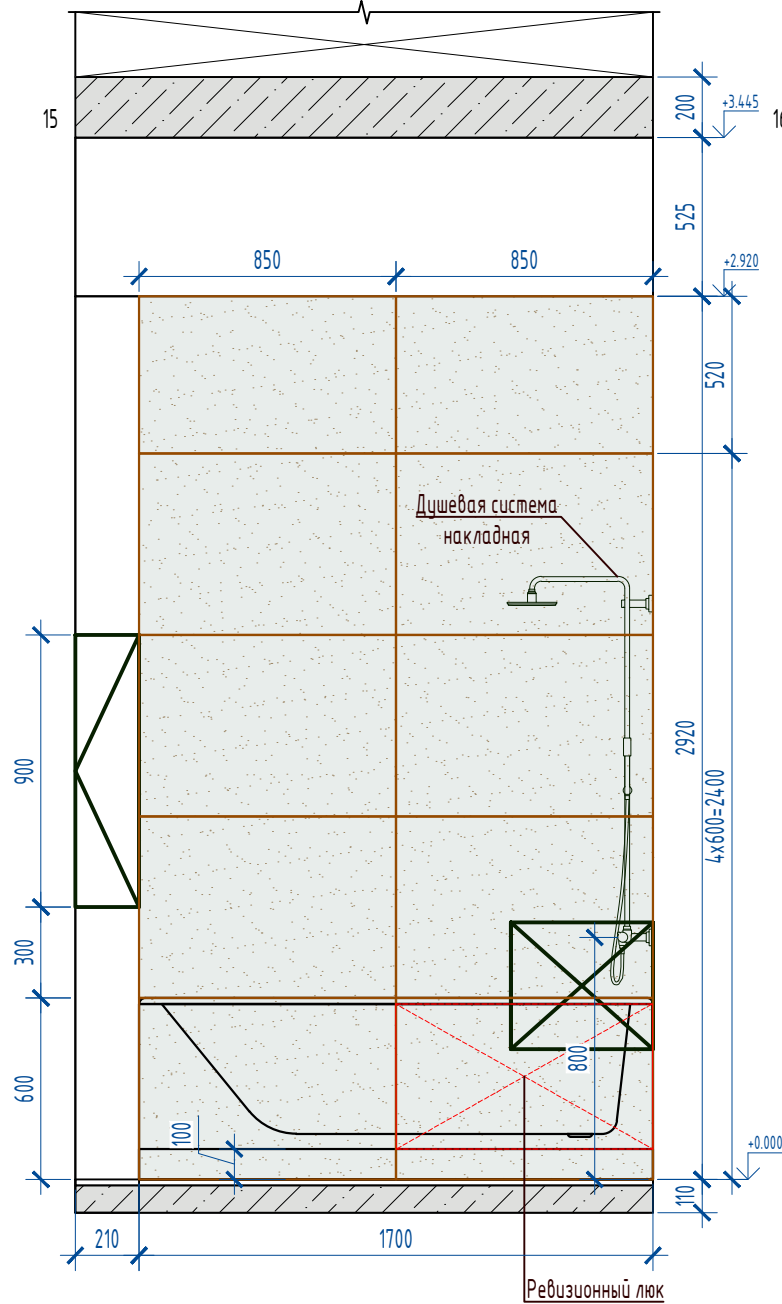


Изм.	Кол.уч.	Лист	№ док.	Подп.	Дата




Развертка 16-17

Развертка 17-14

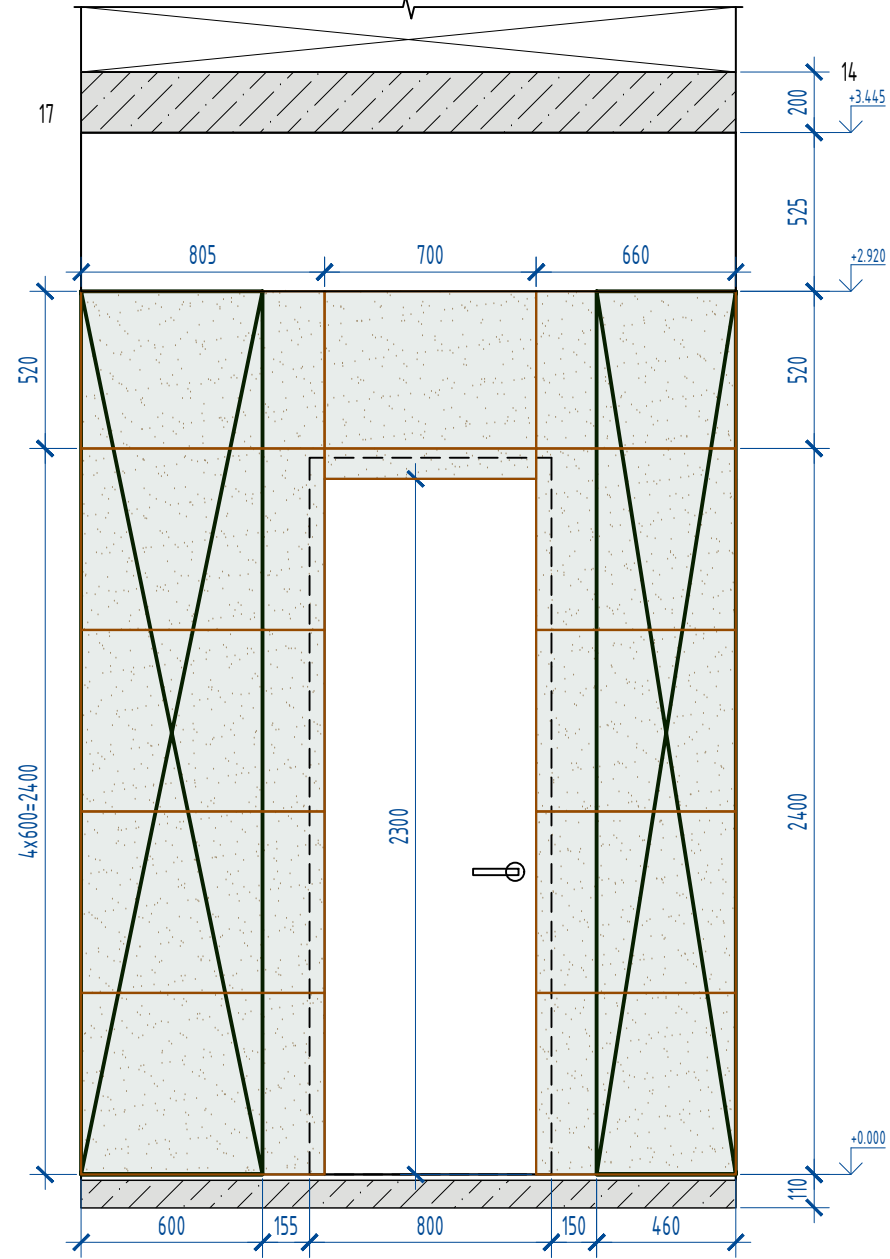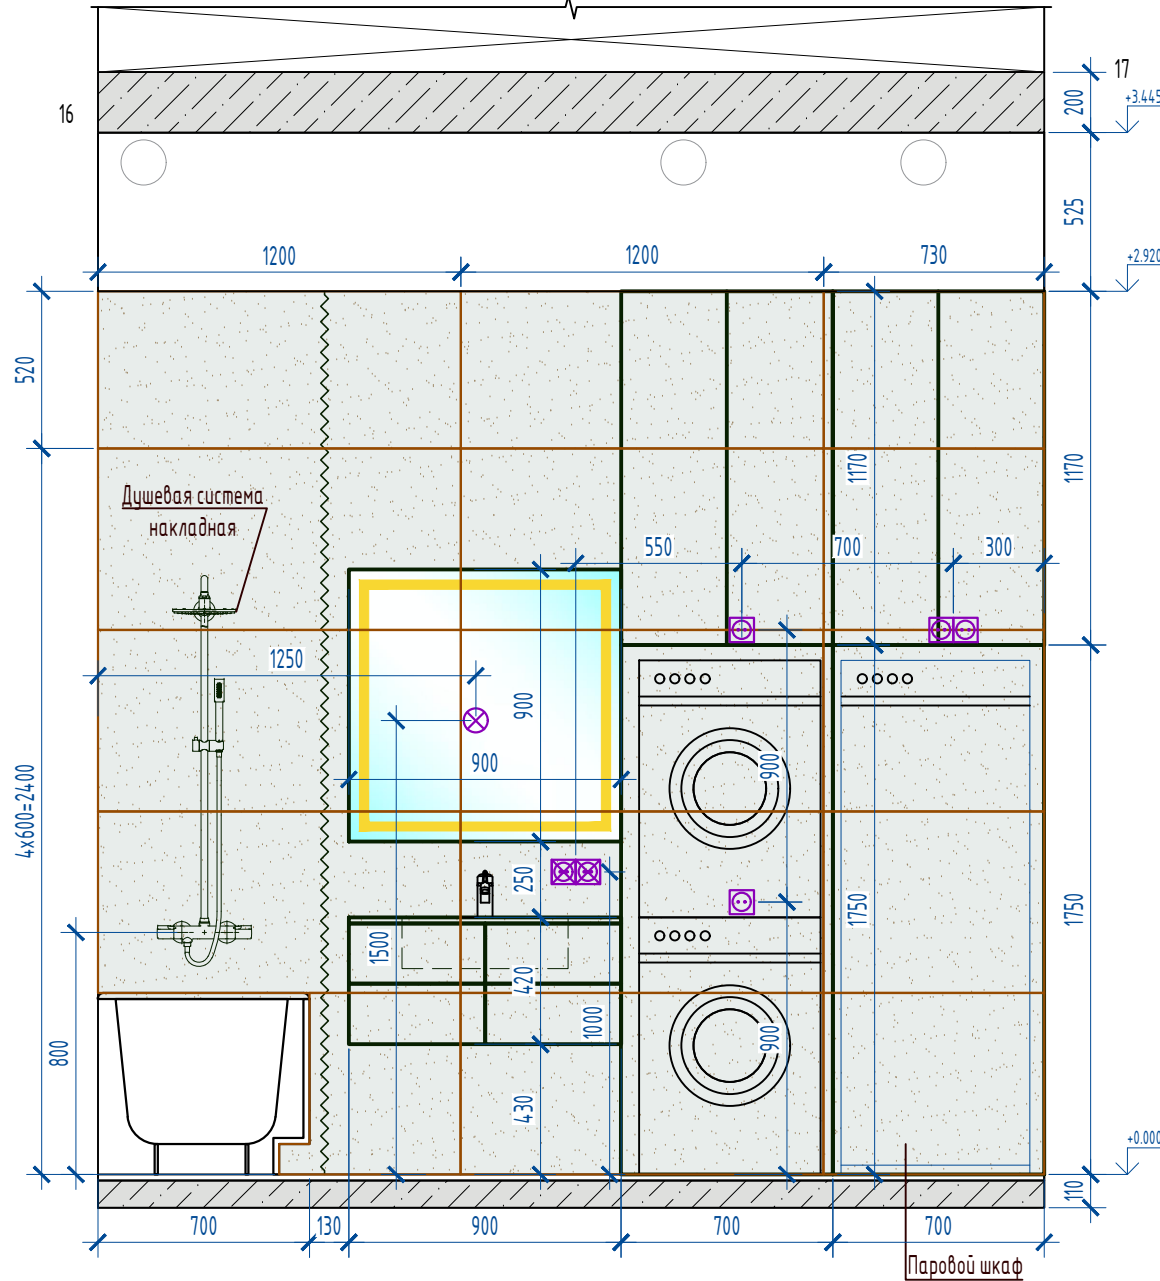


Изм.	Кол.уч.	Лист	№ док.	Подп.	Дата

Развертка 18-19

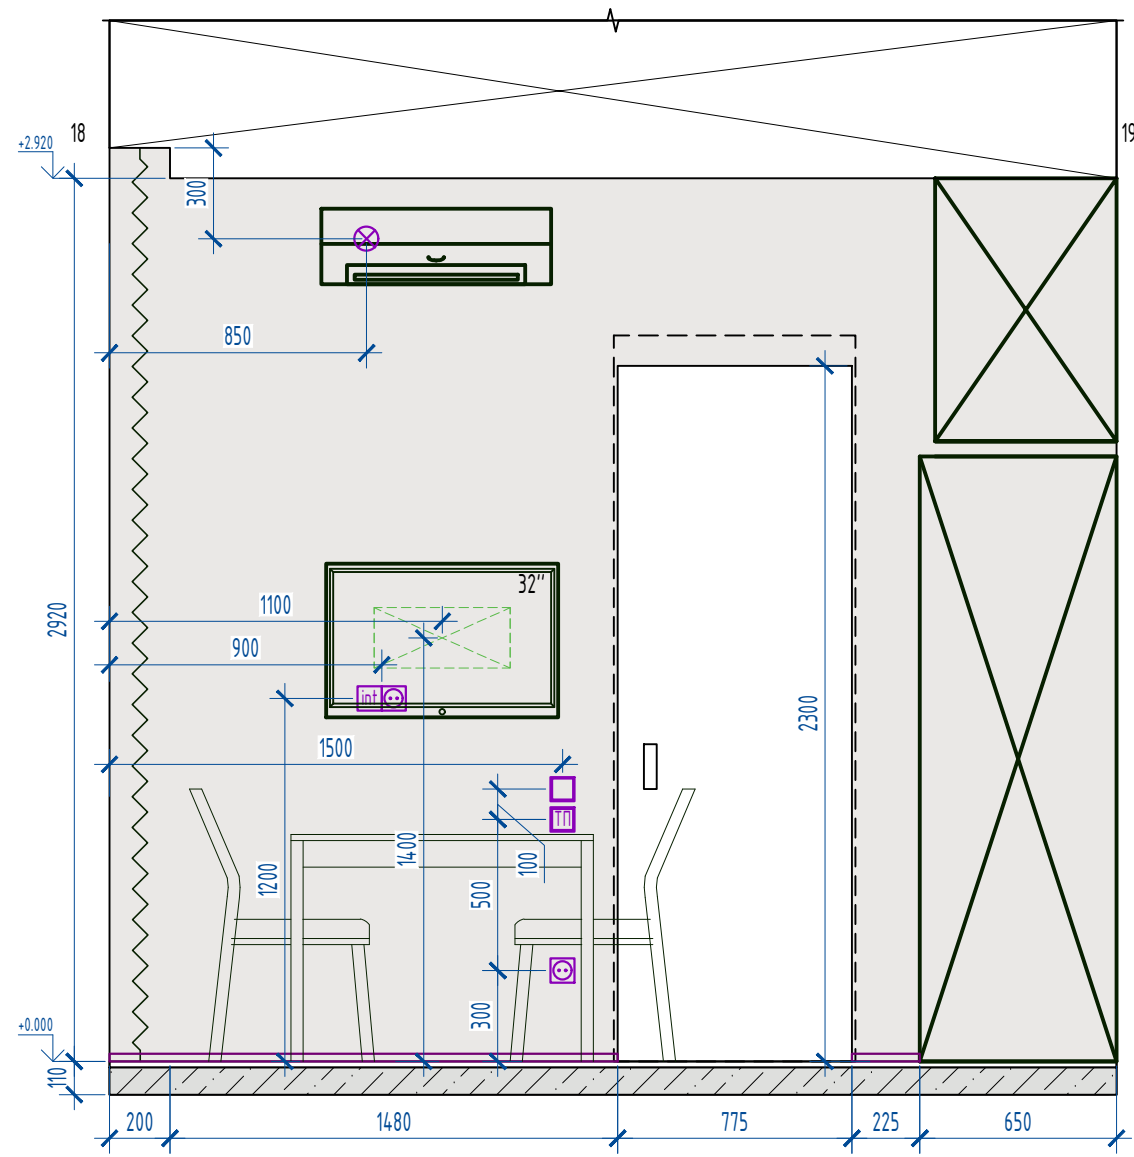


Развертка 19-20





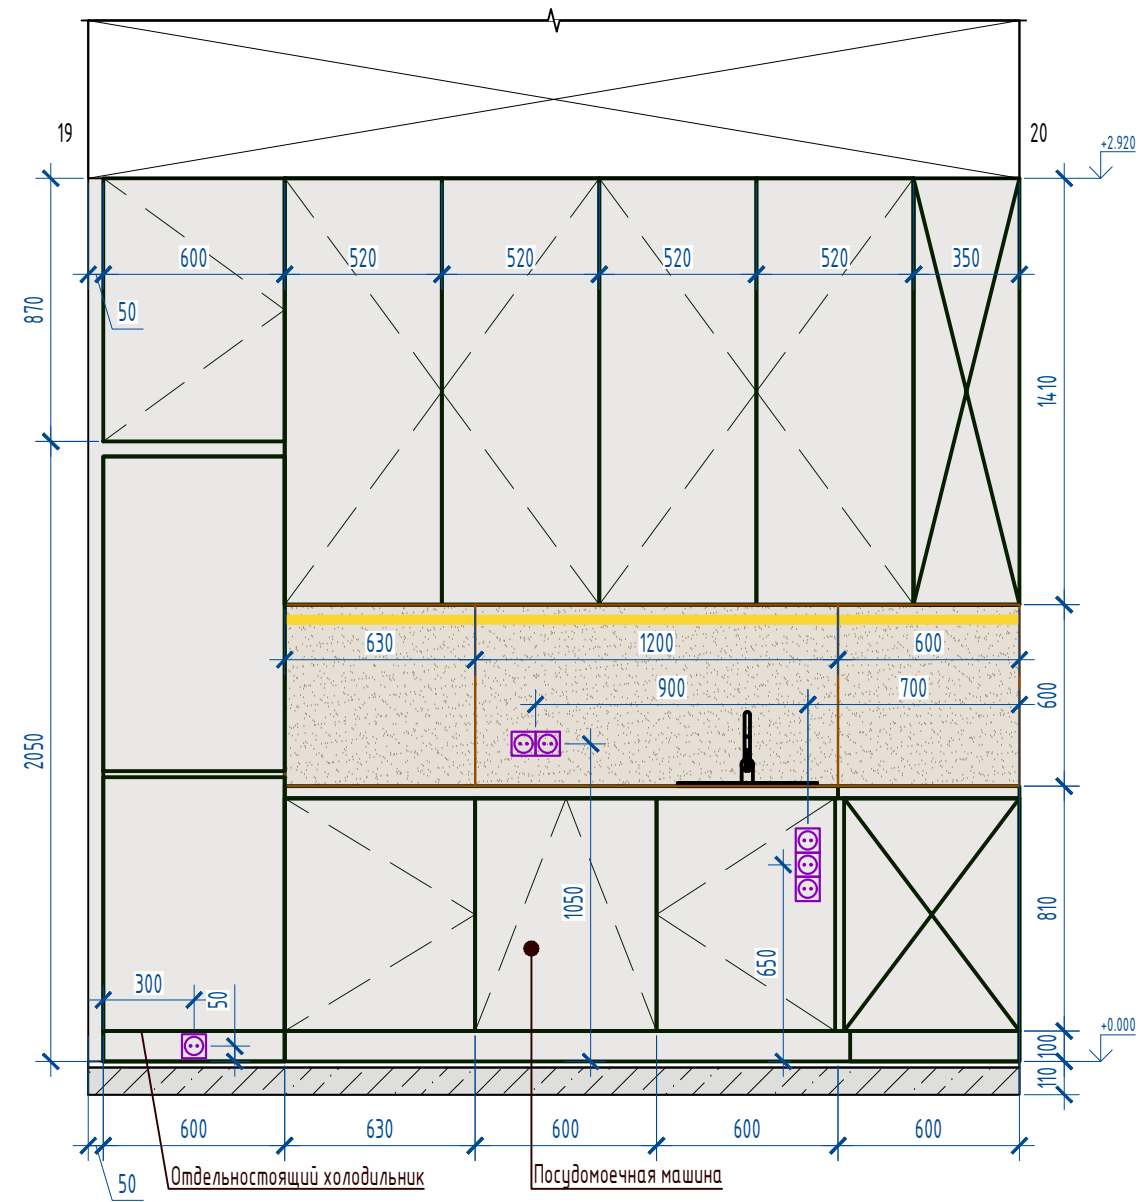


Изм.	Кол.уч.	Лист	№ док.	Подп.	Дата

Развертка 20-21

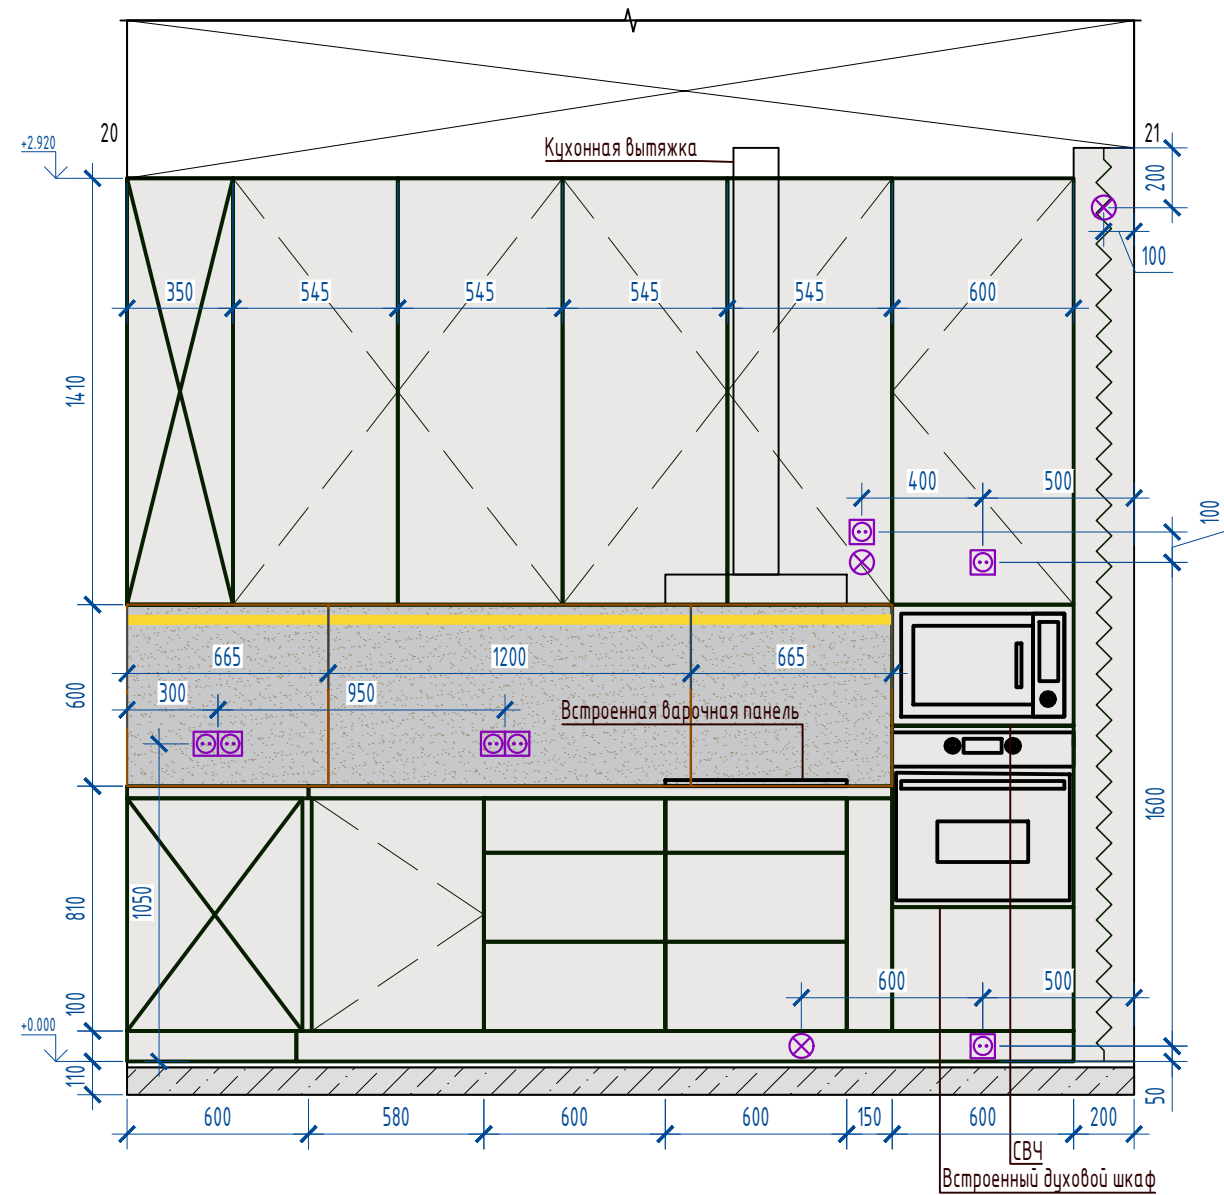

						Развертки 20...21. Кухня.	Лист
Изм.	Кол.уч.	Лист	№ док.	Подп.	Дата		25

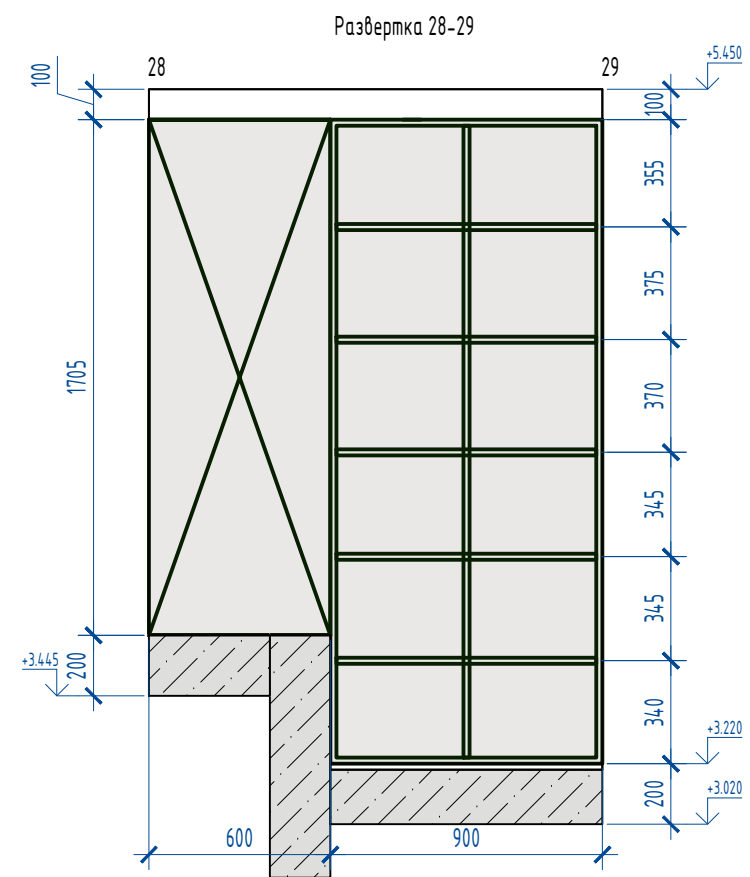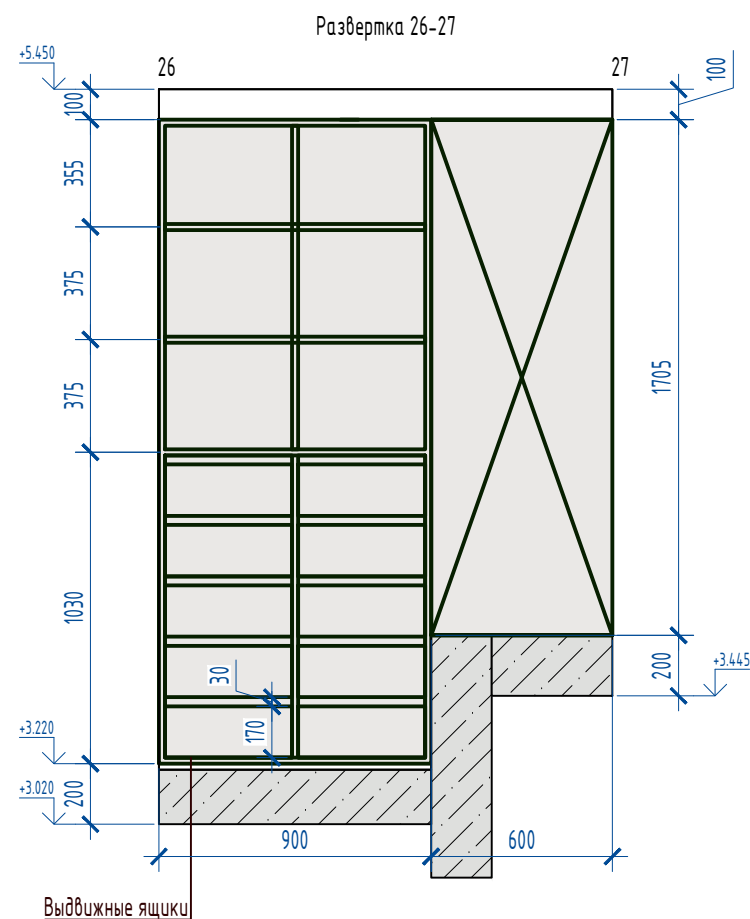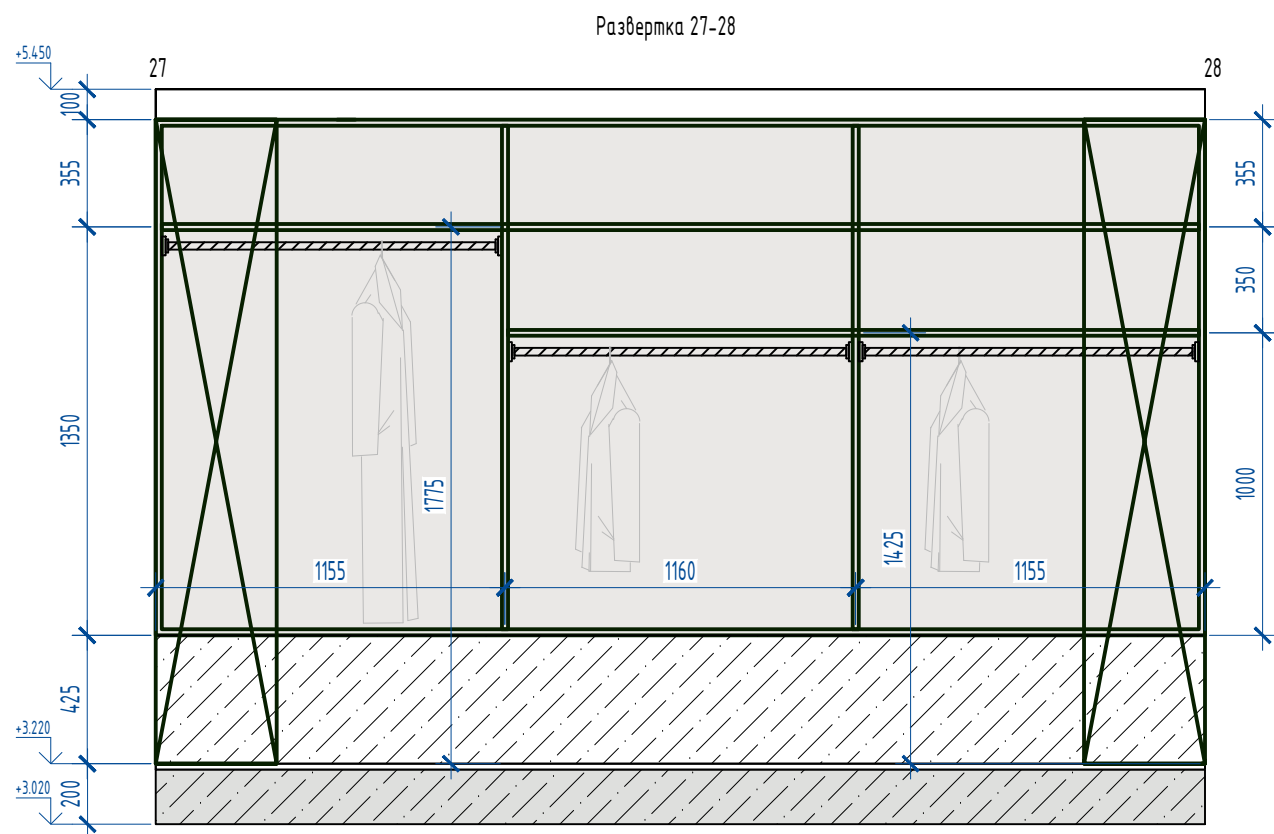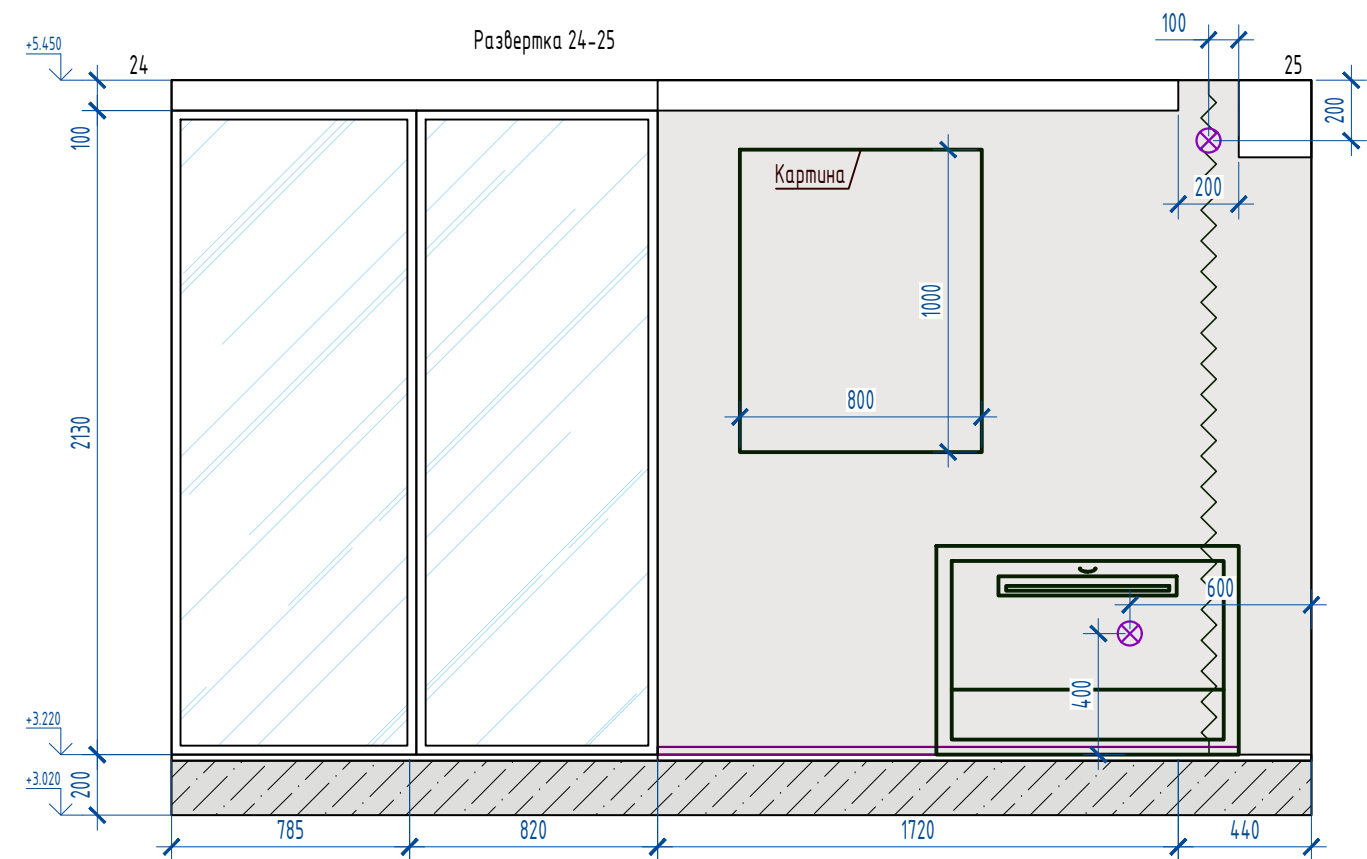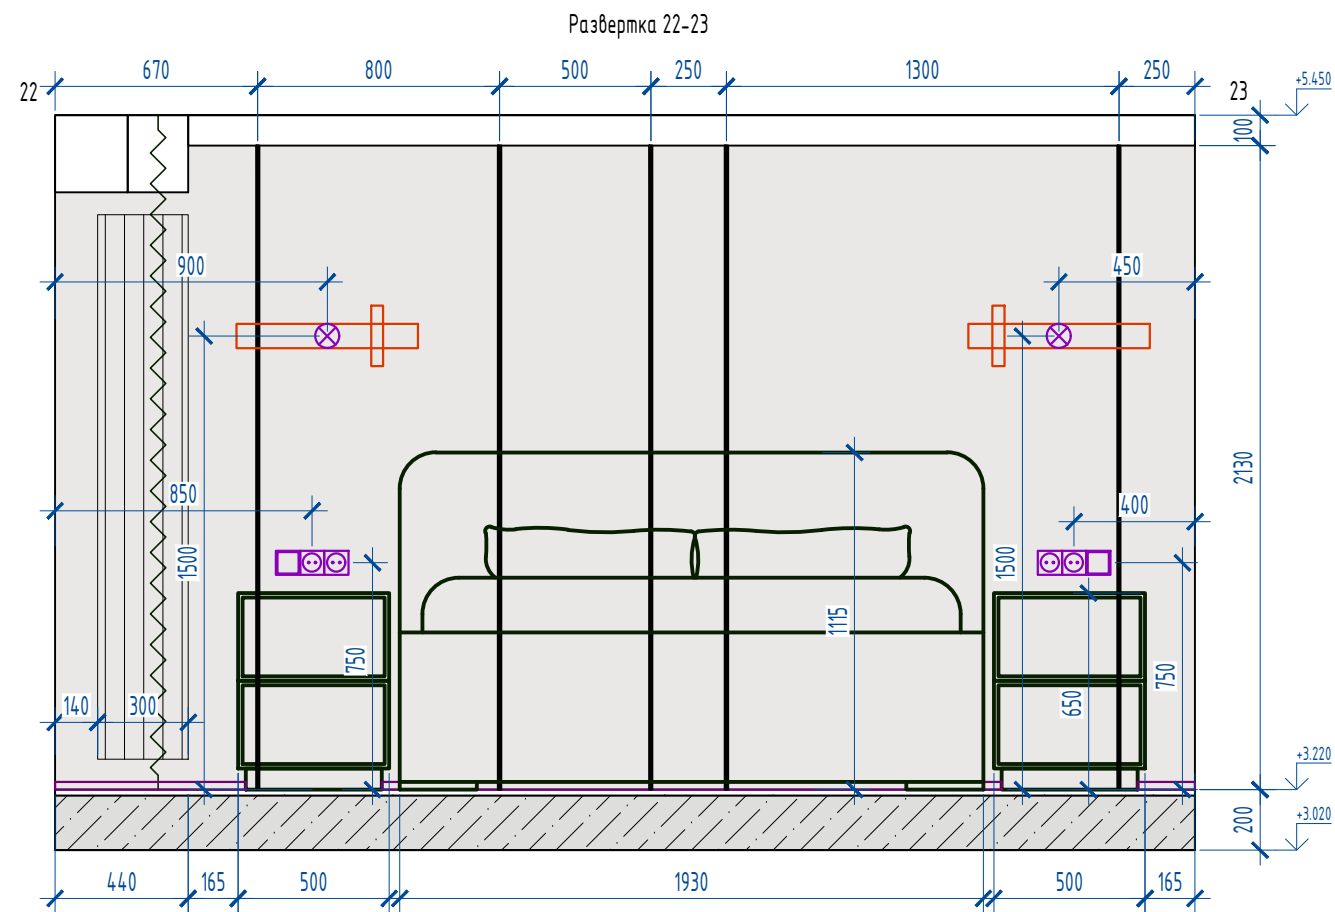

Изм.	Кол.уч.	Лист	№ док.	Подп.	Дата

Развертки 22...29. Спальня.

Лист

26

Копировал

Формат А3